


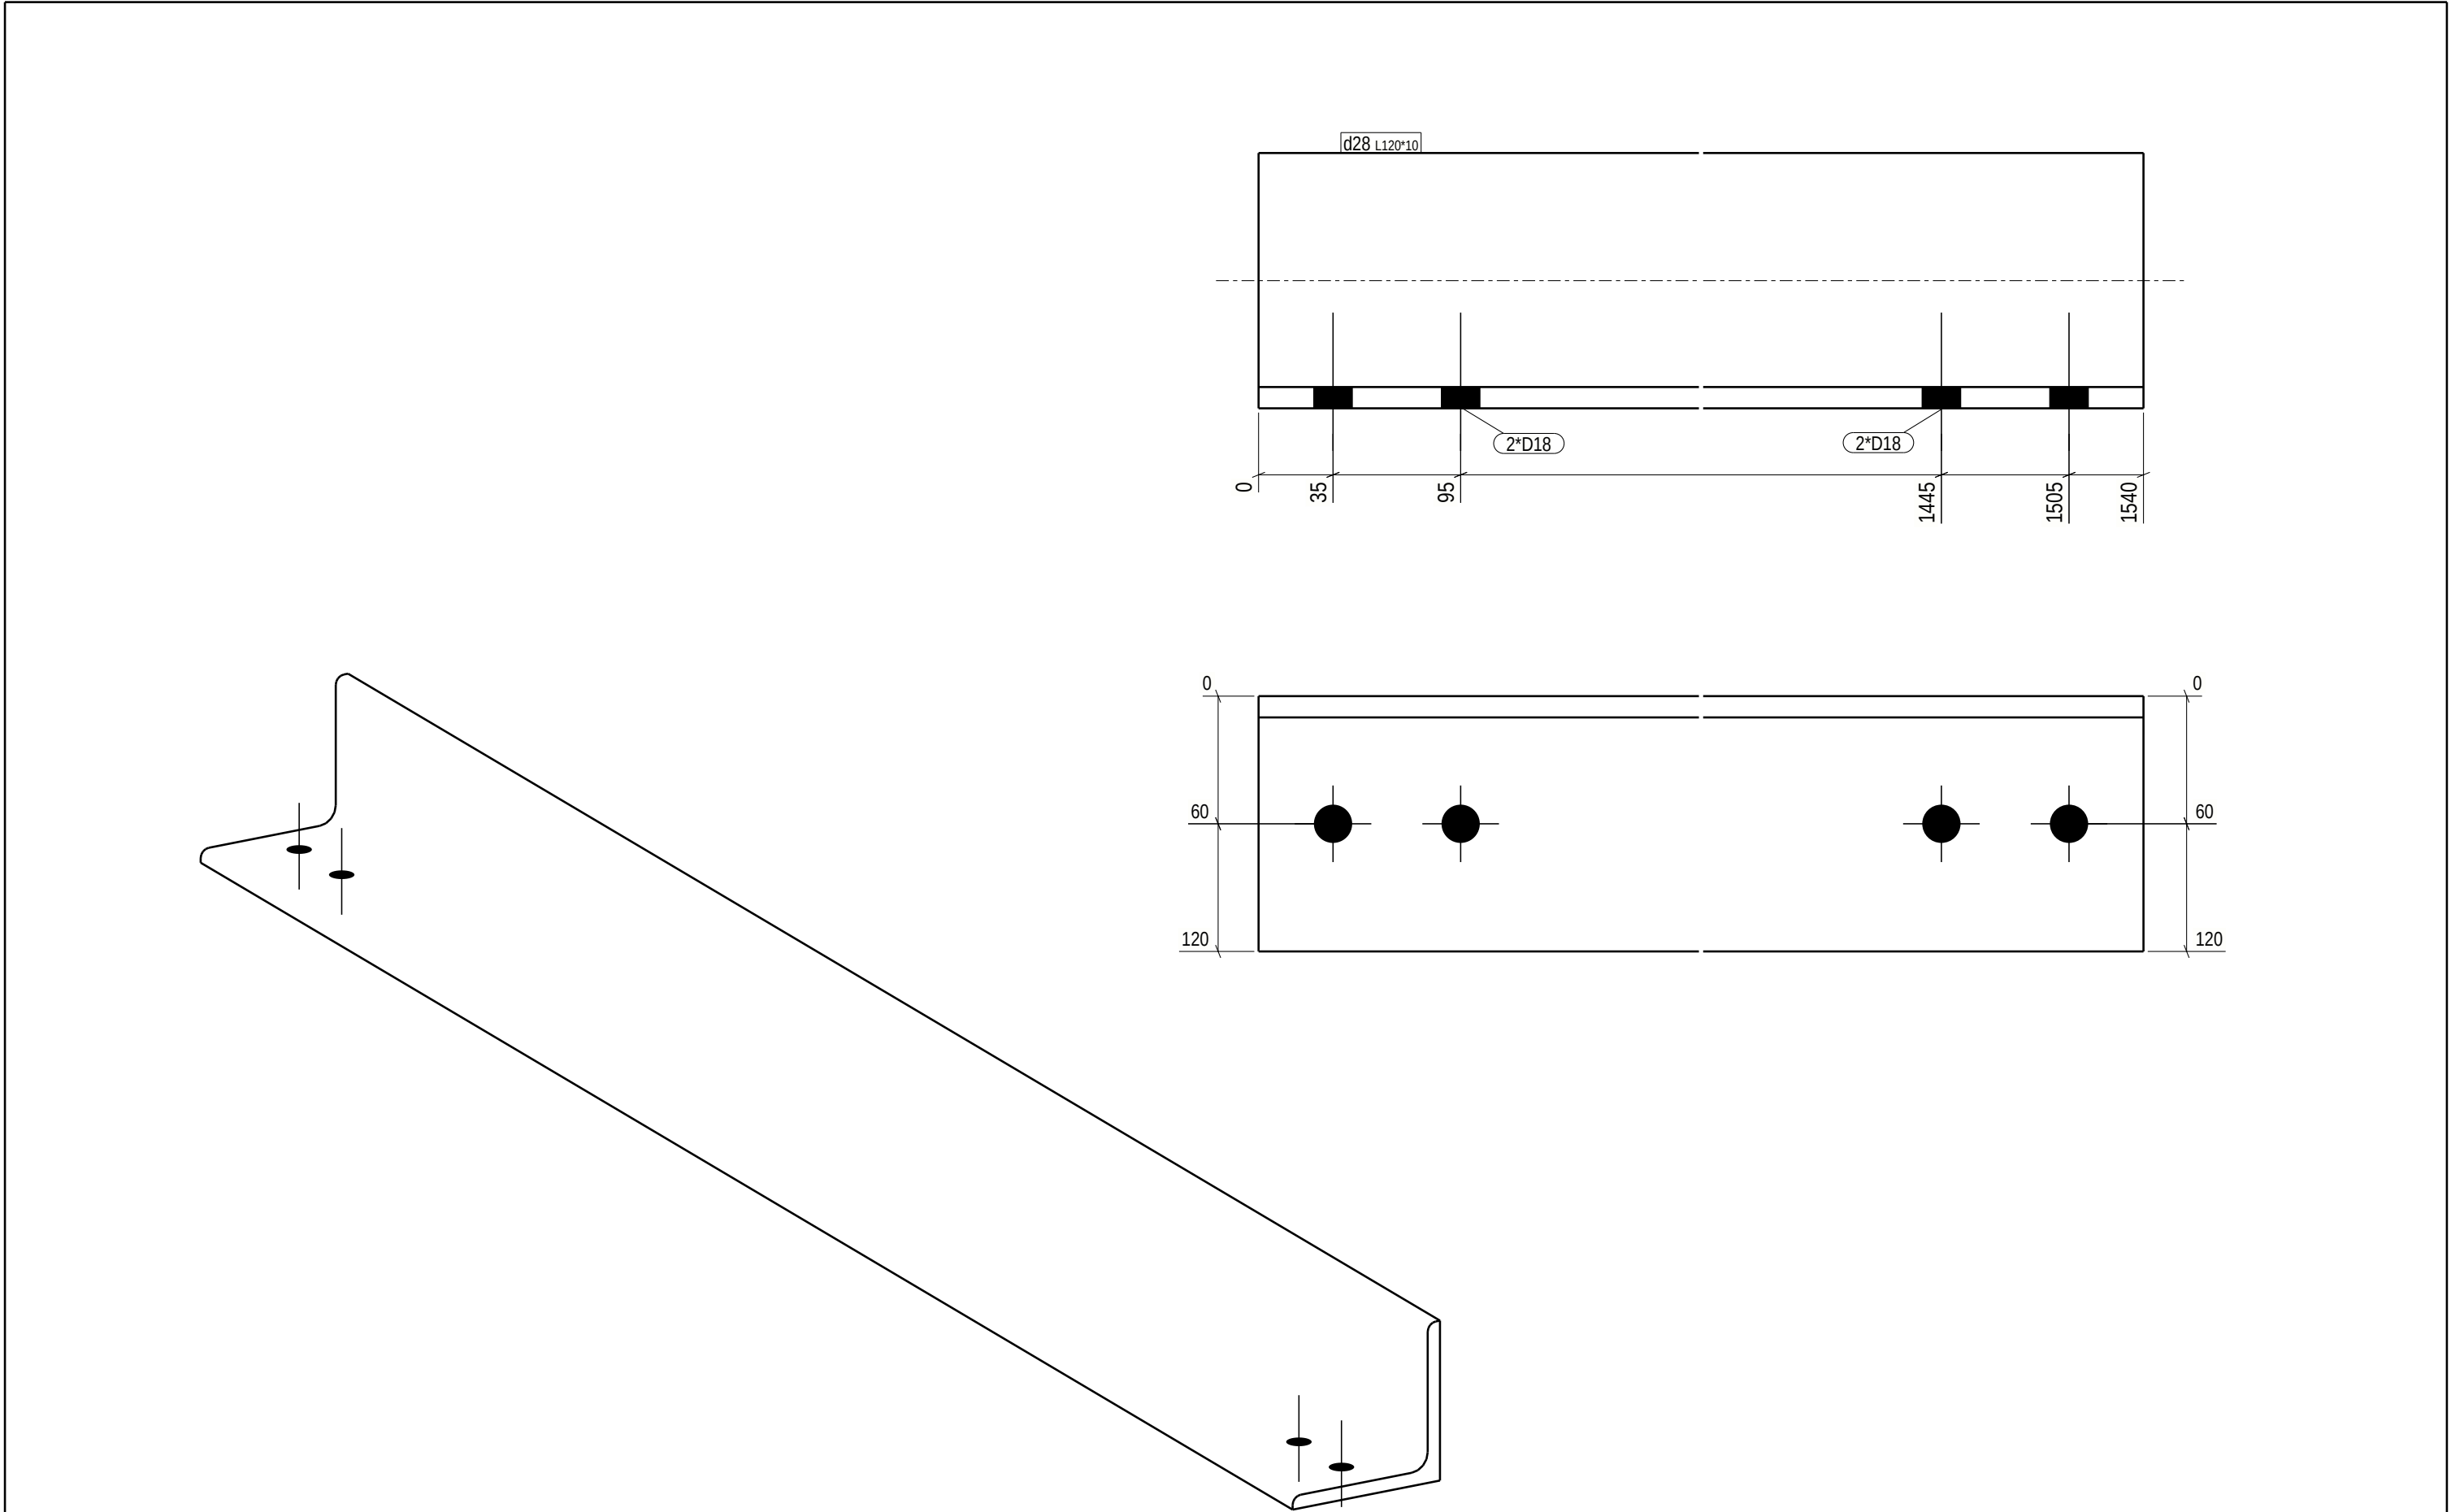

GENERAL NOTES: For your safety, check weight before handling:  
0-5kg Light 5-15kg Normal 15+kg Heavy

ALL WELDS ARE 4 UNLESS NOTED ON DRAWING

| MATERIAL LIST FOR ASSEMBLY MK'D <b>d.28</b> |         |          |     |        |      |         |
|---------------------------------------------|---------|----------|-----|--------|------|---------|
| Mark                                        | Profile | Material | No. | Length | Area | Weight  |
| d28                                         | L120*10 | S355J2   | 1   | 1540   | 0.7  | 28.0 !! |
| Total                                       |         |          |     | 0.7    | 28.0 |         |

Finish Class  
Standard

|                         |                                 |     |
|-------------------------|---------------------------------|-----|
| Surface treatment info: | Thickness/start point--> length | No. |
| Galvanised              | /                               | 8   |



Special  
surface treatment



weld a = 4

| PHASE | QUANTITY |
|-------|----------|
| 3     | 8        |

|   |                                      |              |             |
|---|--------------------------------------|--------------|-------------|
| * o 3 0 4 8 0 - 3 *  <b>DS</b> <i>Stalkonstruktion</i> * A d 2 8 * |                                      |              |             |
| PROJECT   | Akkasæter Lager- og vedlikeholdshall |              | EXEC. CLASS |
| MEMBER   | Drager                               |              | PROJECT No  |
| REVISION   | ISSUED: 05.11.2025                   |              | DRAWING No. |
| QUANTITY: 8   |                                      | DRAFTER: ZLL | d.28        |
| BIM control: SST   |                                      | EXC 2        |             |