
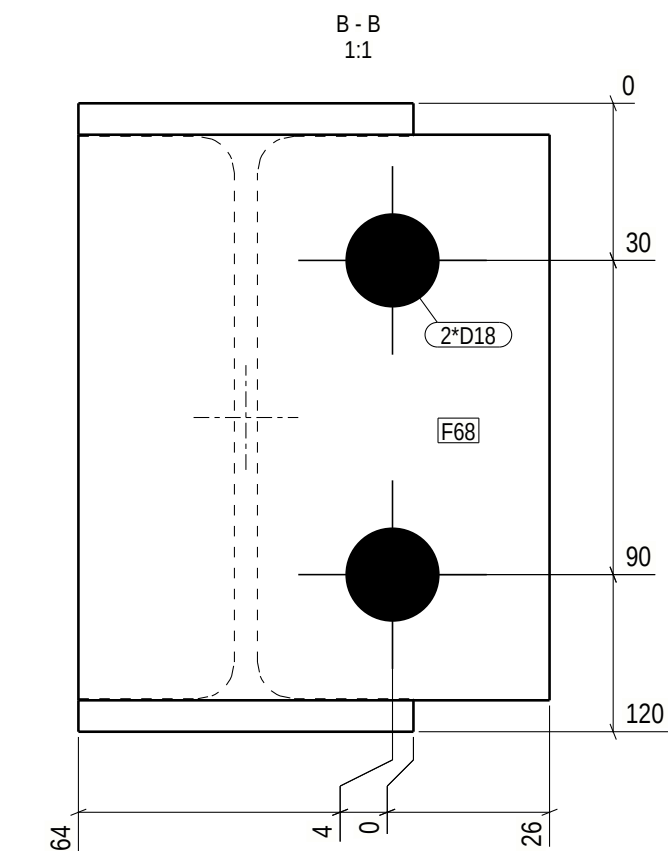
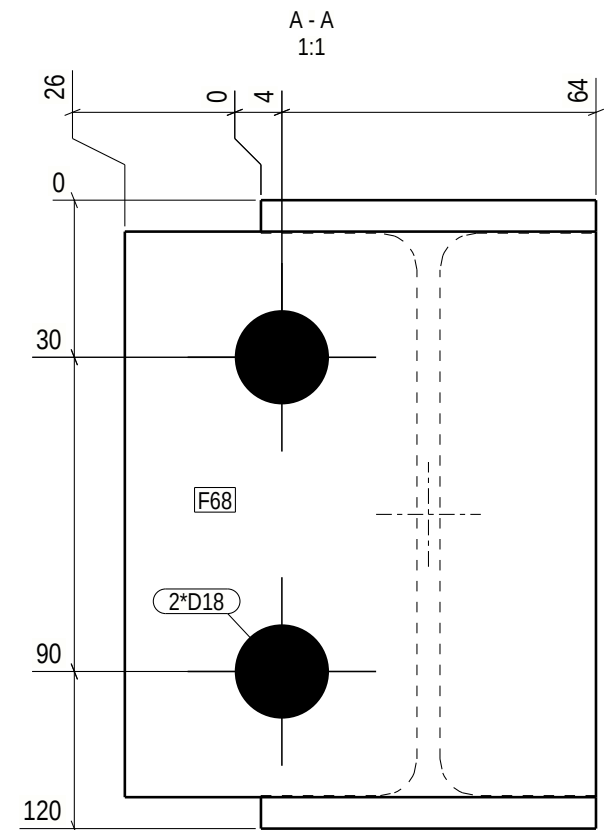
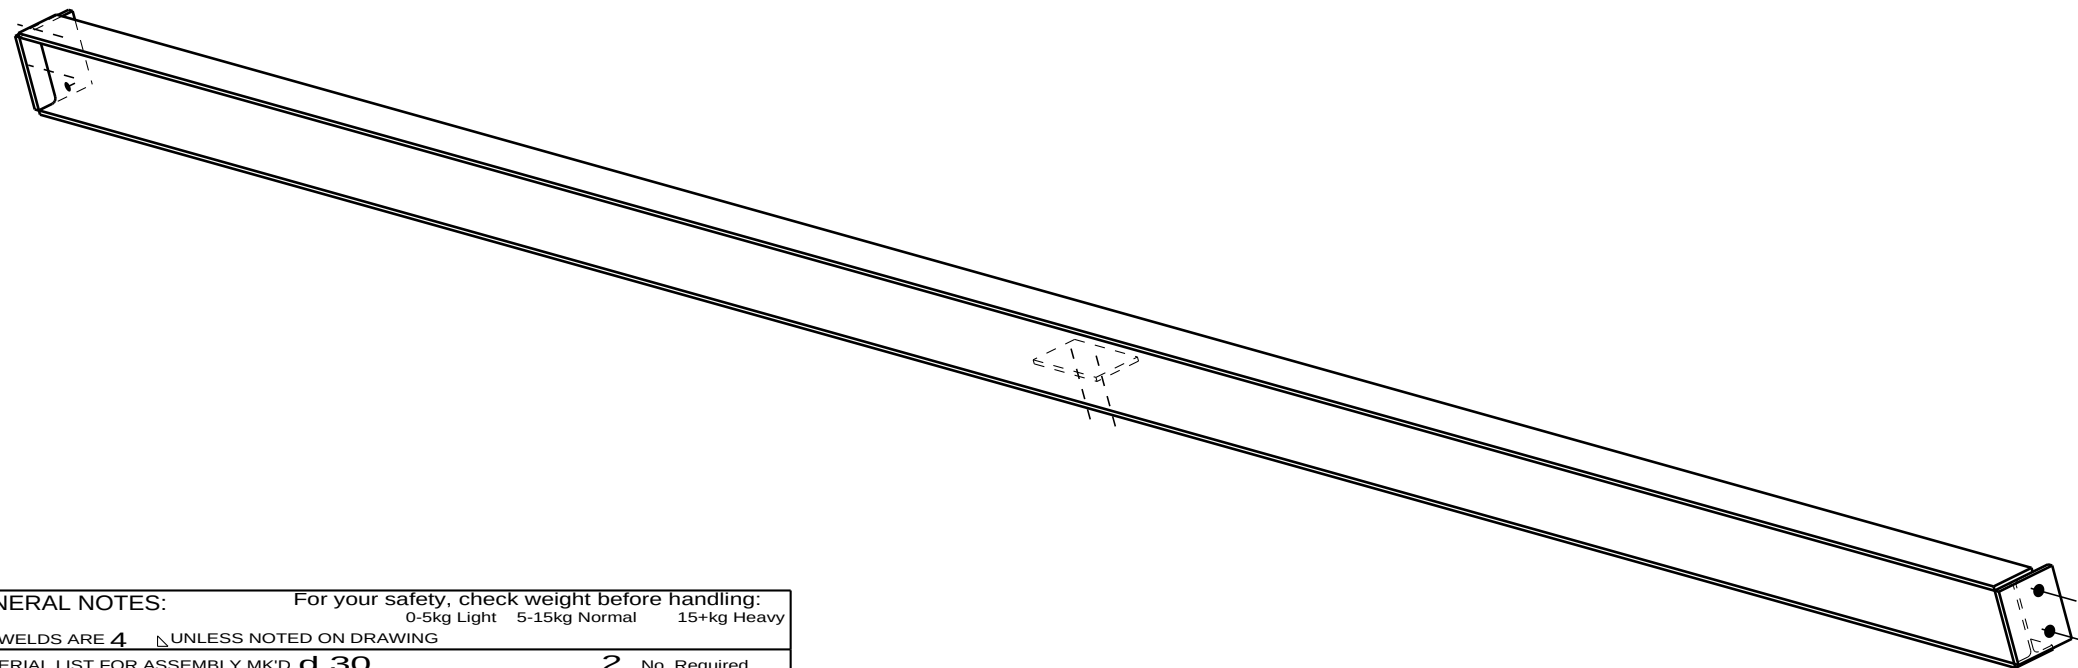
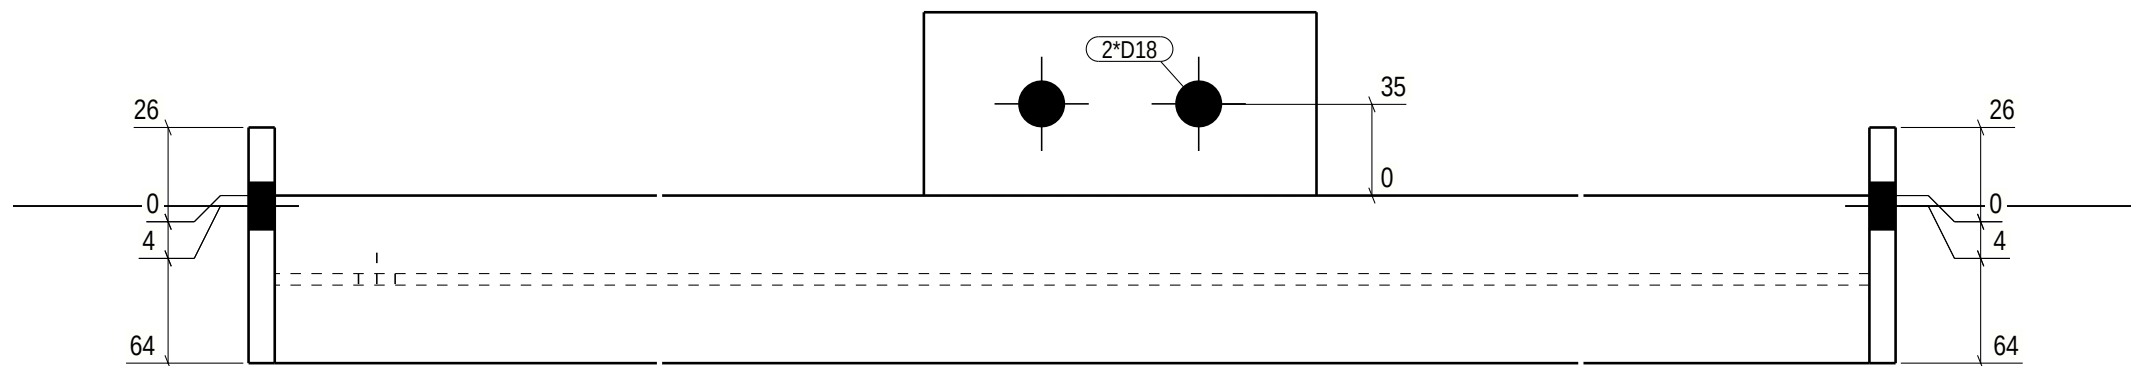


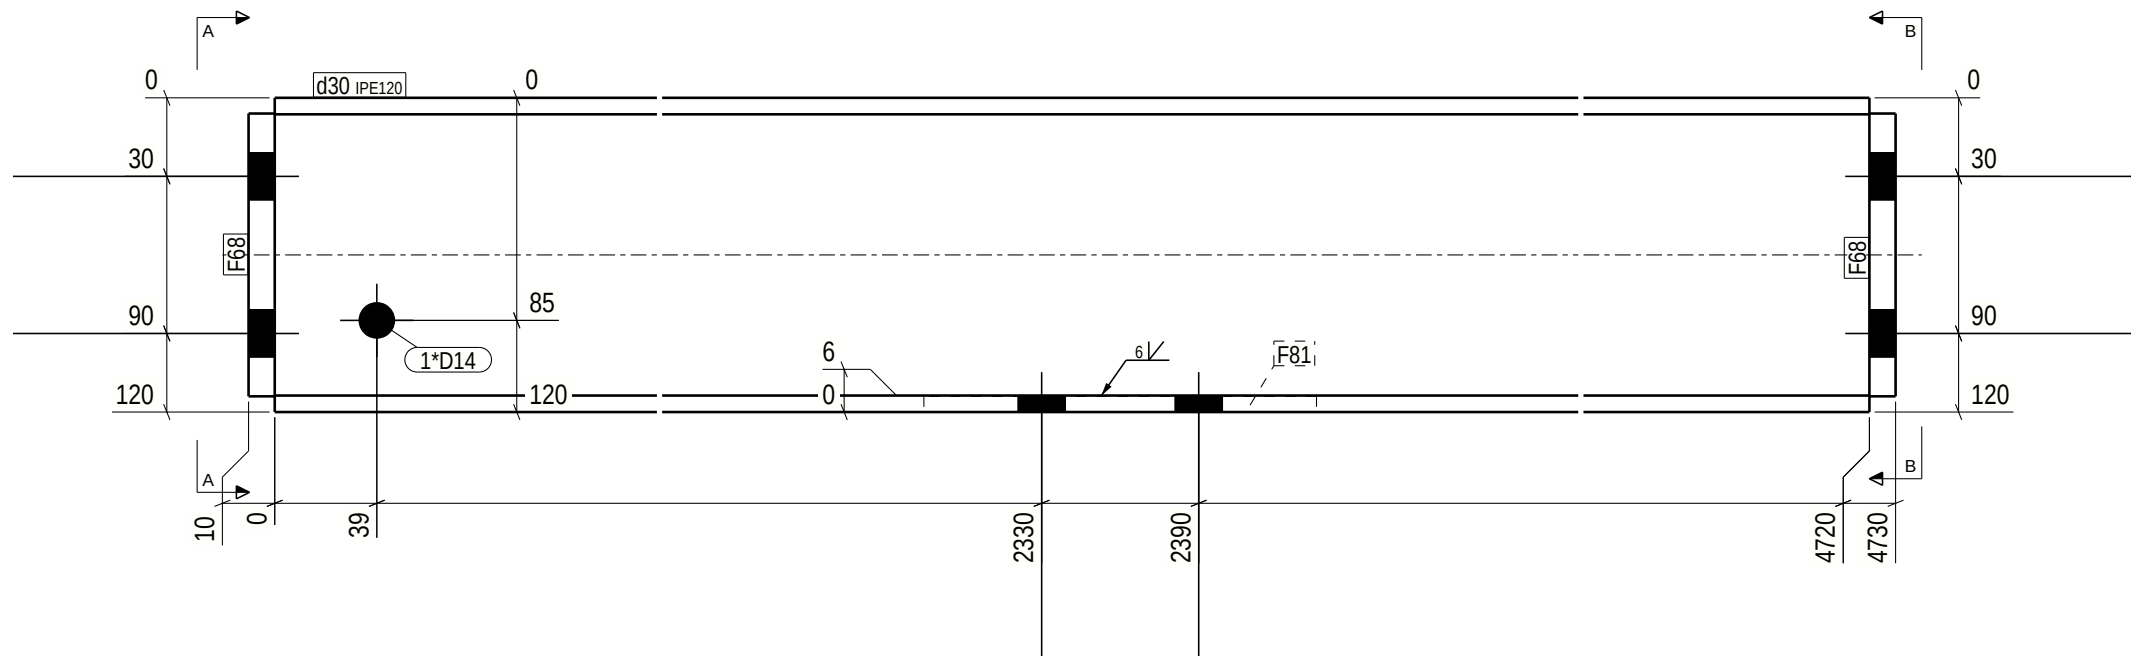

GENERAL NOTES: For your safety, check weight before handling:
0-5kg Light 5-15kg Normal 15+kg Heavy

ALL WELDS ARE 4 UNLESS NOTED ON DRAWING

MATERIAL LIST FOR ASSEMBLY MK'D **d.30** **2** No. Required

Mark	Profile	Material	No.	Length	Area	Weight
d30	IPE120	S355J2	1	4720	2.2	48.9 !!
F68	FL10*90	S355J2	2	108	0.0	0.8
F81	FL6*70	S355J2	1	150	0.0	0.5
Total					2.3	50.9

Finish Class
Standard

Surface treatment info:	Thickness/start point-> length	No.
Galvanised	/	2



Special
surface treatment



weld a = 4

PHASE	QUANTITY
3	2

* o 3 0 4 8 0 - 3 *  DS <i>Stålkonstruktion</i> * A d 3 0 *			
PROJECT	Akkasæter Lager- og vedlikeholdshall		EXEC. CLASS
MEMBER	Drager		PROJECT No
REVISION	ISSUED: 04.11.2025		DRAWING No.
QUANTITY: 2		PROJECT No 30480-3	
DRAFTER: ZLL		DRAWING No. d.30	
BIM control: SST			