

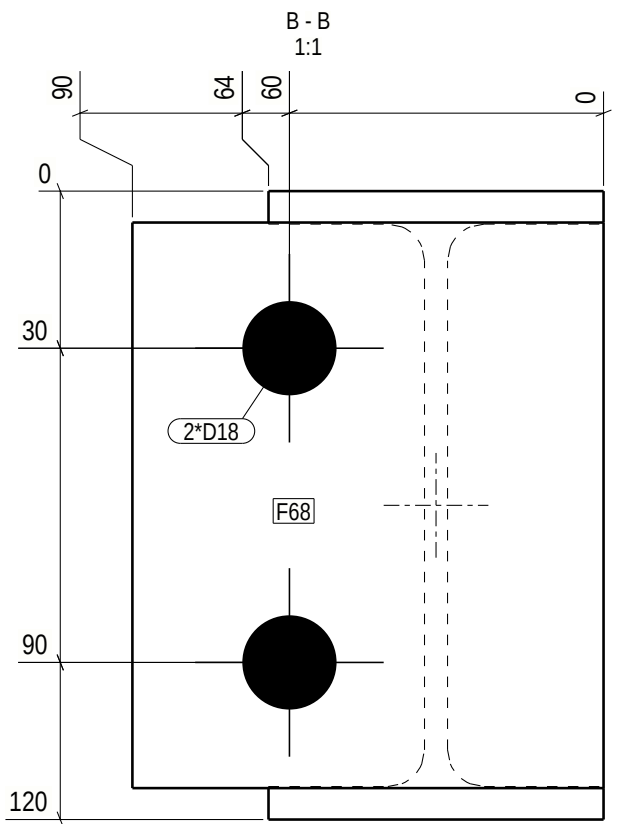
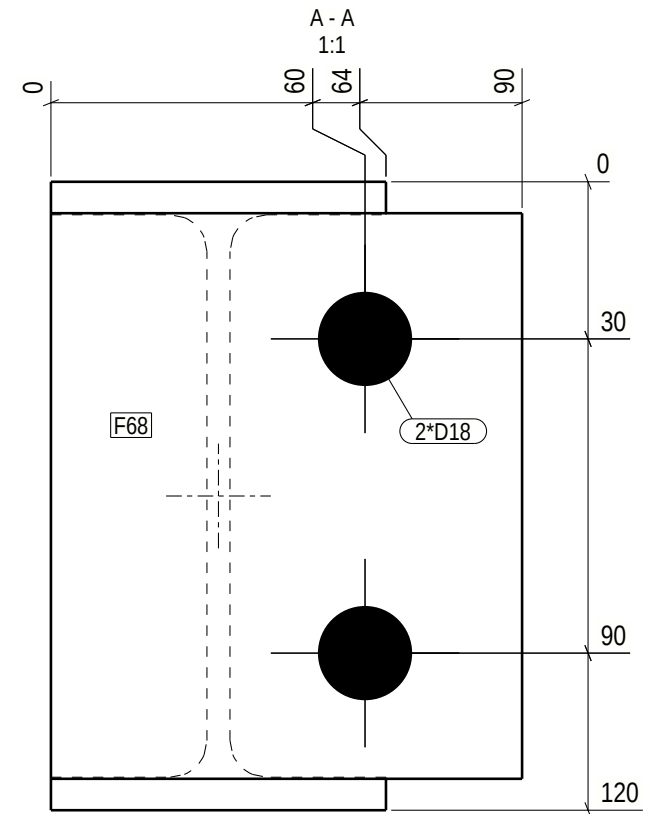
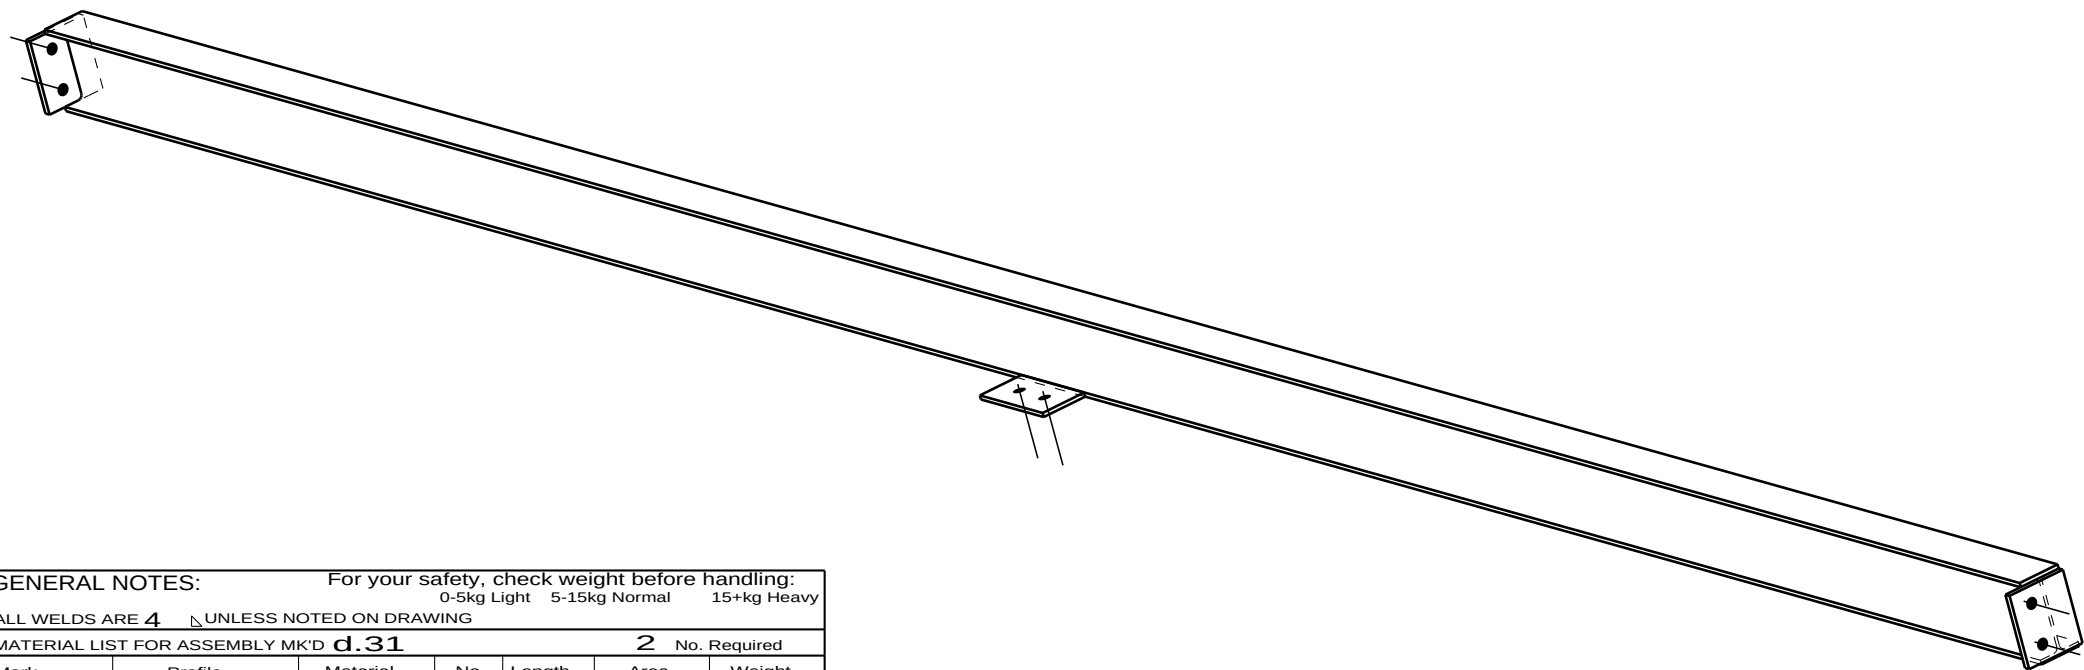


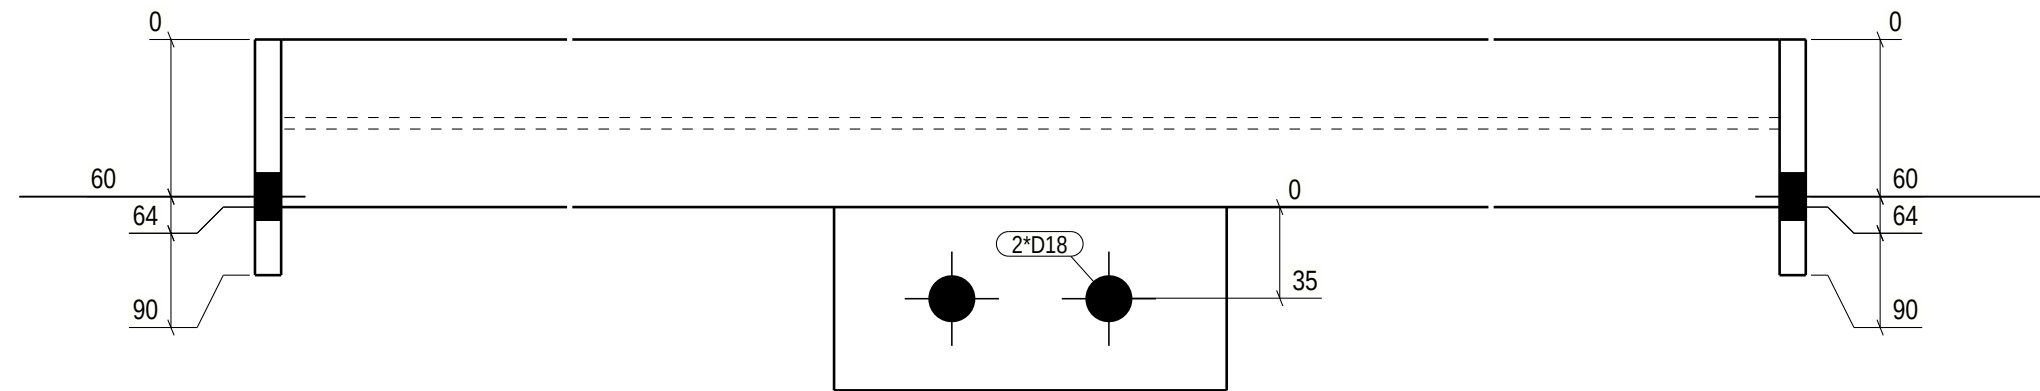

GENERAL NOTES:						
For your safety, check weight before handling:						
0-5kg Light 5-15kg Normal 15+kg Heavy						
ALL WELDS ARE 4 UNLESS NOTED ON DRAWING						
MATERIAL LIST FOR ASSEMBLY MK'D d.31						
2 No. Required						
Mark	Profile	Material	No.	Length	Area	Weight
d31	IPE120	S355J2	1	4720	2.2	48.9 !!
F68	FL10*90	S355J2	2	108	0.0	0.8
F81	FL6*70	S355J2	1	150	0.0	0.5
Total				2.3		50.9

Finish Class
Standard

Surface treatment info:	Thickness/start point-> length	No.
Galvanised	/	2

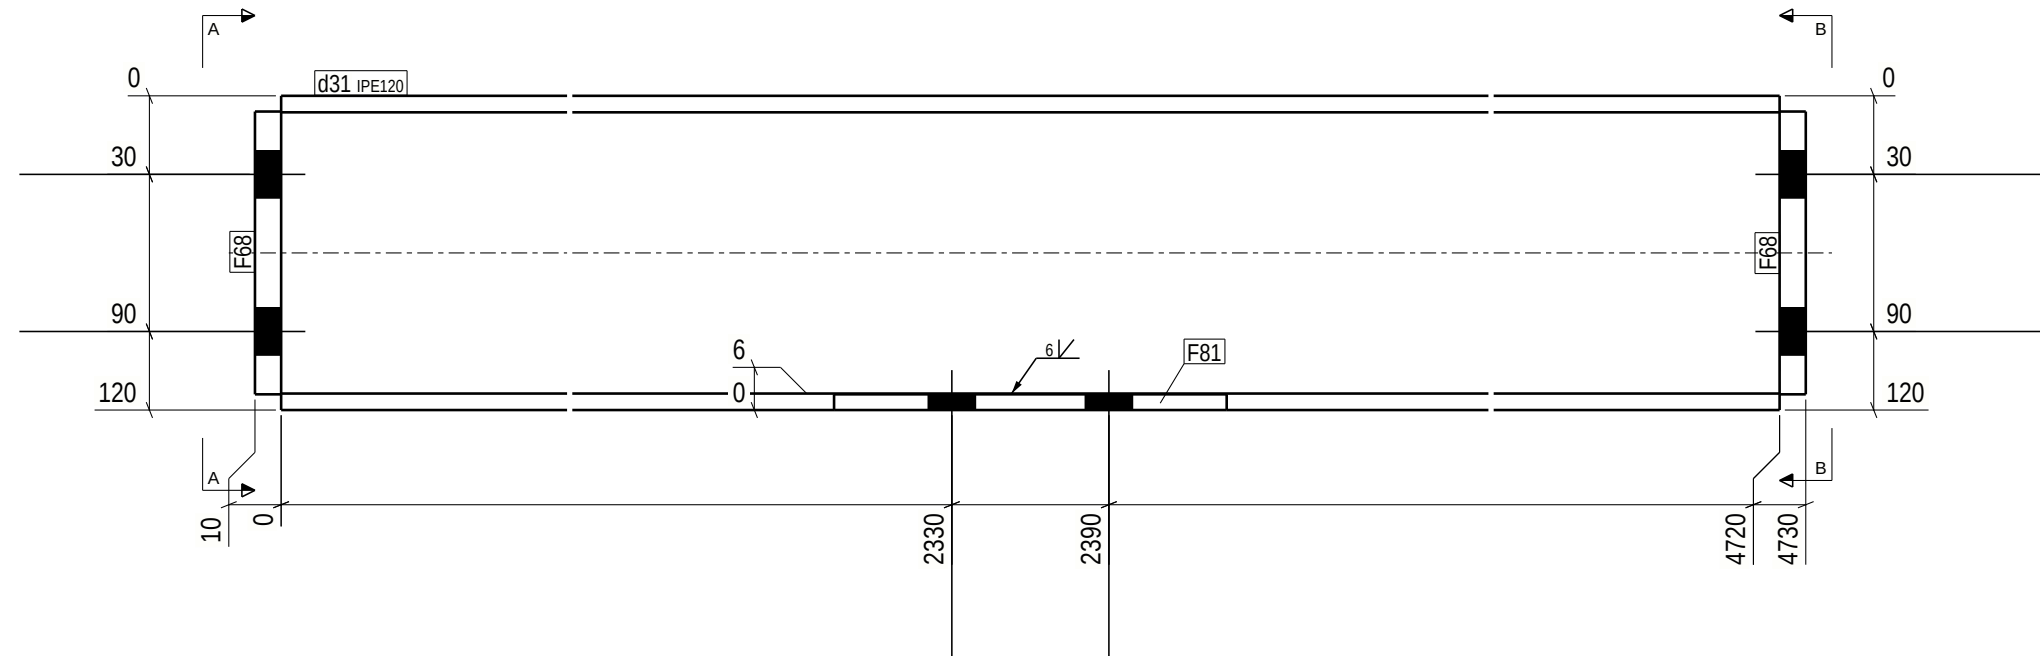

Special
surface treatment



weld a = 4

PHASE	QUANTITY
3	2

* o 3 0 4 8 0 - 3 * DS Skalkonstruktion * A d 3 1 *			
PROJECT	Akkasæter Lager- og vedlikeholdshall	EXEC. CLASS	EXC 2
MEMBER	Drager	QUANTITY:	2
REVISION	ISSUED: 04.11.2025	DRAFTER: ZLL	PROJECT No 30480-3
		BIM control: SST	DRAWING No. d.31