
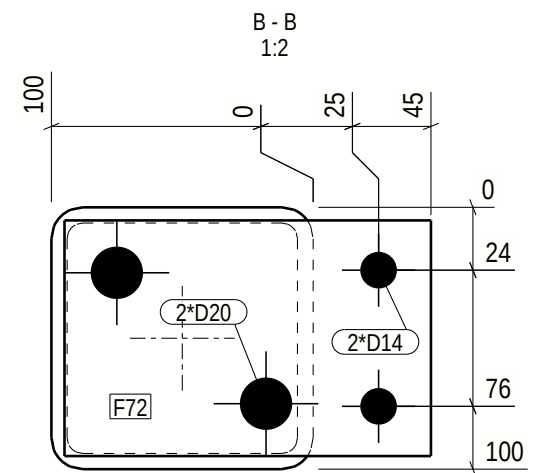
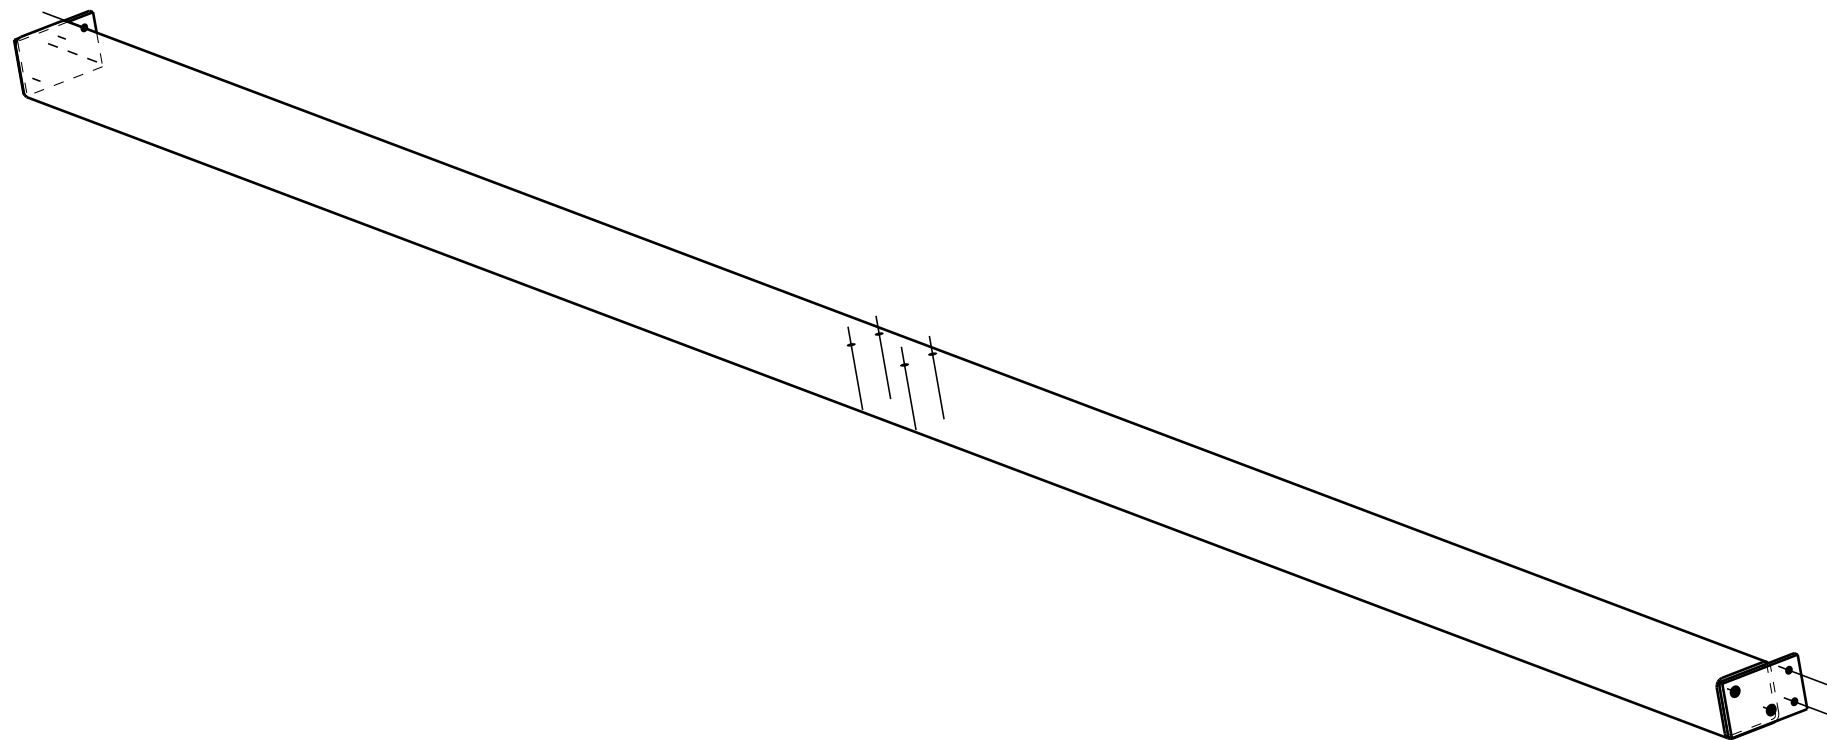
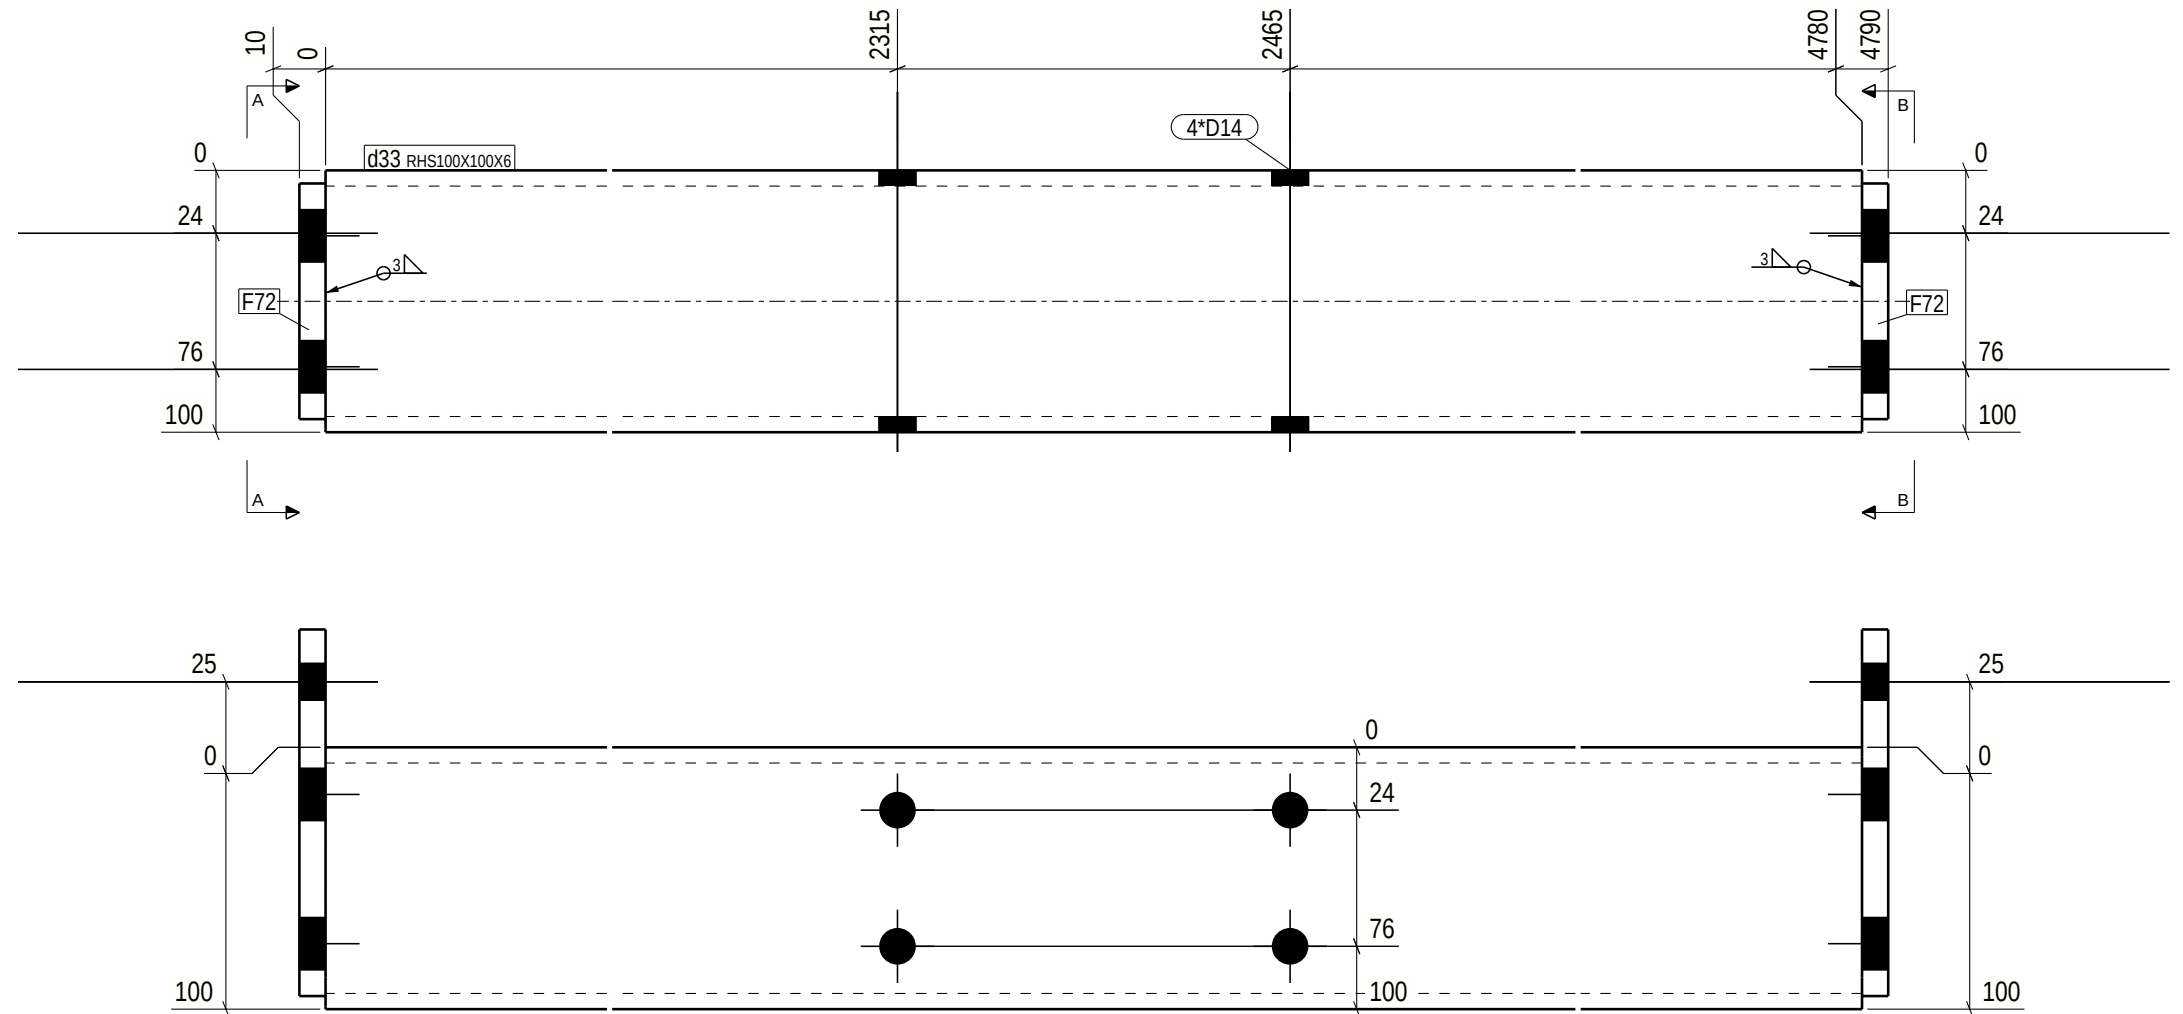


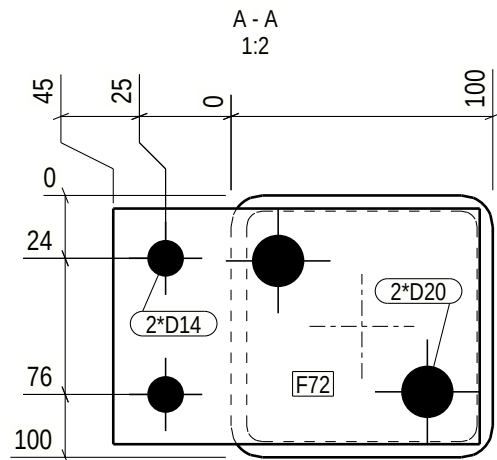

GENERAL NOTES: For your safety, check weight before handling:
0-5kg Light 5-15kg Normal 15+kg Heavy

ALL WELDS ARE 4 UNLESS NOTED ON DRAWING

MATERIAL LIST FOR ASSEMBLY MK'D **d.33**

Mark	Profile	Material	No.	Length	Area	Weight
d33	RHS100X100X6	S355J2H	1	4780	1.8	80.8 !!
F72	FL10*90	S355J2	2	140	0.0	1.0
Total					1.9	82.8

Finish Class
Standard

Surface treatment info:	Thickness/start point-> length	No.
Galvanised	/	2



Special
surface treatment



weld a = 4

PHASE	QUANTITY
3	2

* o 3 0 4 8 0 - 3 *  DS <i>Stålkonstruktion</i> * A d 3 3 *			
PROJECT	Akkasæter Lager- og vedlikeholdshall	EXEC. CLASS	EXC 2
MEMBER	Drager	QUANTITY:	2
REVISION		ISSUED:	04.11.2025
		DRAFTER:	ZLL
		BIM control:	SST
PROJECT No		30480-3	
DRAWING No.		d.33	