
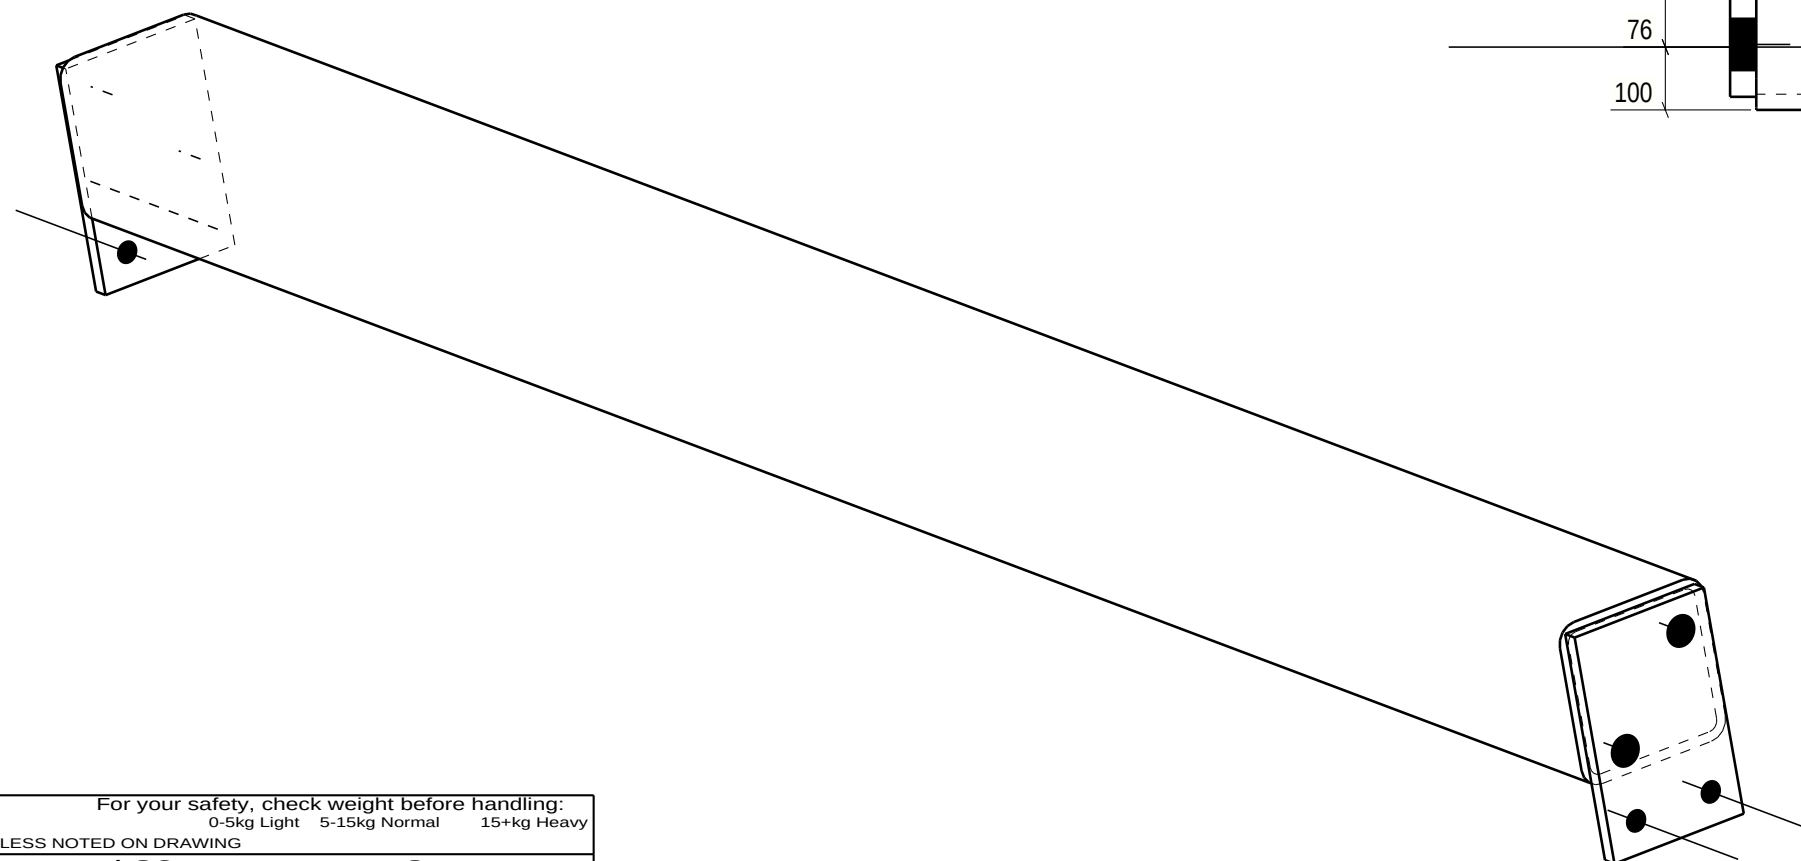


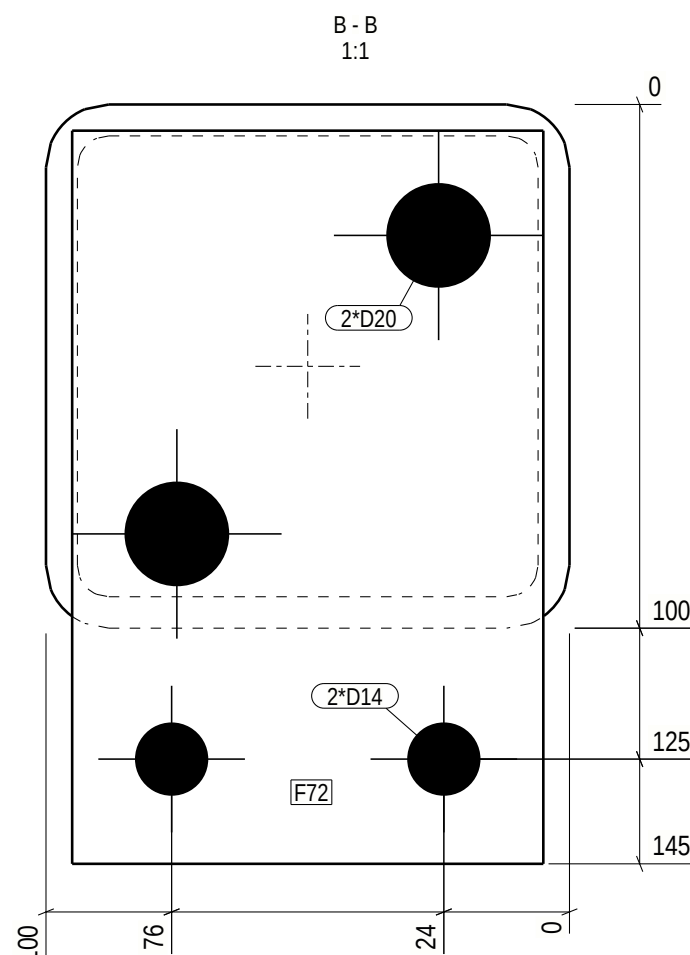

* o 3 0 4 8 0 - 3 *					 DS Steelkonstruktion		* A d 3 6 *	
PROJECT	Akkasæter Lager- og vedlikeholdshall				EXEC. CLASS		EXC 2	
MEMBER	Drager		QUANTITY:	2	PROJECT No	30480-3		
REVISION	ISSUED: 04.11.2025		DRAFTER: BIM control:	ZLL SSS	DRAWING No.	d.36		