
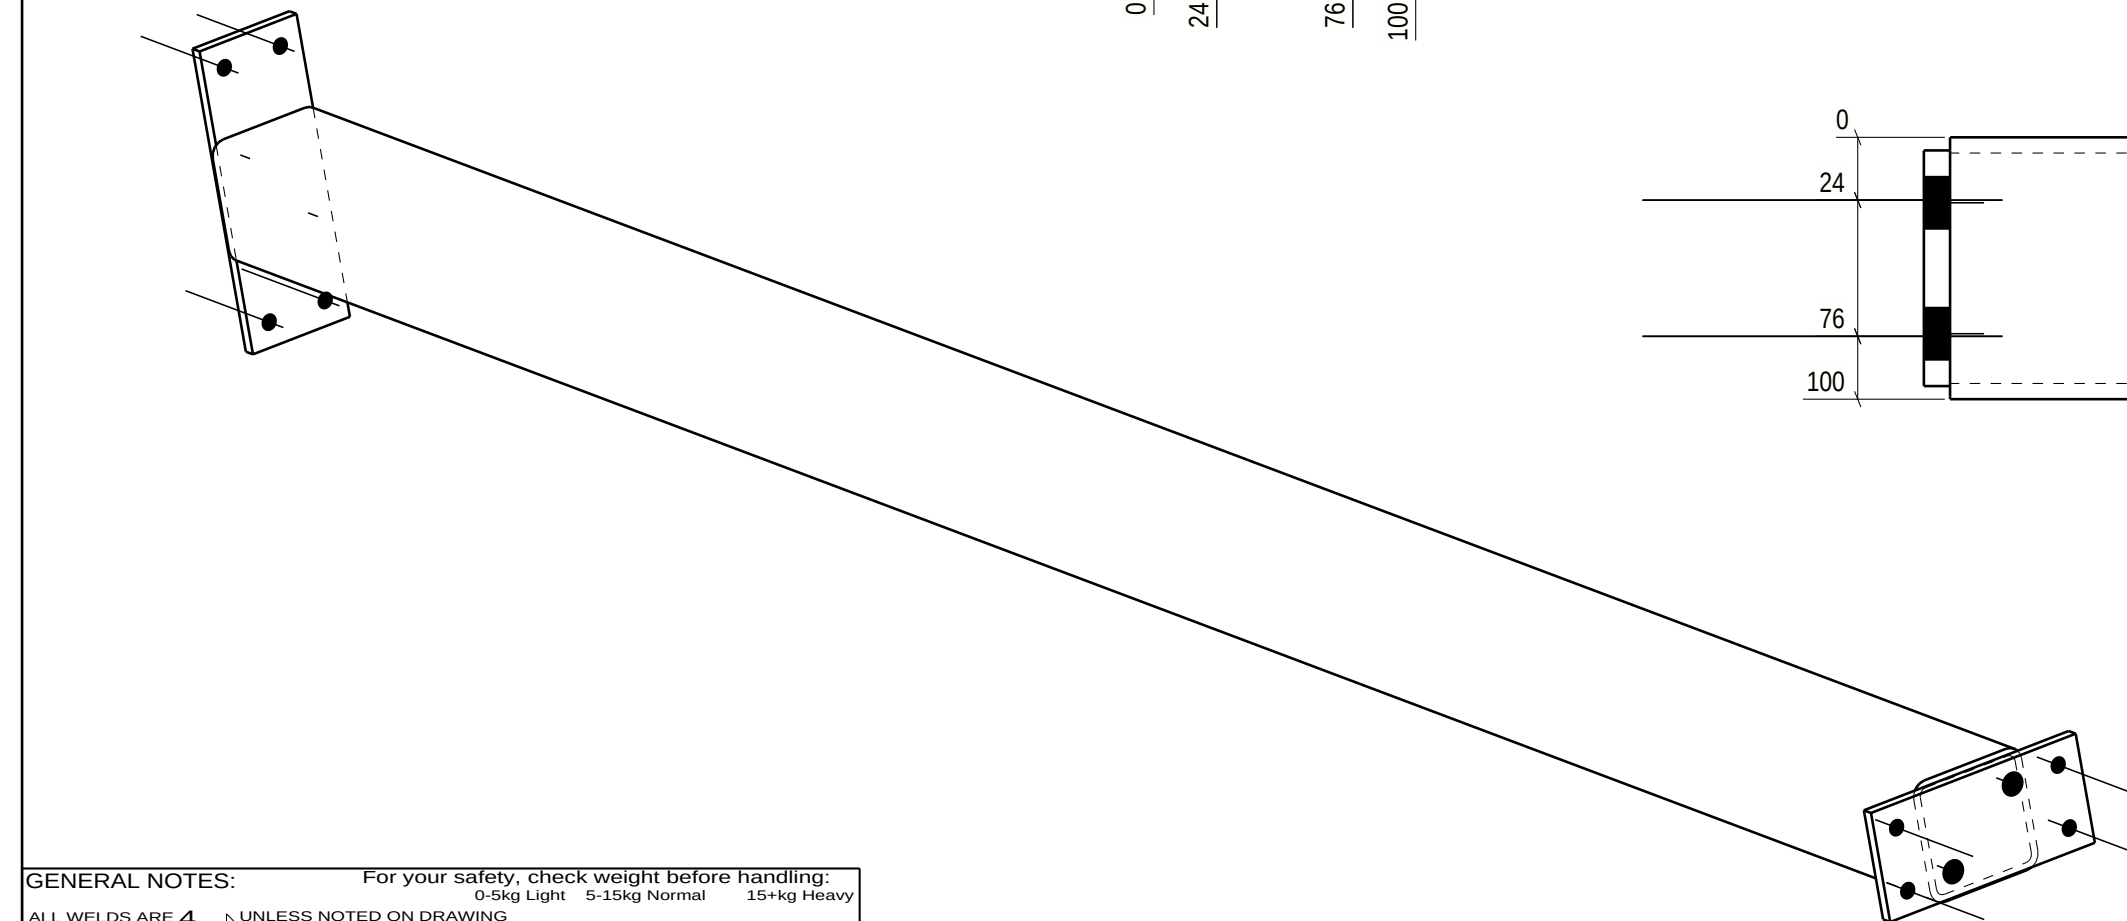
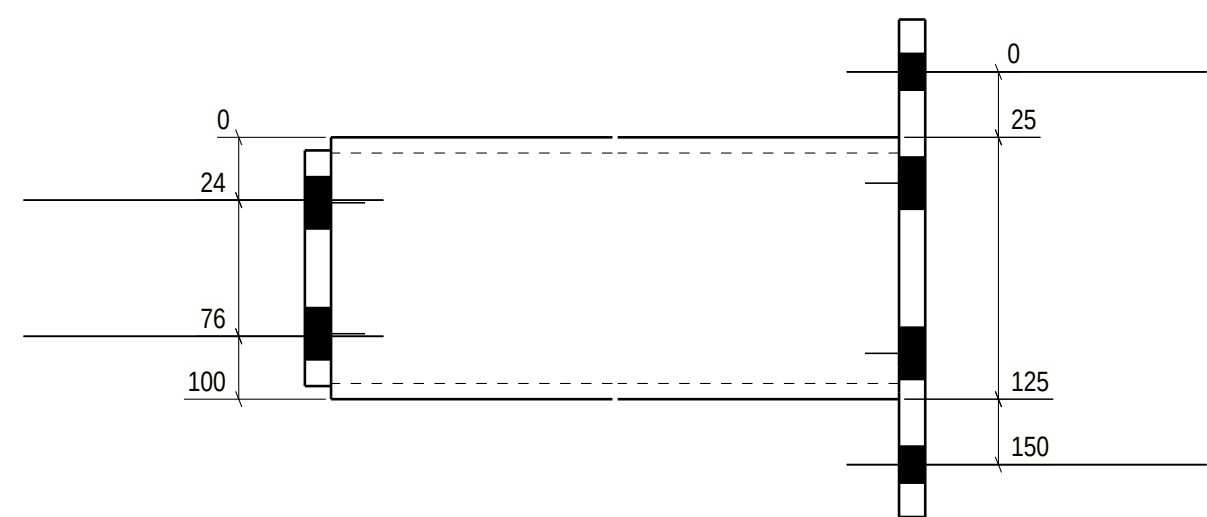
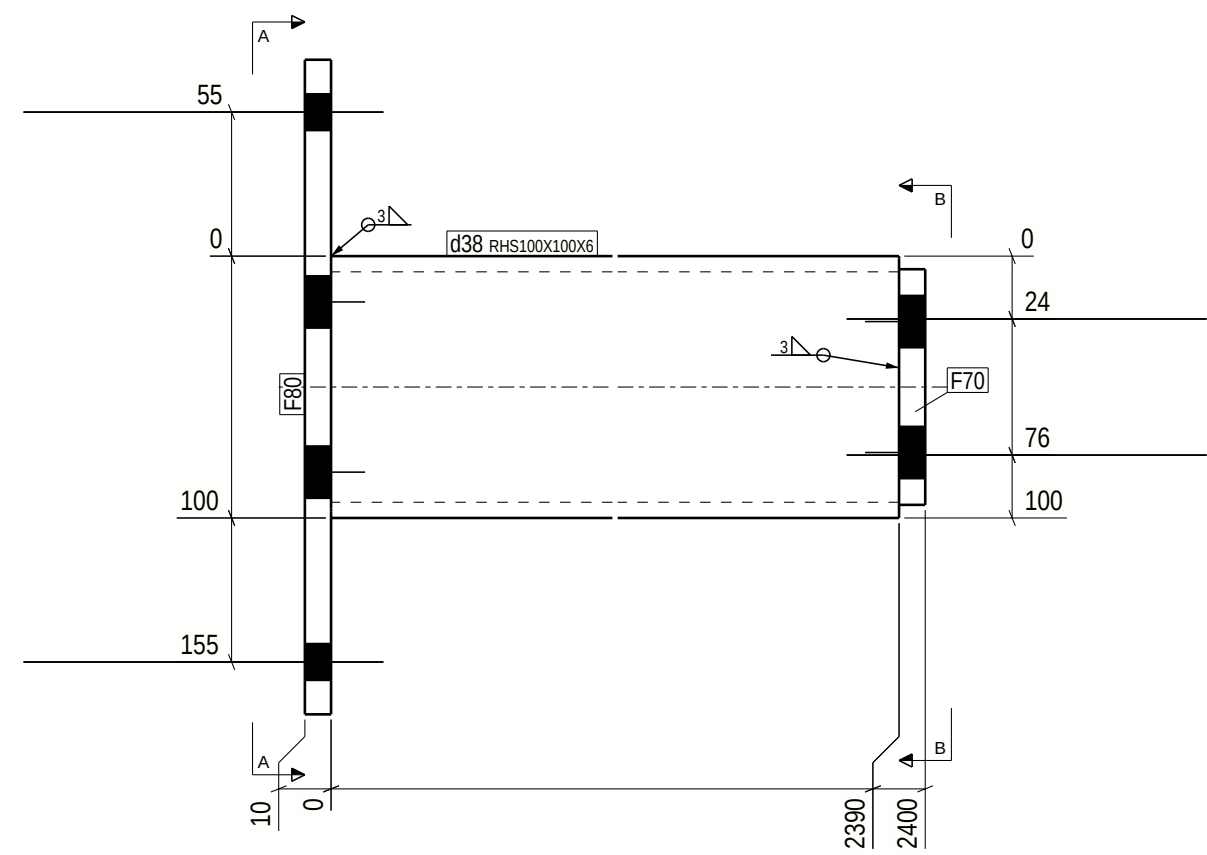
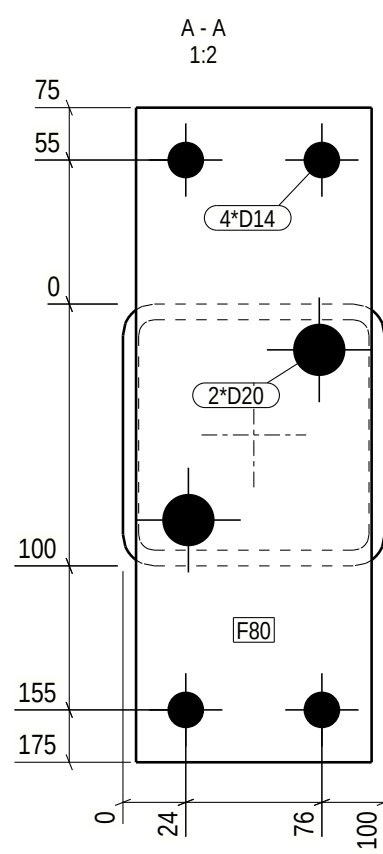


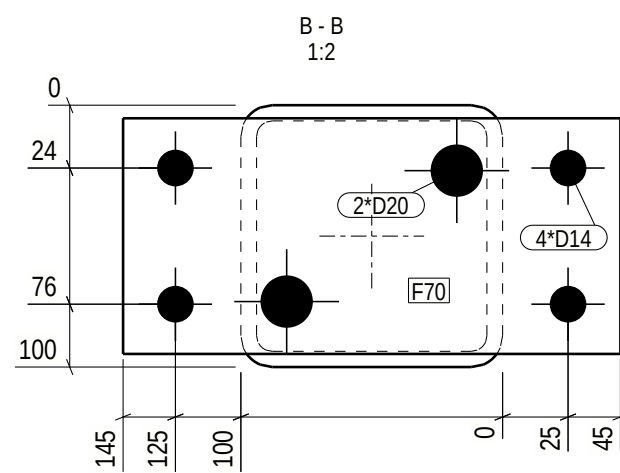

GENERAL NOTES: For your safety, check weight before handling:
0-5kg Light 5-15kg Normal 15+kg Heavy

ALL WELDS ARE 4 UNLESS NOTED ON DRAWING

MATERIAL LIST FOR ASSEMBLY MK'D d.38

Mark	Profile	Material	No.	Length	Area	Weight
d38	RHS100X100X6	S355J2H	1	2390	0.9	40.4 !!
F70	FL10*90	S355J2	1	190	0.0	1.3
F80	FL10*90	S355J2	1	250	0.1	1.8
Total					1.0	43.5

**Finish Class
Standard**

Surface treatment info:	Thickness/start point-> length	No.
Galvanised	/	4

Special surface treatment weld a = 4

PHASE	QUANTITY
3	4

* o 3 0 4 8 0 - 3 * DS <i>Stålkonstruktion</i> * A d 3 8 *			
PROJECT	Akkasæter Lager- og vedlikeholdshall	EXEC. CLASS	EXC 2
MEMBER	Drager	QUANTITY:	4
REVISION	ISSUED: 04.11.2025	DRAFTER: ZLL SST	BIM control:
PROJECT No		30480-3	
DRAWING No.		d.38	