
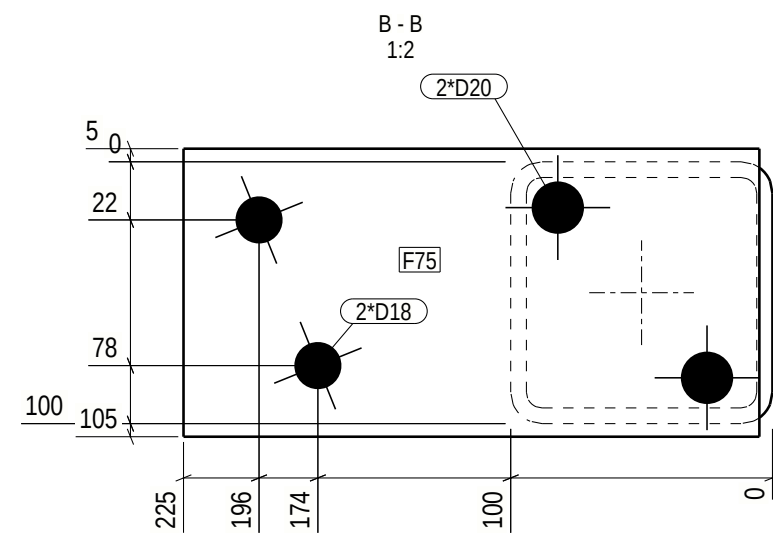
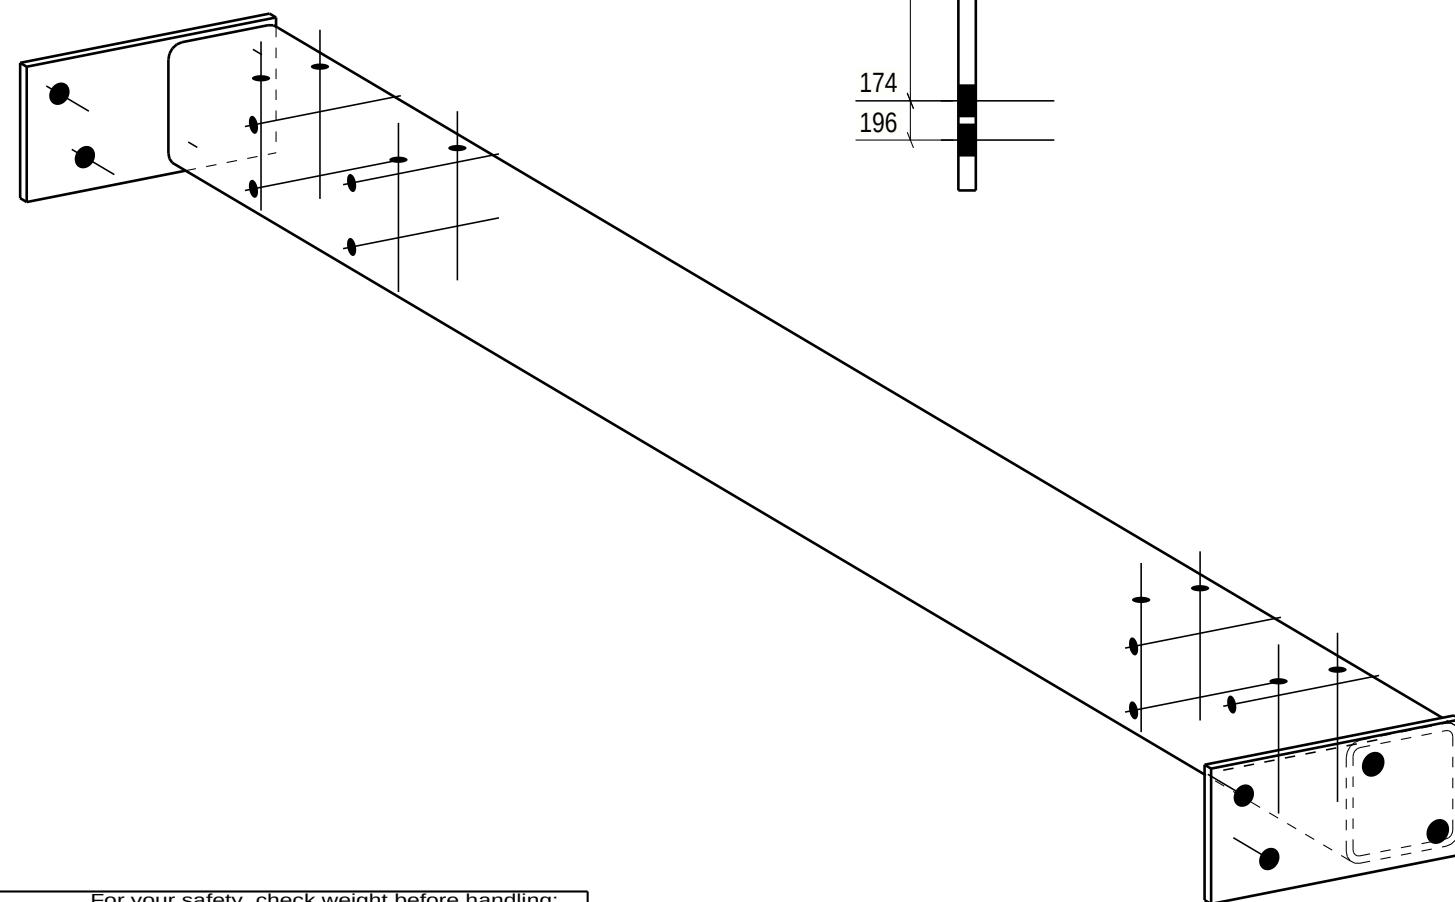
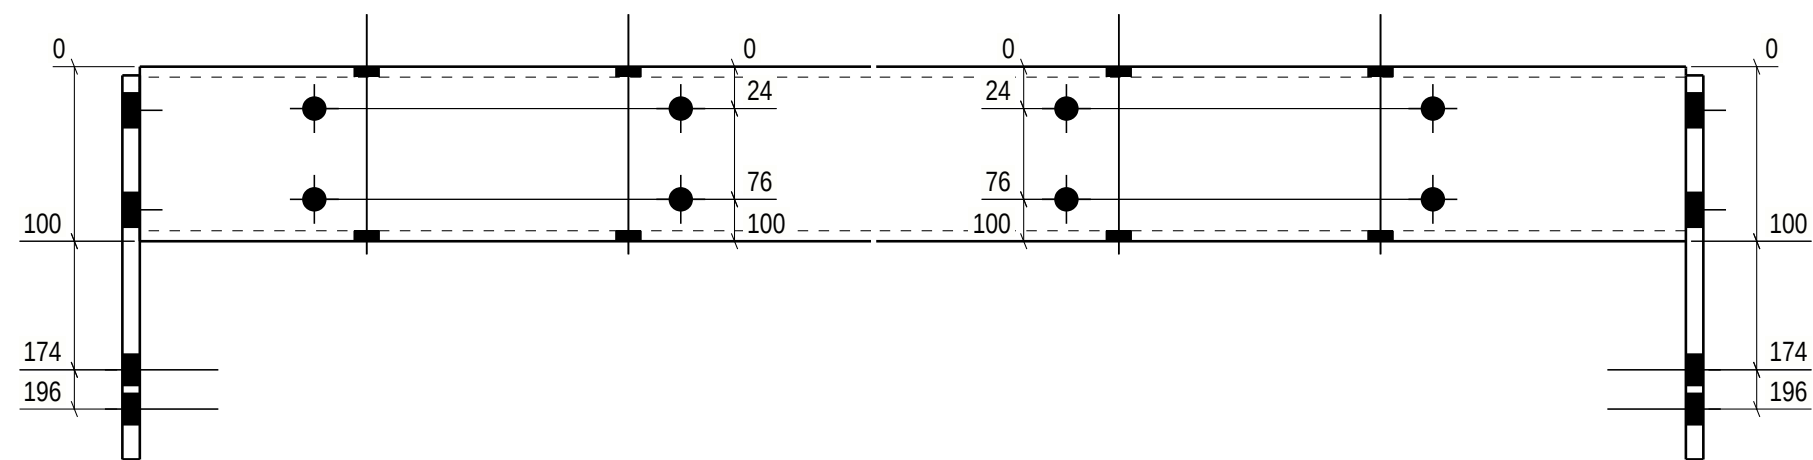
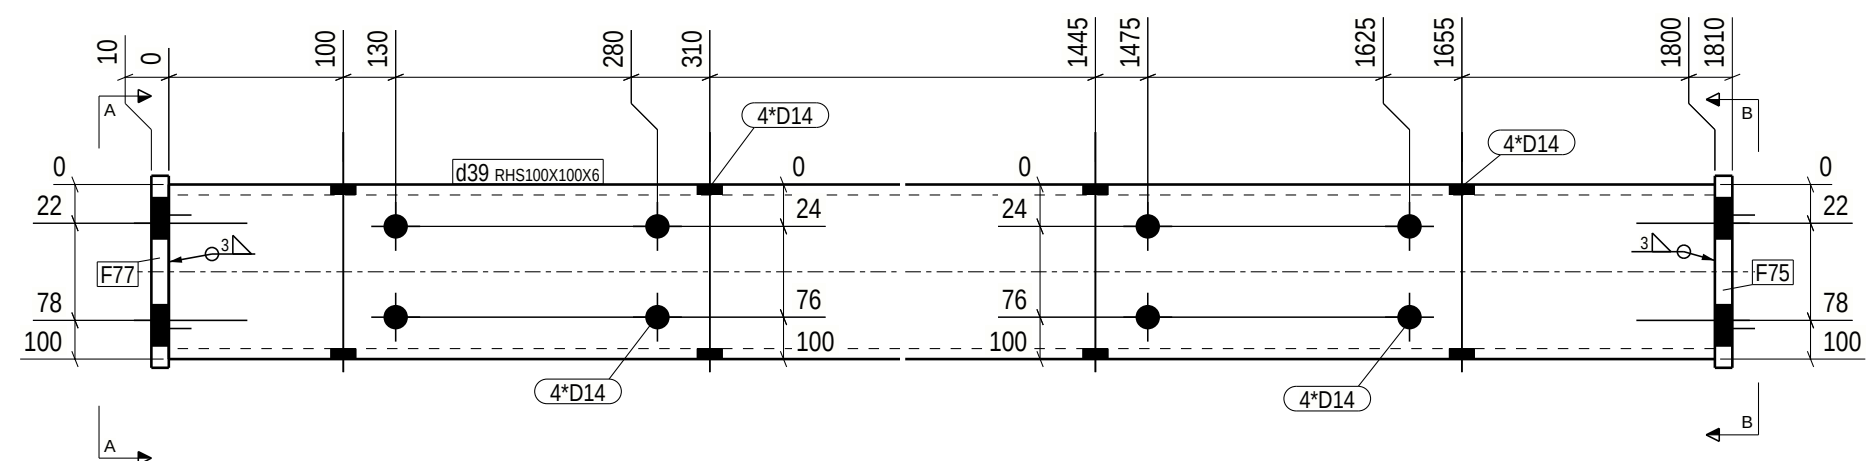


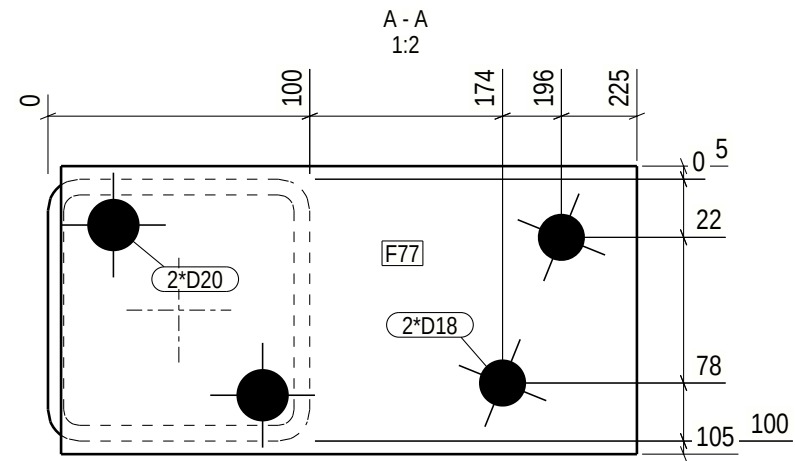

GENERAL NOTES:

For your safety, check weight before handling:

0-5kg Light

5-15kg Normal

15+kg Heavy

ALL WELDS ARE 4 UNLESS NOTED ON DRAWING

MATERIAL LIST FOR ASSEMBLY MK'D d.39

2 No. Required

Mark	Profile	Material	No.	Length	Area	Weight
d39	RHS100X100X6	S355J2H	1	1800	0.7	30.4 !!
F75	FL10*110	S355J2	1	220	0.1	1.9
F77	FL10*110	S355J2	1	220	0.1	1.9
Total					0.8	34.2

Finish Class
Standard

Surface treatment info:	Thickness/start point--> length	No.
Galvanised	/	2



Special
surface treatment



weld a = 4

PHASE	QUANTITY
3	2

* o 3 0 4 8 0 - 3 *  DS <i>Stålkonstruktion</i> * A d 3 9 *			
PROJECT	Akkasæter Lager- og vedlikeholdshall	EXEC. CLASS	EXC 2
MEMBER	Drager	QUANTITY:	2
REVISION		ISSUED:	05.11.2025
		DRAFTER:	ZLL
		BIM control:	SST
PROJECT No		30480-3	
DRAWING No.		d.39	