


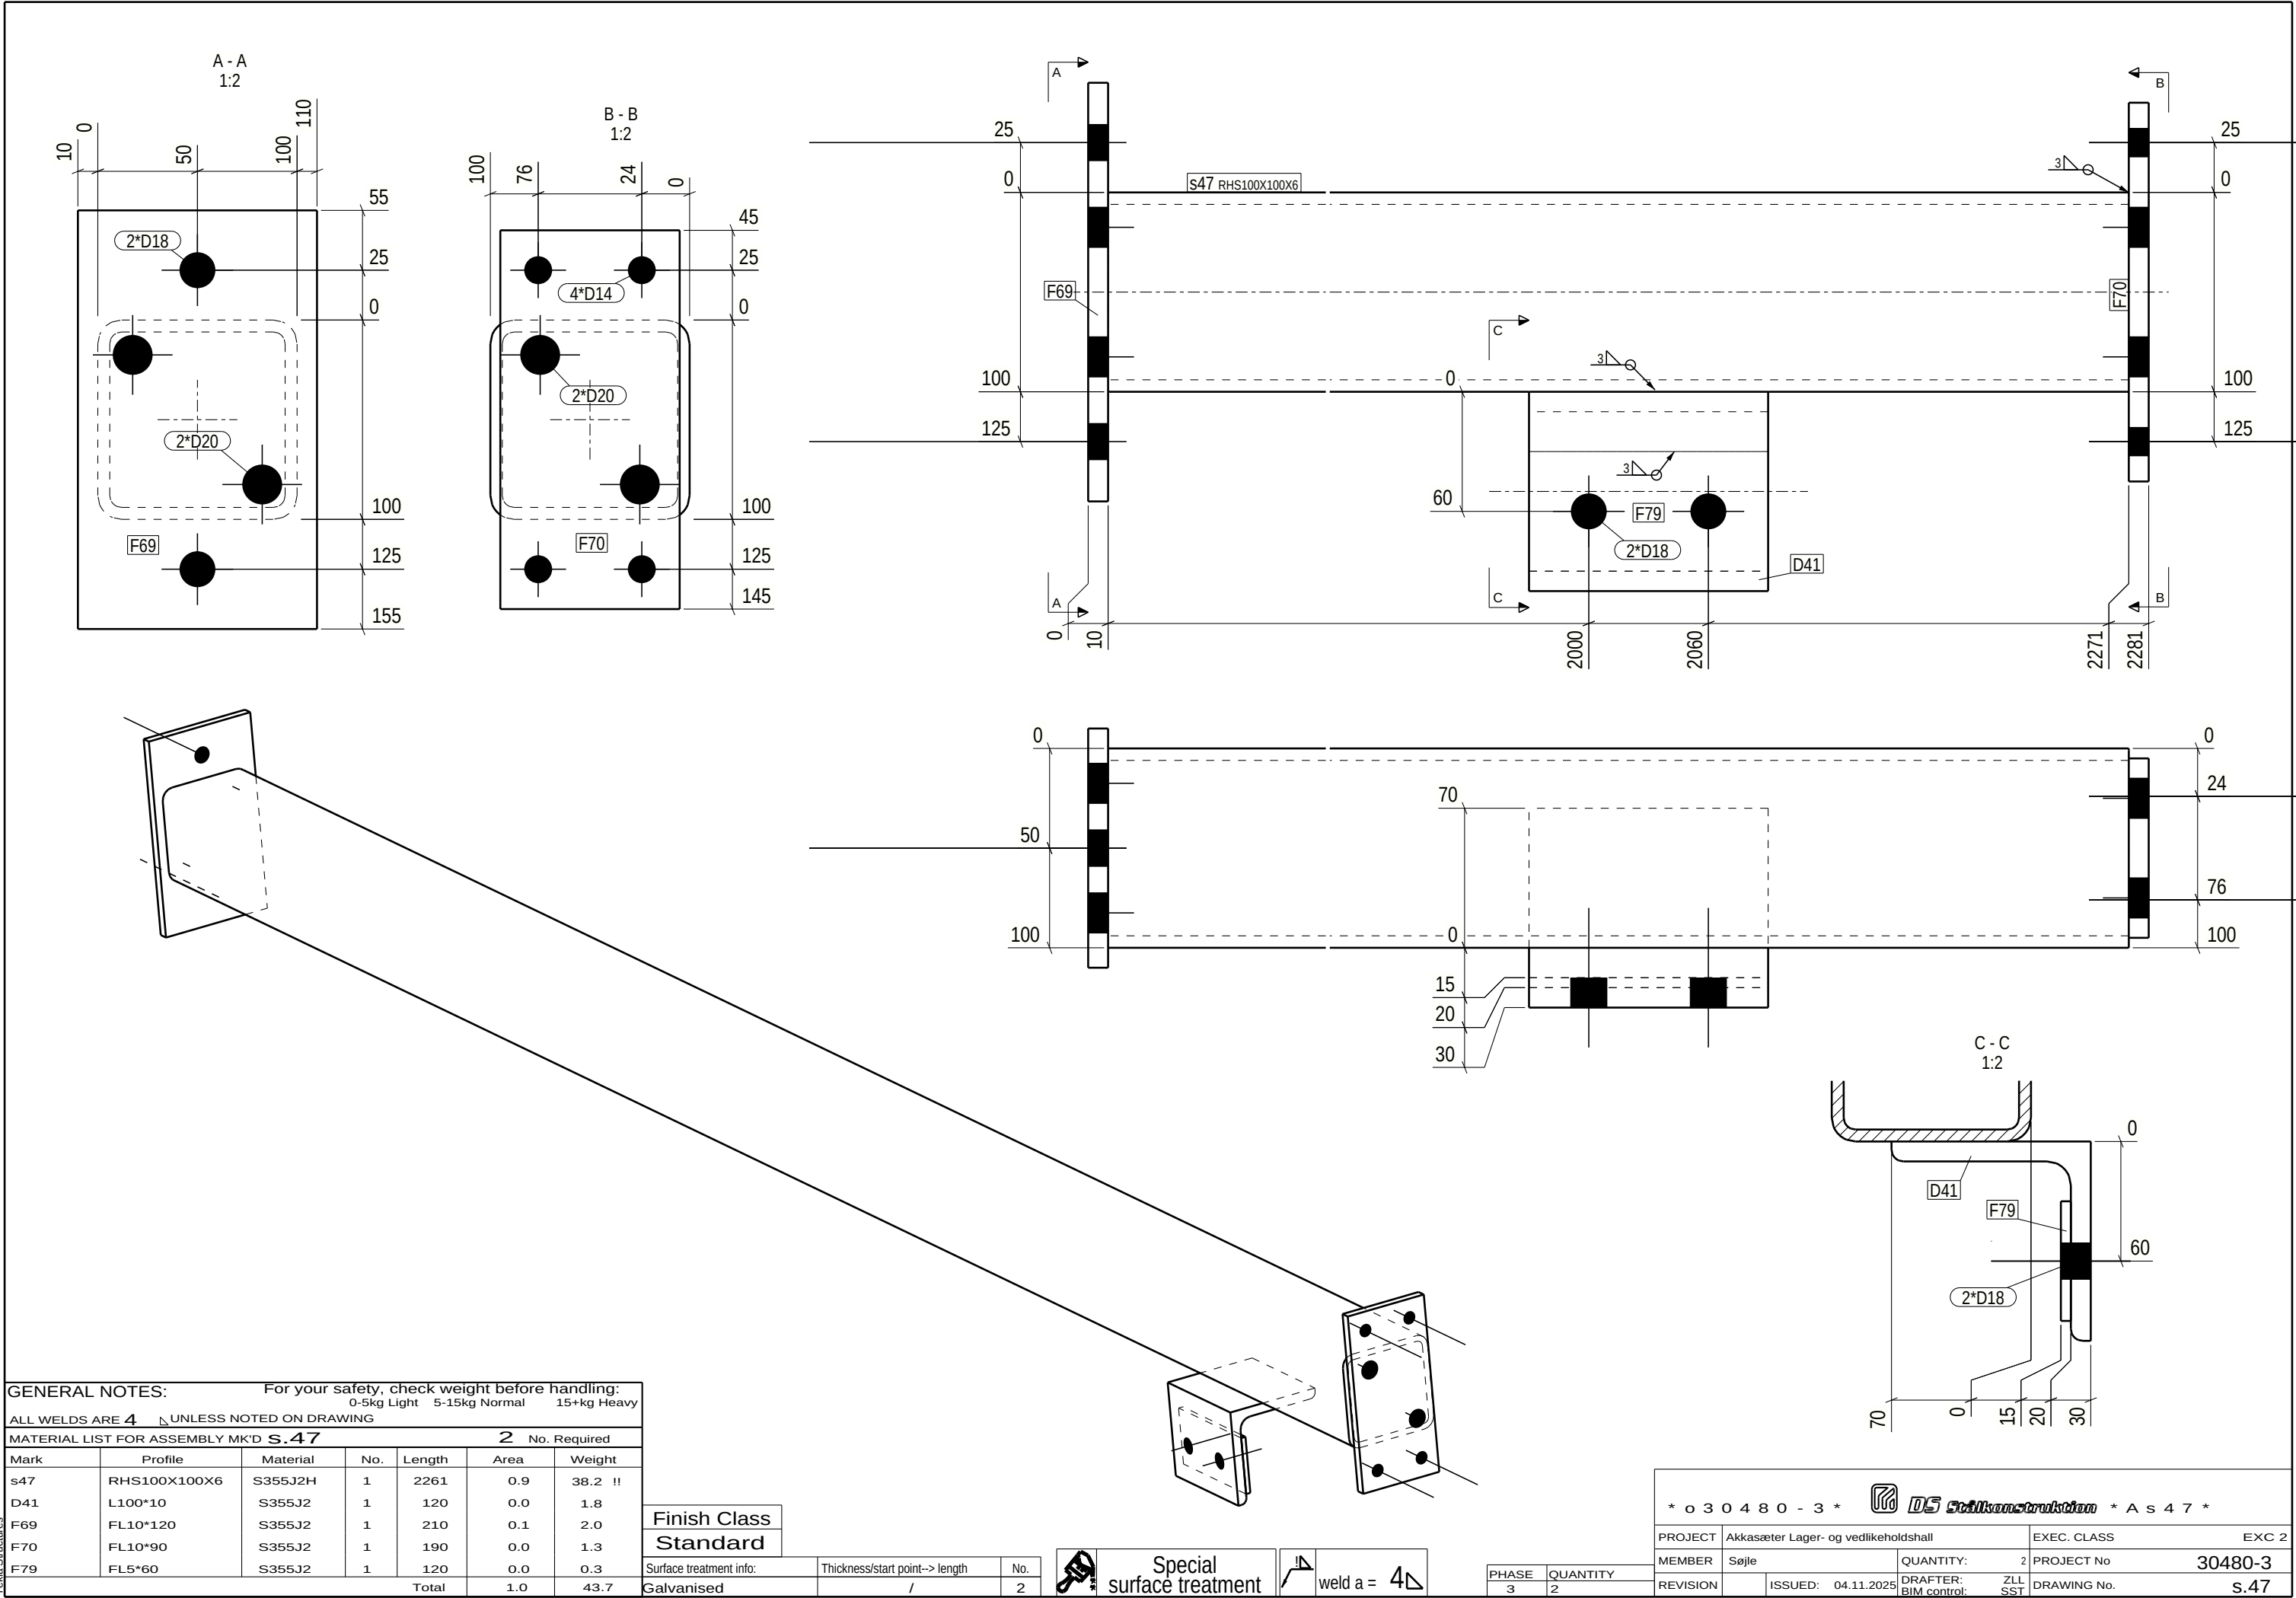

GENERAL NOTES: For your safety, check weight before handling:
0-5kg Light 5-15kg Normal 15+kg Heavy

ALL WELDS ARE 4 UNLESS NOTED ON DRAWING

MATERIAL LIST FOR ASSEMBLY MK'D S.47						2	No. Required
Mark	Profile	Material	No.	Length	Area	Weight	
s47	RHS100X100X6	S355J2H	1	2261	0.9	38.2 !!	
D41	L100*10	S355J2	1	120	0.0	1.8	
F69	FL10*120	S355J2	1	210	0.1	2.0	
F70	FL10*90	S355J2	1	190	0.0	1.3	
F79	FL5*60	S355J2	1	120	0.0	0.3	
Total				1.0	43.7		

Finish Class
Standard

Surface treatment info:	Thickness/start point-> length	No.
Galvanised	/	2

Special
surface treatment

weld a = 4

PHASE	QUANTITY
3	2

* o 3 0 4 8 0 - 3 * DS Steelkonstruktion * As 4 7 *			
PROJECT	Akkasæter Lager- og vedlikeholdshall	EXEC. CLASS	EXC 2
MEMBER	Søyle	QUANTITY:	2
REVISION	ISSUED: 04.11.2025	DRAFTER:	ZLL
		BIM control:	SST
PROJECT No		30480-3	
DRAWING No.		s.47	