
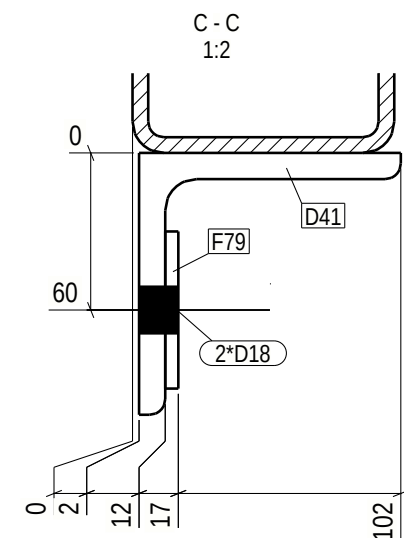
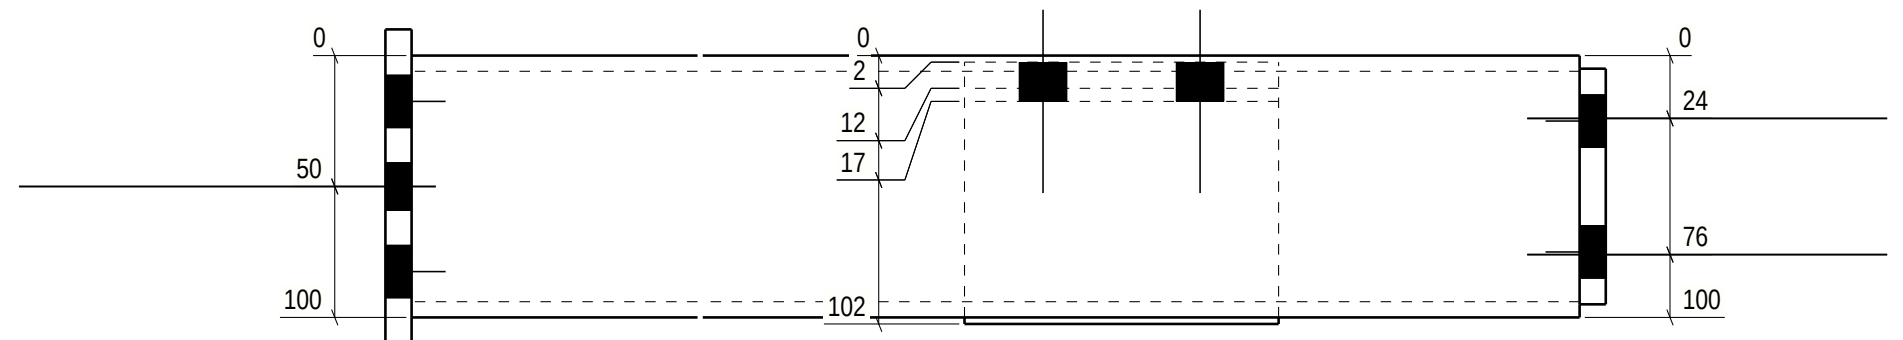


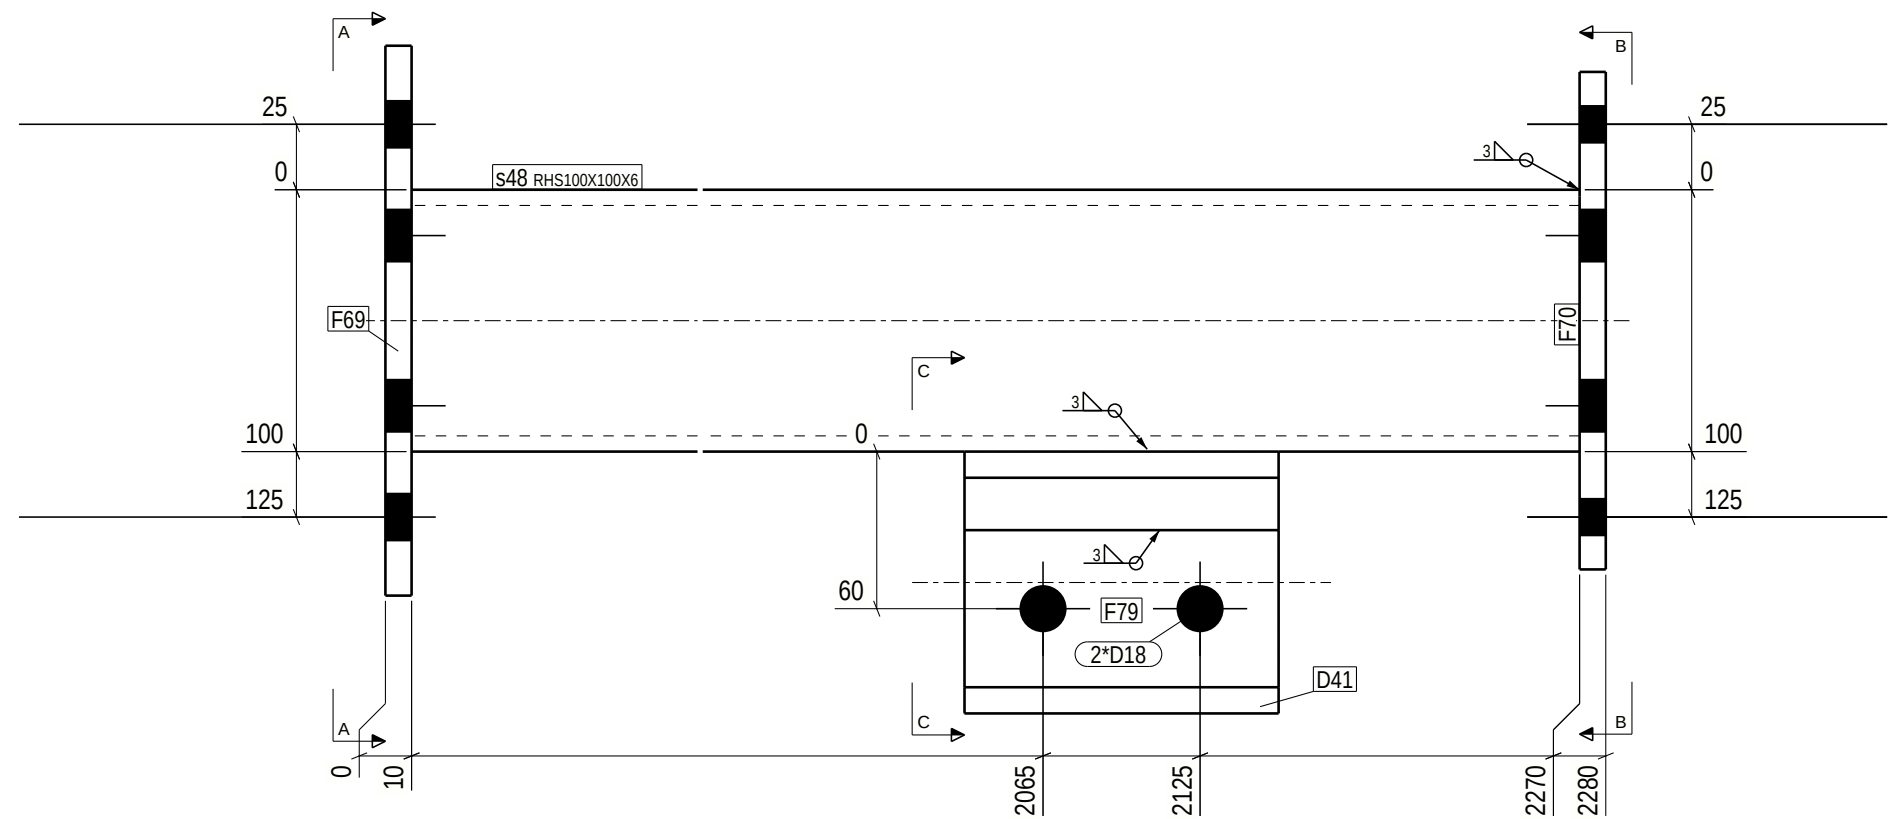

MATERIAL LIST FOR ASSEMBLY MK'D s.48						1 No. Required
Mark	Profile	Material	No.	Length	Area	Weight
s48	RHS100X100X6	S355J2H	1	2260	0.9	38.2 !!
D41	L100*10	S355J2	1	120	0.0	1.8
F69	FL10*120	S355J2	1	210	0.1	2.0
F70	FL10*90	S355J2	1	190	0.0	1.3
F79	FL5*60	S355J2	1	120	0.0	0.3
Total					1.0	43.6

Surface treatment info:	Thickness/start point--> length	No.
Galvanised	/	1

	weld a = 4
---	--

PHASE	QUANTITY
3	1

* 030480 - 3 *				 DS <i>Skalkonstruktion</i>		* A s 4 8 *			
PROJECT		Akksæter Lager- og vedlikeholdshall				EXEC. CLASS		EXC 2	
MEMBER		Sølle		QUANTITY:		1		PROJECT No. 30480-3	
REVISION		ISSUED: 04.11.2025		DRAFTER: BIM		ZLL		DRAWING No. s.48	