
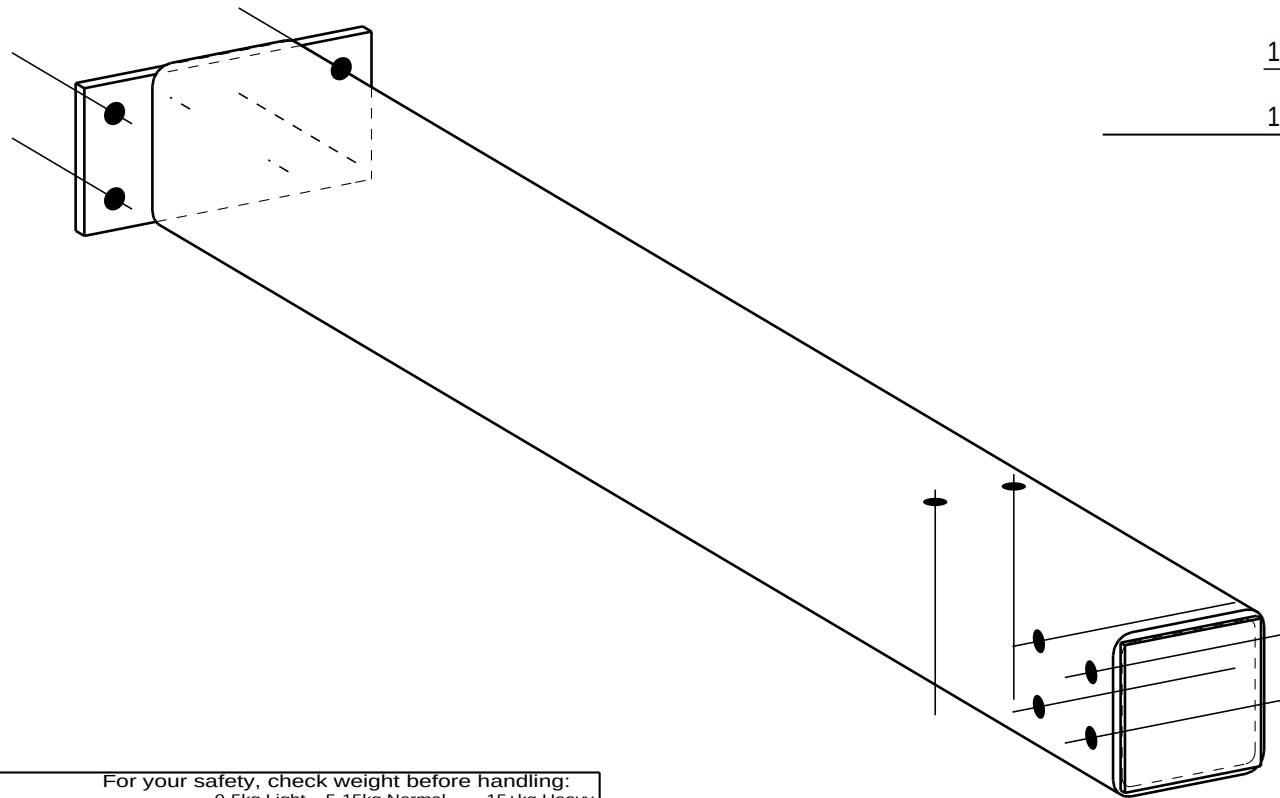
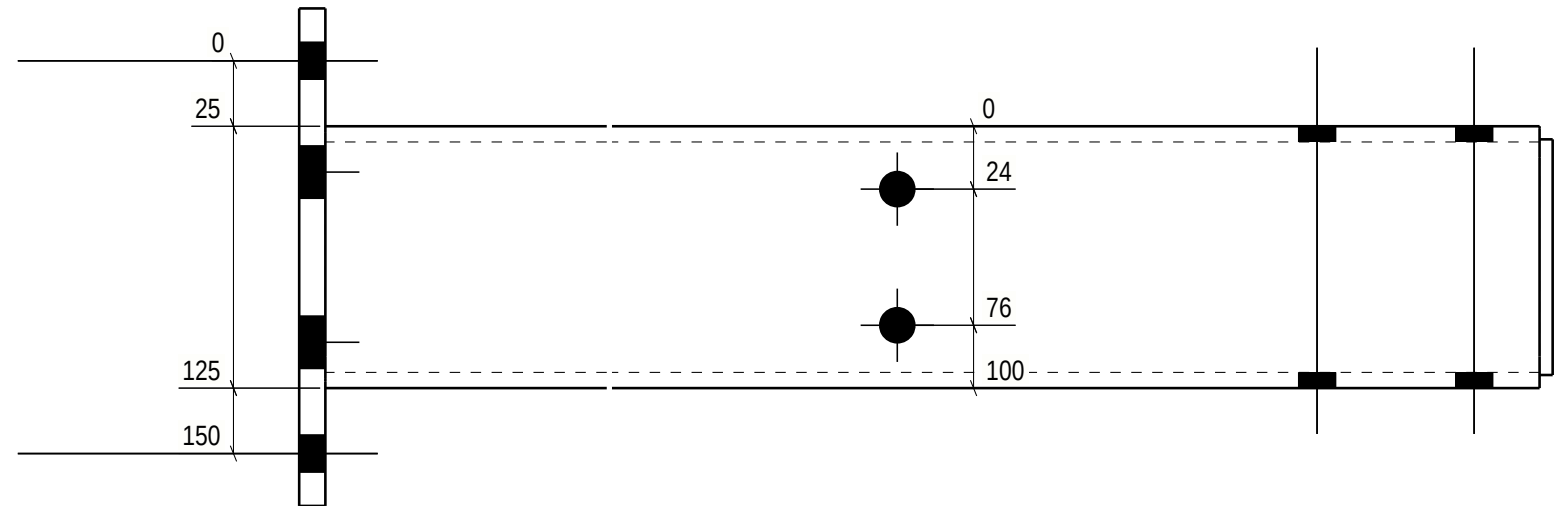
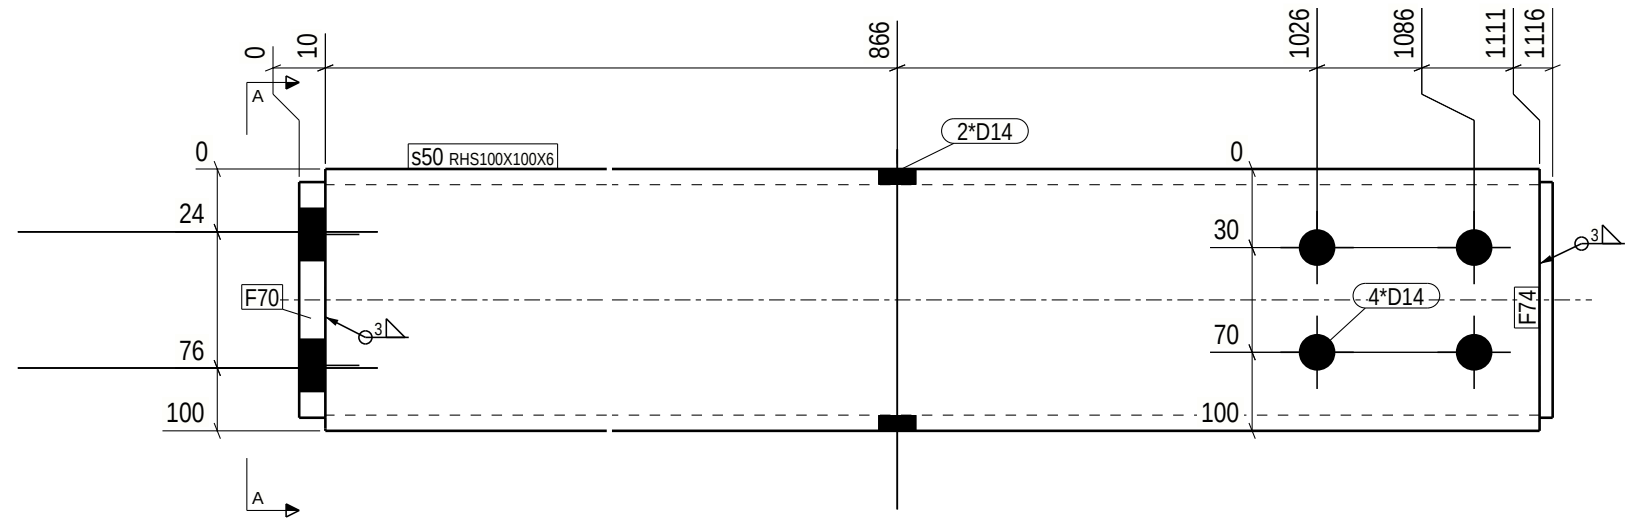


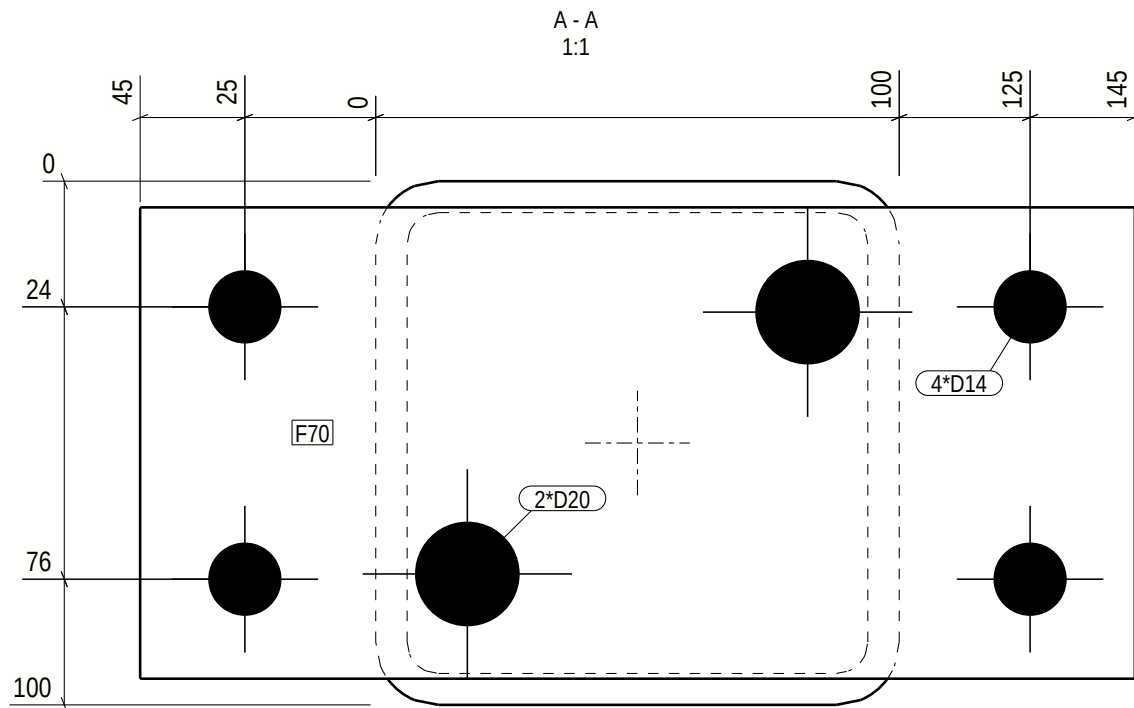

GENERAL NOTES: For your safety, check weight before handling:
0-5kg Light 5-15kg Normal 15+kg Heavy

ALL WELDS ARE 4 UNLESS NOTED ON DRAWING

MATERIAL LIST FOR ASSEMBLY MK'D **s.50** 4 No. Required

Mark	Profile	Material	No.	Length	Area	Weight
S50	RHS100X100X6	S355J2H	1	1101	0.4	18.6 !!
F70	FL10*90	S355J2	1	190	0.0	1.3
F74	FL5*90	S355J2	1	90	0.0	0.3
Total					0.5	20.3

Finish Class
Standard

Surface treatment info:	Thickness/start point-> length	No.
Galvanised	/	4



Special
surface treatment



weld a = 4

PHASE	QUANTITY
3	4

* o 3 0 4 8 0 - 3 *  DS <i>Stalkonstruktion</i> * A s 5 0 *			
PROJECT	Akkasæter Lager- og vedlikeholdshall	EXEC. CLASS	EXC 2
MEMBER	Søyle	QUANTITY:	4
REVISION		ISSUED:	04.11.2025
		DRAFTER:	ZLL
		BIM control:	SST
PROJECT No		30480-3	
DRAWING No.		s.50	