
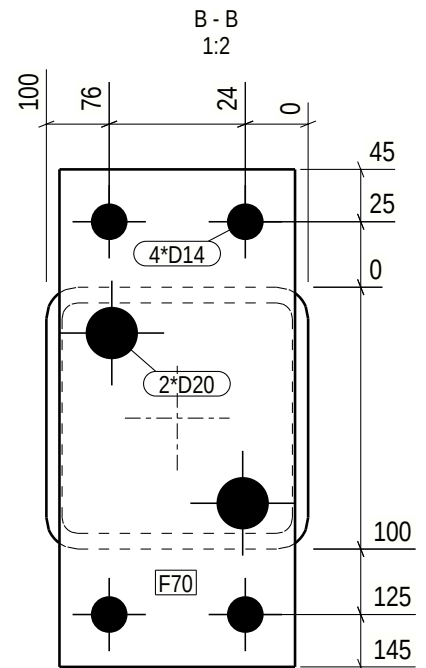
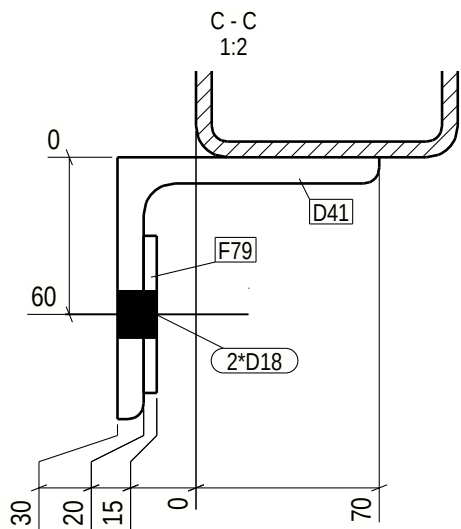
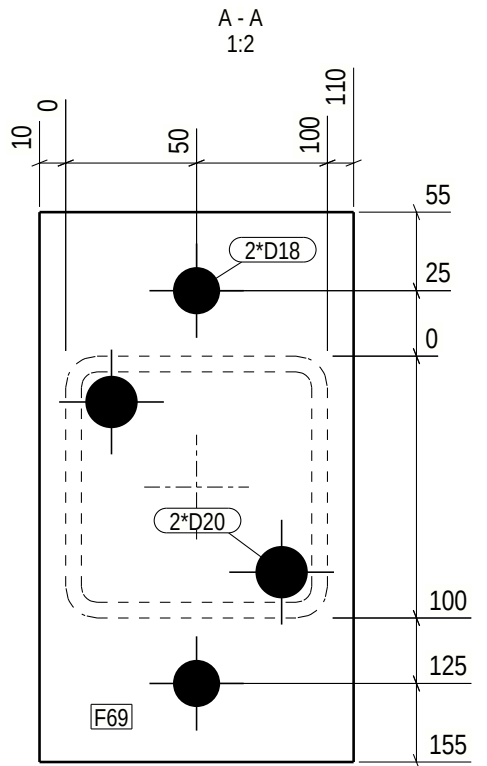
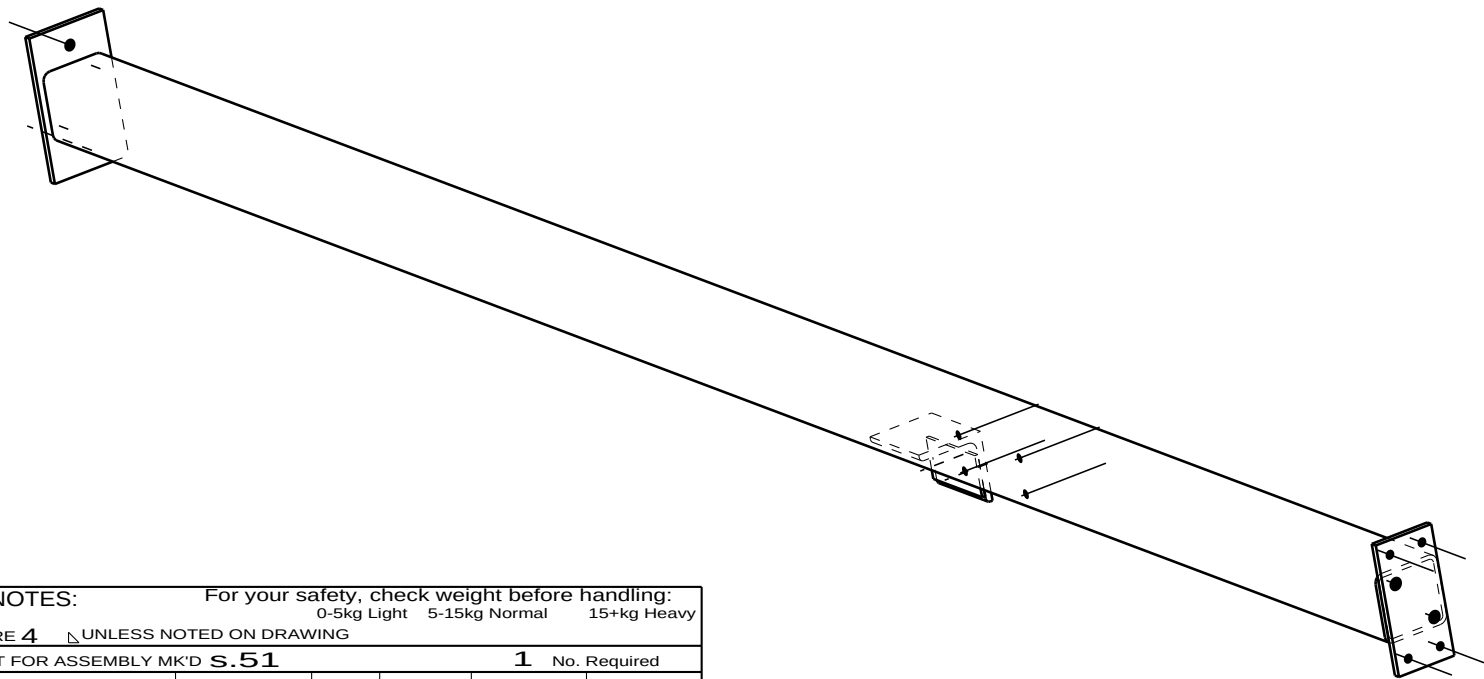
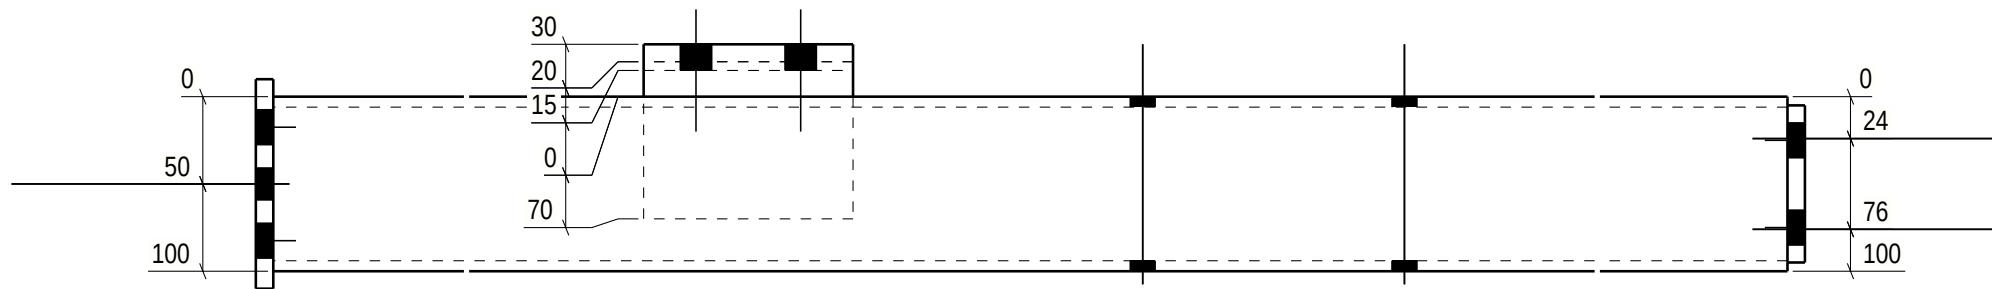


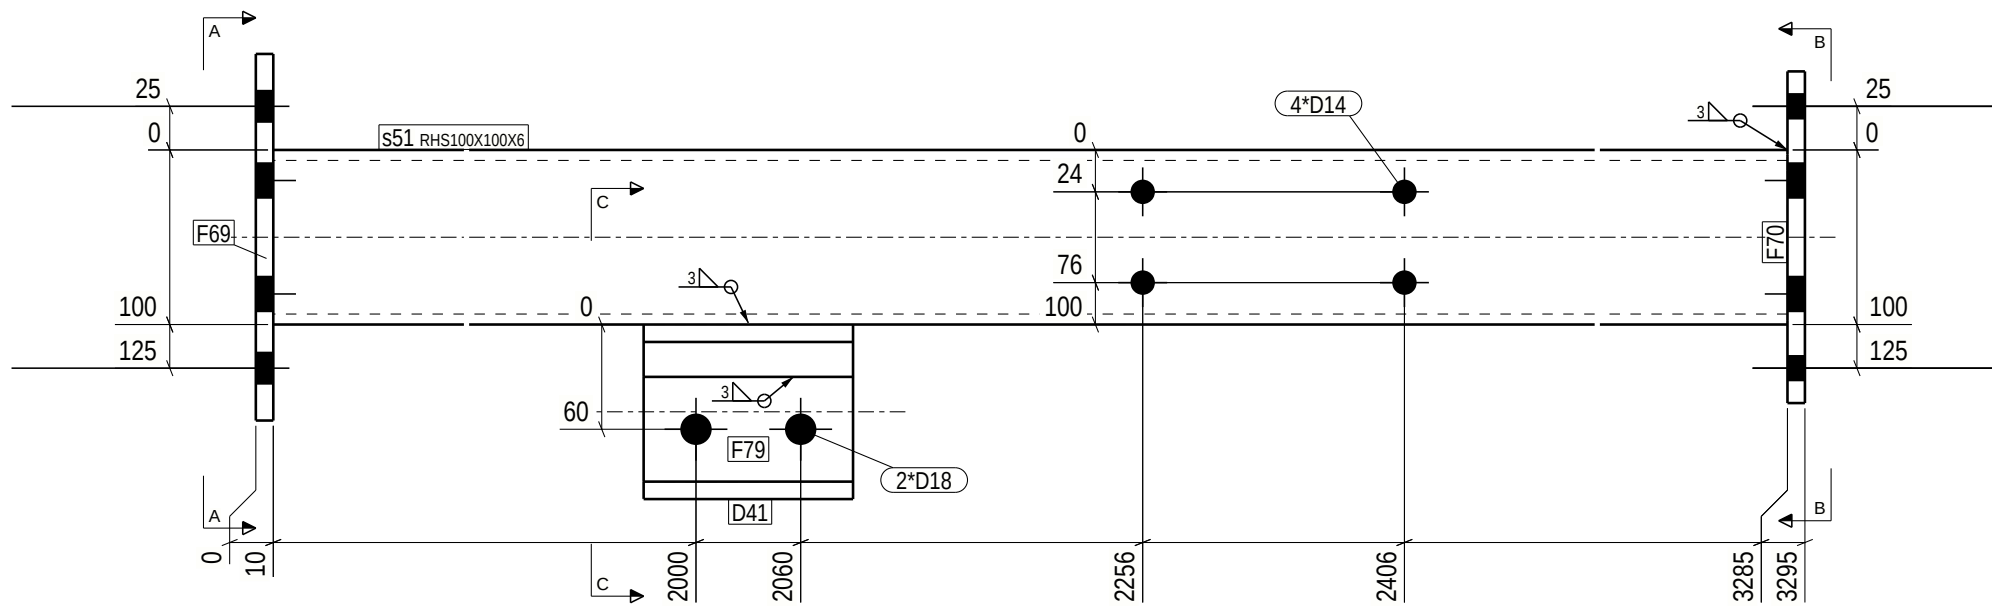

GENERAL NOTES: For your safety, check weight before handling:
0-5kg Light 5-15kg Normal 15+kg Heavy

ALL WELDS ARE 4 UNLESS NOTED ON DRAWING

MATERIAL LIST FOR ASSEMBLY MK'D s.51						1 No. Required
Mark	Profile	Material	No.	Length	Area	Weight
s51	RHS100X100X6	S355J2H	1	3275	1.3	55.4 !!
D41	L100*10	S355J2	1	120	0.0	1.8
F69	FL10*120	S355J2	1	210	0.1	2.0
F70	FL10*90	S355J2	1	190	0.0	1.3
F79	FL5*60	S355J2	1	120	0.0	0.3
Total					1.4	60.8

Finish Class
Standard

Surface treatment info:	Thickness/start point-> length	No.
Galvanised	/	1

Special
surface treatment

weld a = 4

PHASE	QUANTITY
3	1

* o 3 0 4 8 0 - 3 *  DS <i>Stalkonstruktion</i> * A s 5 1 *			
PROJECT	Akkasæter Lager- og vedlikeholdshall	EXEC. CLASS	EXC 2
MEMBER	Søyle	QUANTITY:	1
REVISION	ISSUED: 04.11.2025	DRAFTER:	ZLL SST
PROJECT No		30480-3	
DRAWING No.		s.51	