

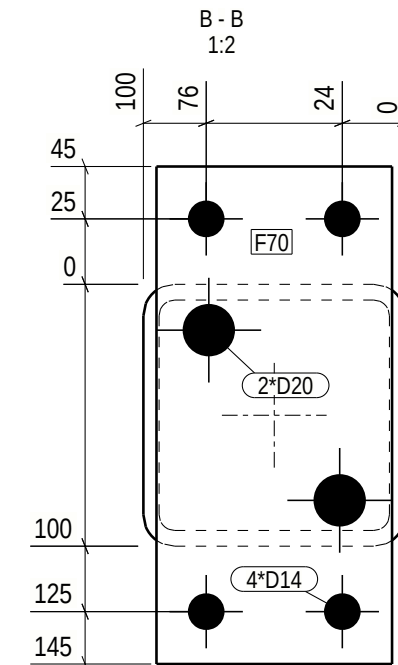
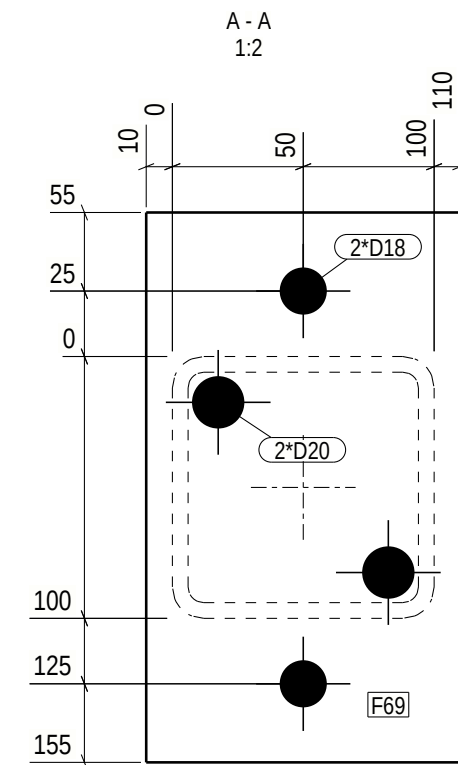
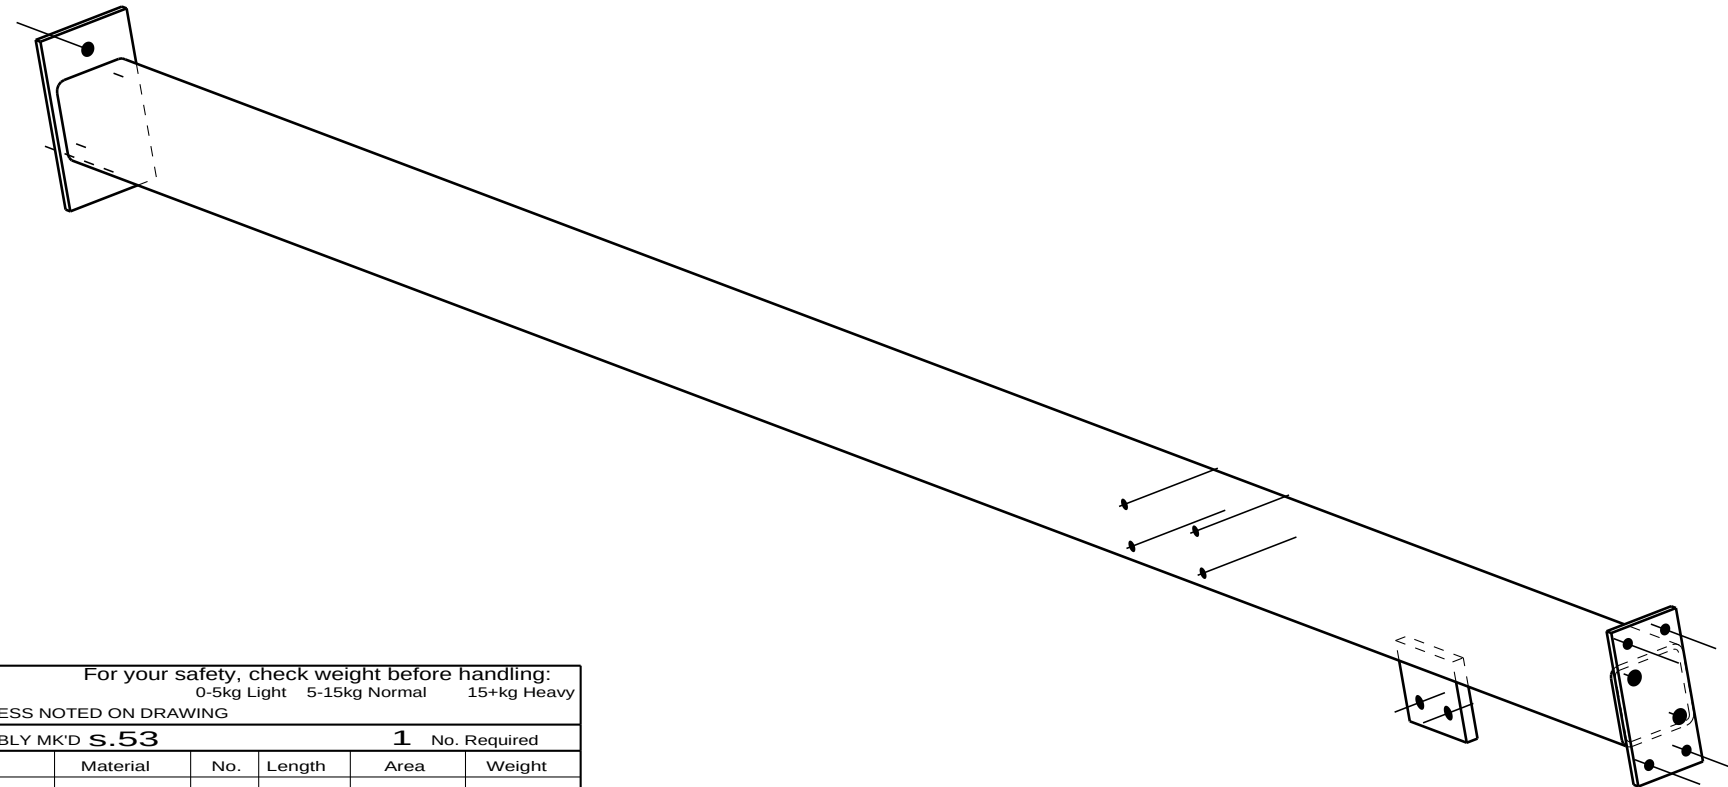


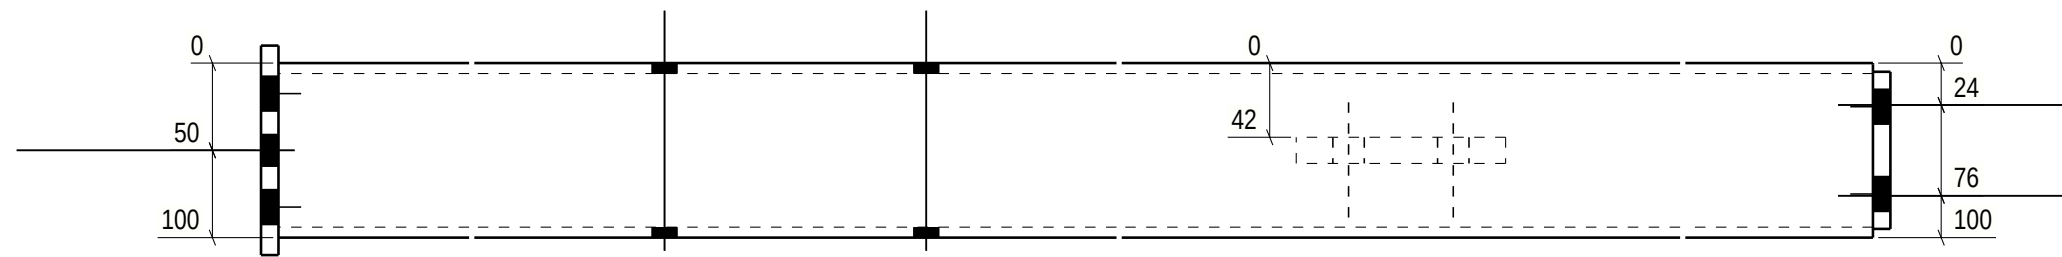

GENERAL NOTES:						
For your safety, check weight before handling:						
ALL WELDS ARE 4 UNLESS NOTED ON DRAWING						
MATERIAL LIST FOR ASSEMBLY MK'D S.53						
Mark	Profile	Material	No.	Length	Area	Weight
s53	RHS100X100X6	S355J2H	1	3275	1.3	55.4 !!
F69	FL10*120	S355J2	1	210	0.1	2.0
F70	FL10*90	S355J2	1	190	0.0	1.3
F82	FL15*100	S355J2	1	120	0.0	1.4
Total					1.4	60.1

Finish Class
Standard

Surface treatment info:	Thickness/start point-> length	No.
Galvanised	/	1

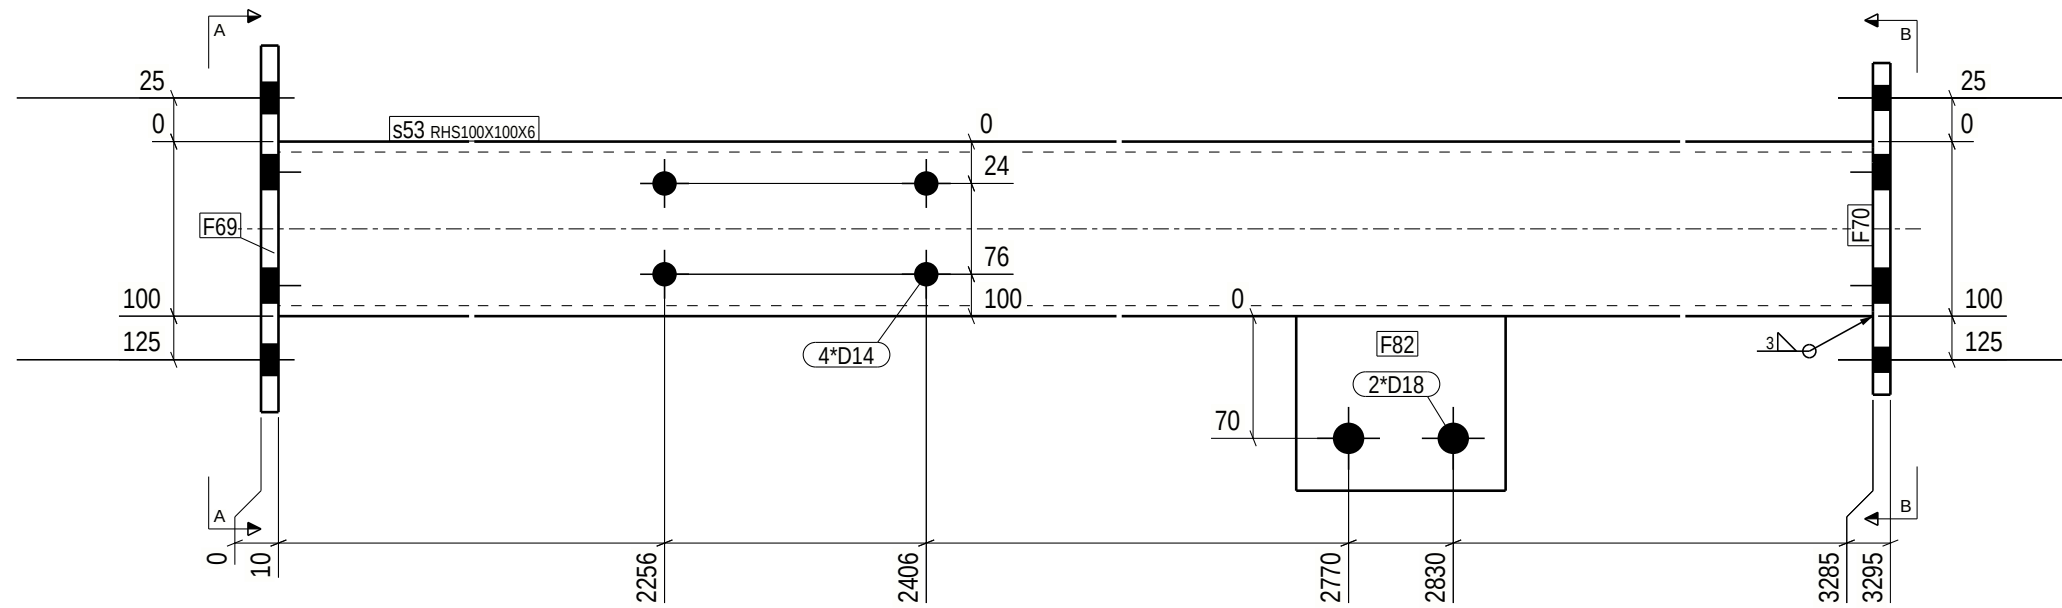

Special
surface treatment



weld a = 4

PHASE	QUANTITY
3	1

* o 3 0 4 8 0 - 3 * DS Steelkonstruktion * A s 5 3 *			
PROJECT	Akkasæter Lager- og vedlikeholdshall	EXEC. CLASS	EXC 2
MEMBER	Søyle	QUANTITY:	1
REVISION	ISSUED: 04.11.2025	DRAFTER: ZLL	PROJECT No 30480-3
	BIM control: SST	DRAWING No.	s.53