


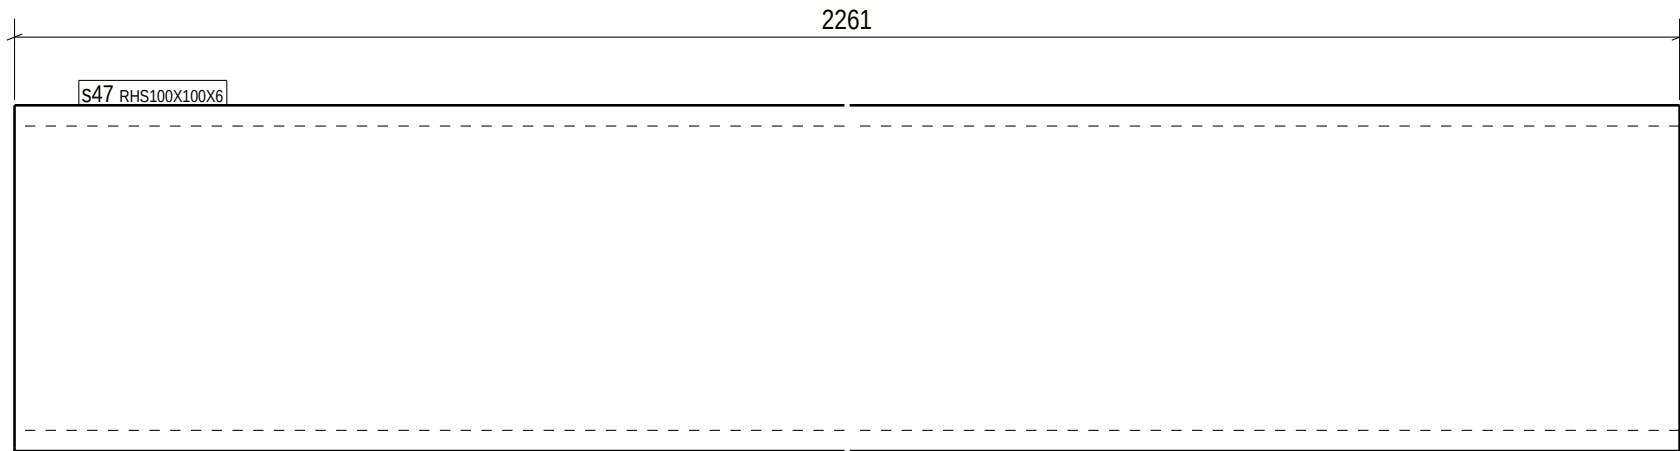

GENERAL NOTES:		For your safety, check weight before handling: 0-5kg Light 5-15kg Normal 15+kg Heavy				
MATERIAL LIST FOR PART - S47				2 PARTS REQUIRED		
POS. No.	PROFILE	No.	GRADE	L (mm)	AREA (m ²)	WEIGHT (kg)
s47	RHS100X100X6	1	S355J2H	2261	0.9	38.2 !!
TOTAL WEIGHT FOR				2	PARTS	76.5

Execution class: EXC 2		* o 3 0 4 8 0 - 3 *  DS <i>Stalkonstruktion</i> * W s 4 7 *			
No utilization on drawings = over 50%					
V-SEAM Utilization under 50% EXC 2=> Acc. to process control EXC 3=> 20% UT Utilization over 50% EXC 2=> 10% UT EXC 3=> 20% UT		PROJECT	Akkasæter Lager- og vedlikeholdshall		PHASE 3 / Phase 3
		MEMBER	Søje		QUANTITY: 2 PROJECT No 30480-3
		REVISION		ISSUED: 04.11.2025	DRAFTER: ZLL BIM control: SST DRAWING No. s.47