


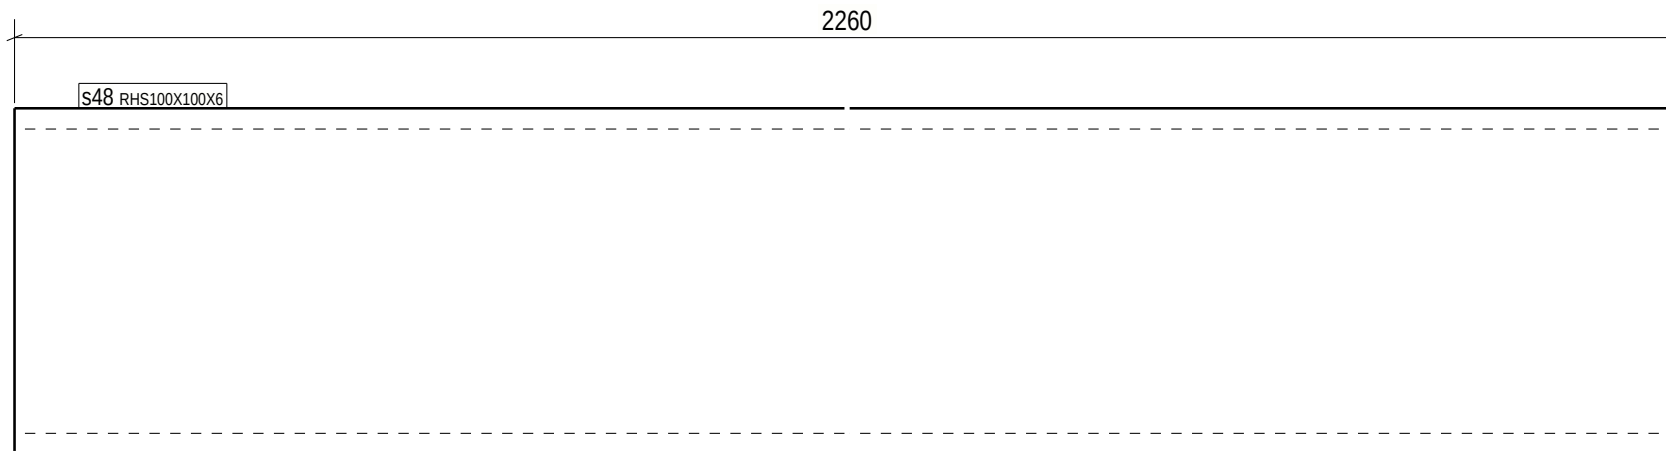

GENERAL NOTES:		For your safety, check weight before handling: 0-5kg Light 5-15kg Normal 15+kg Heavy				
MATERIAL LIST FOR PART - S48				1 PARTS REQUIRED		
POS. No.	PROFILE	No.	GRADE	L (mm)	AREA (m ²)	WEIGHT (kg)
s48	RHS100X100X6	1	S355J2H	2260	0.9	38.2 !!
TOTAL WEIGHT FOR				1	PARTS	38.2

Execution class: EXC 2	
No utilization on drawings = over 50%	
Part list	Qty.
GS	1

* o 3 0 4 8 0 - 3 *  DS <i>Stalkonstruktion</i> * W s 4 8 *			
PROJECT	Akkasæter Lager- og vedlikeholdshall		PHASE 3 / Phase 3
MEMBER	Søje	QUANTITY: 1	PROJECT No 30480-3
REVISION		ISSUED: 04.11.2025	DRAWING No. s.48
		DRAFTER: ZLL	BIM control: SST