


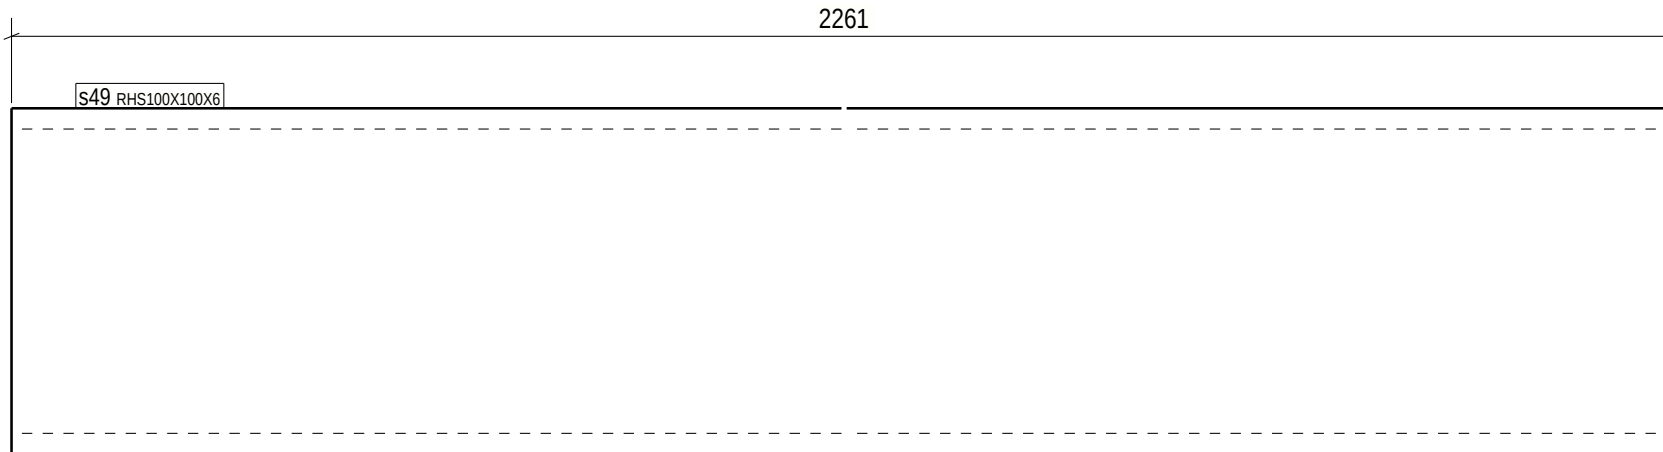

GENERAL NOTES:						
For your safety, check weight before handling:						
0-5kg Light 5-15kg Normal 15+kg Heavy						
MATERIAL LIST FOR PART - s49						
6 PARTS REQUIRED						
POS. No.	PROFILE	No.	GRADE	L (mm)	AREA (m ²)	WEIGHT (kg)
s49	RHS100X100X6	1	S355J2H	2261	0.9	38.2 !!
TOTAL WEIGHT FOR				6	PARTS	229.4

Part list	Qty.
GS	6

Execution class: EXC 2		* o 3 0 4 8 0 - 3 *  DS <i>Stålkonstruktion</i> * W s 4 9 *			
No utilization on drawings = over 50%					
V-SEAM Utilization under 50% EXC 2=> Acc. to process control EXC 3=> 20% UT Utilization over 50% EXC 2=> 10% UT EXC 3=> 20% UT		PROJECT	Akkasæter Lager- og vedlikeholdshall		PHASE 3 / Phase 3
		MEMBER	Søyle	QUANTITY: 6	PROJECT No 30480-3
		REVISION		ISSUED: 04.11.2025	DRAWING No. s.49
				DRAFTER: ZLL BIM control: SST	