


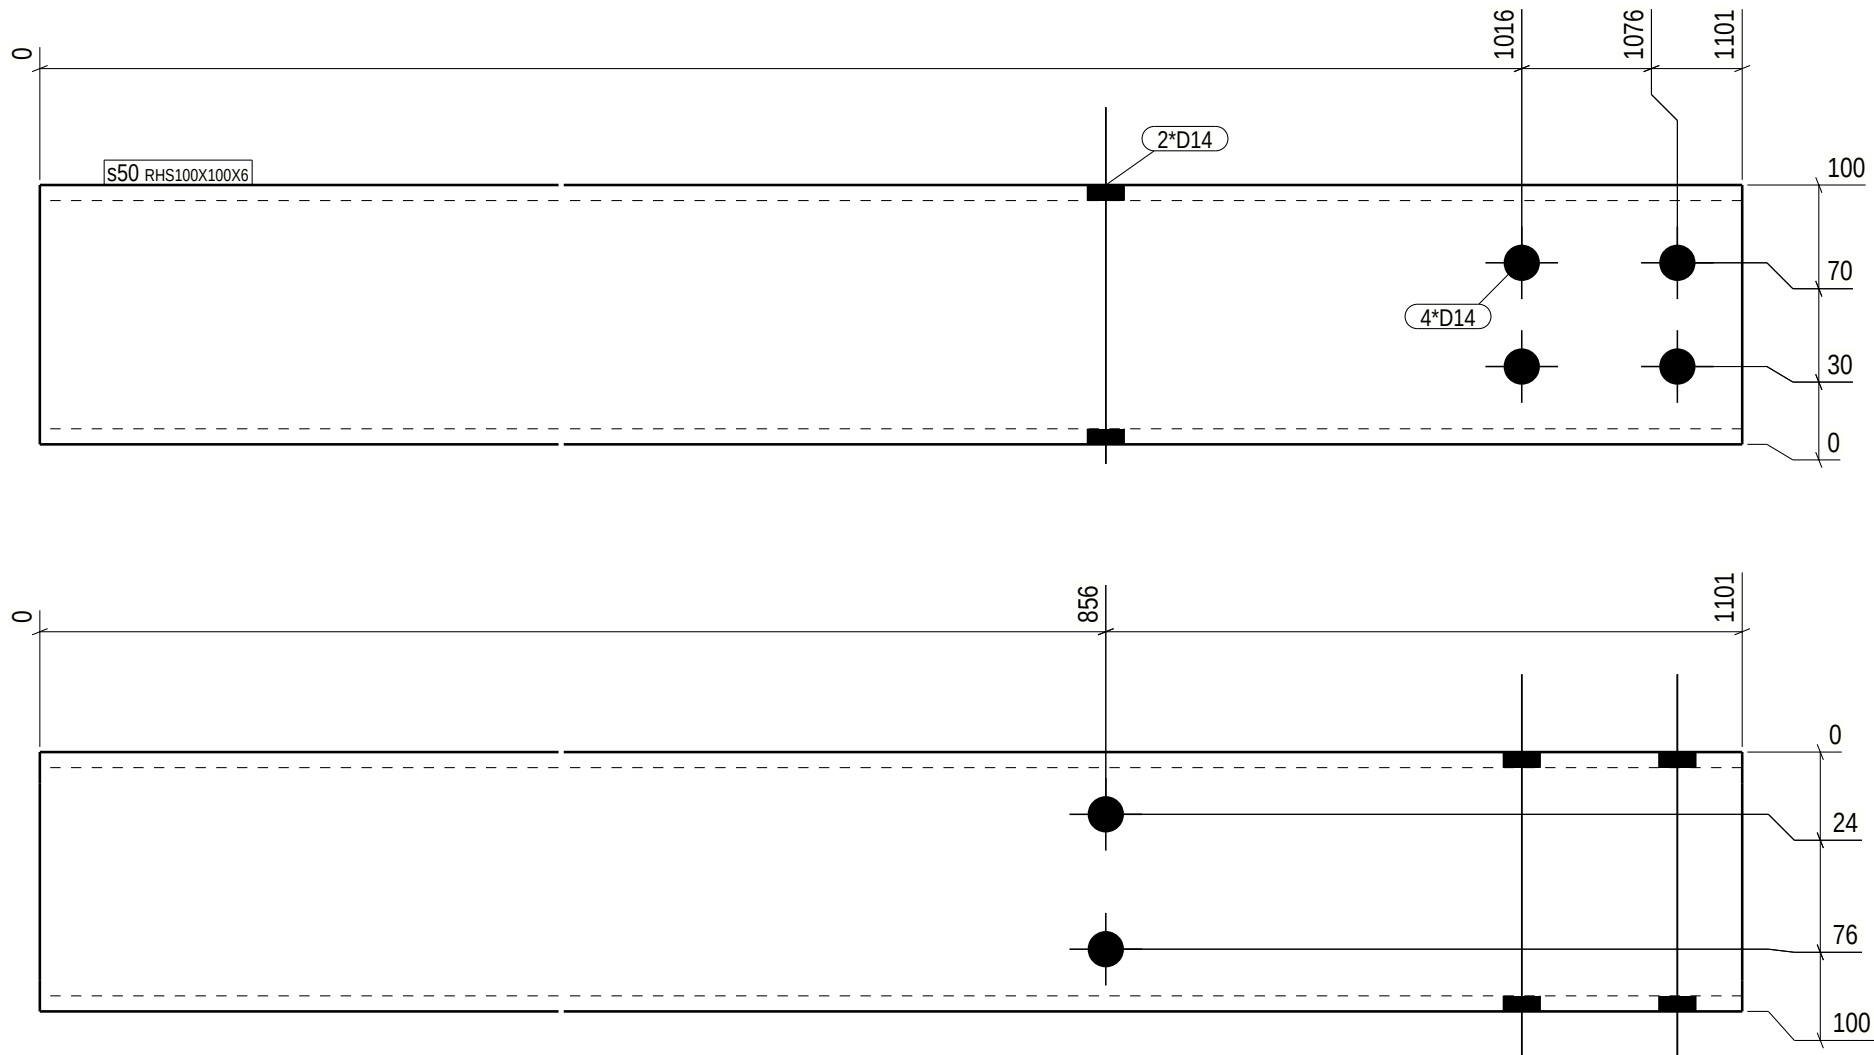

GENERAL NOTES:

For your safety, check weight before handling:
0-5kg Light 5-15kg Normal 15+kg Heavy

MATERIAL LIST FOR PART - s50

4 PARTS REQUIRED

POS. No.	PROFILE	No.	GRADE	L (mm)	AREA (m ²)	WEIGHT (kg)
s50	RHS100X100X6	1	S355J2H	1101	0.4	18.6 !!

TOTAL WEIGHT FOR 4 PARTS 74.5

Part list	Qty.
GS	4

Execution class: EXC 2

No utilization on drawings = over 50%

V-SEAM
Utilization under 50%
EXC 2=> Acc. to process control
EXC 3=> 20% UT
Utilization over 50%
EXC 2=> 10% UT
EXC 3=> 20% UT

* o 3 0 4 8 0 - 3 *



DS Sivilkonstruksjon

* W s 5 0 *

PROJECT	Akkasæter Lager- og vedlikeholdshall		PHASE	3 / Phase 3	
MEMBER	Søyle		QUANTITY:	4	PROJECT No 30480-3
REVISION		ISSUED: 04.11.2025	DRAFTER: ZLL	BIM control: SST	DRAWING No. s.50