


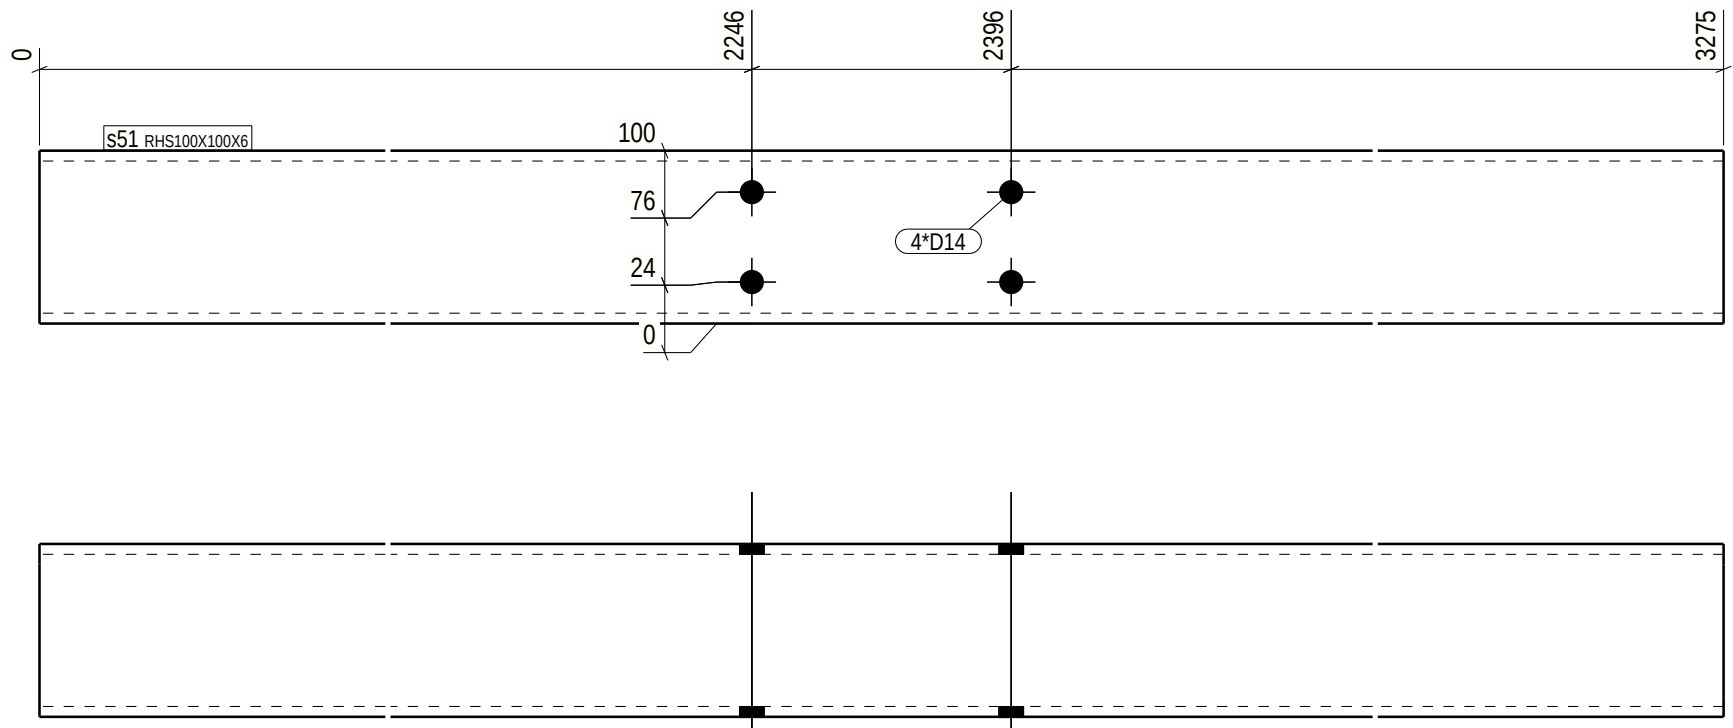

GENERAL NOTES: For your safety, check weight before handling:
0-5kg Light 5-15kg Normal 15+kg Heavy

MATERIAL LIST FOR PART - S51						1 PARTS REQUIRED
POS. No.	PROFILE	No.	GRADE	L (mm)	AREA (m ²)	WEIGHT (kg)
s51	RHS100X100X6	1	S355J2H	3275	1.3	55.4 !!
TOTAL WEIGHT FOR				1	PARTS	55.4

Execution class: EXC 2

No utilization on drawings = over 50%
V-SEAM Utilization under 50% EXC 2=> Acc. to process control EXC 3=> 20% UT Utilization over 50% EXC 2=> 10% UT EXC 3=> 20% UT

Part list	Qty.
GS	1

* o 3 0 4 8 0 - 3 *  DS <i>Skalkonstruktion</i> * W s 5 1 *			
PROJECT	Akkasæter Lager- og vedlikeholdshall		PHASE 3 / Phase 3
MEMBER	Søje	QUANTITY: 1	PROJECT No 30480-3
REVISION	ISSUED: 04.11.2025	DRAFTER: ZLL BIM control: SST	DRAWING No. s.51