


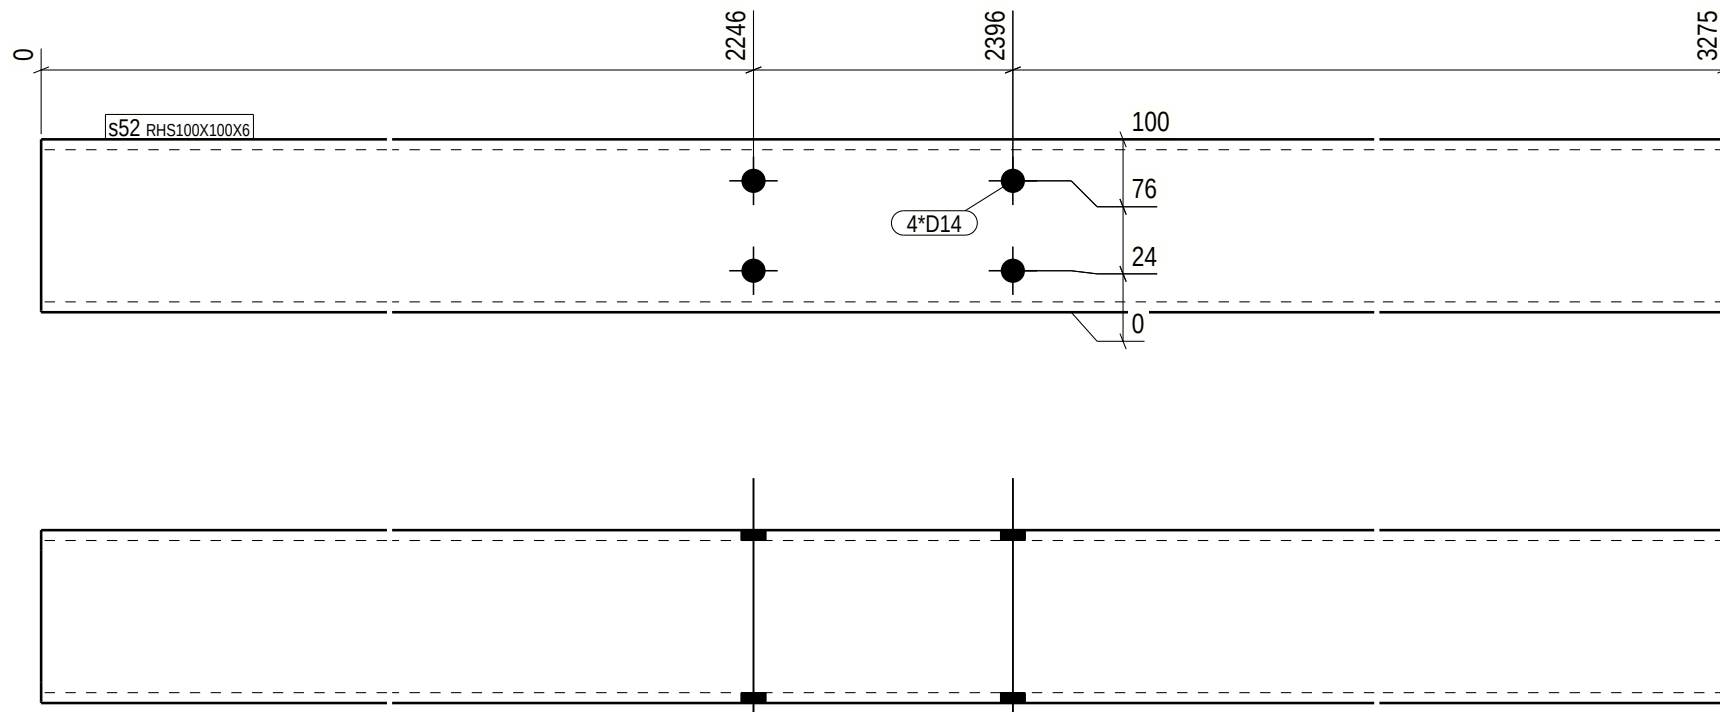

GENERAL NOTES:						
For your safety, check weight before handling:						
0-5kg Light 5-15kg Normal 15+kg Heavy						
MATERIAL LIST FOR PART - S52						
2 PARTS REQUIRED						
POS. No.	PROFILE	No.	GRADE	L (mm)	AREA (m ²)	WEIGHT (kg)
s52	RHS100X100X6	1	S355J2H	3275	1.3	55.4 !!
TOTAL WEIGHT FOR				2	PARTS	110.8

Part list		Qty.	Execution class: EXC 2			
GS		2	No utilization on drawings = over 50%			
			V-SEAM Utilization under 50% EXC 2=> Acc. to process control EXC 3=> 20% UT Utilization over 50% EXC 2=> 10% UT EXC 3=> 20% UT			
			* o 3 0 4 8 0 - 3 *  DS <i>Skalkonstruktion</i> * W s 5 2 *			
PROJECT		Akkasæter Lager- og vedlikeholdshall			PHASE 3 / Phase 3	
MEMBER		Søyle			QUANTITY: 2	PROJECT No 30480-3
REVISION		ISSUED: 04.11.2025			DRAFTER: ZLL BIM control: SST	DRAWING No. s.52