


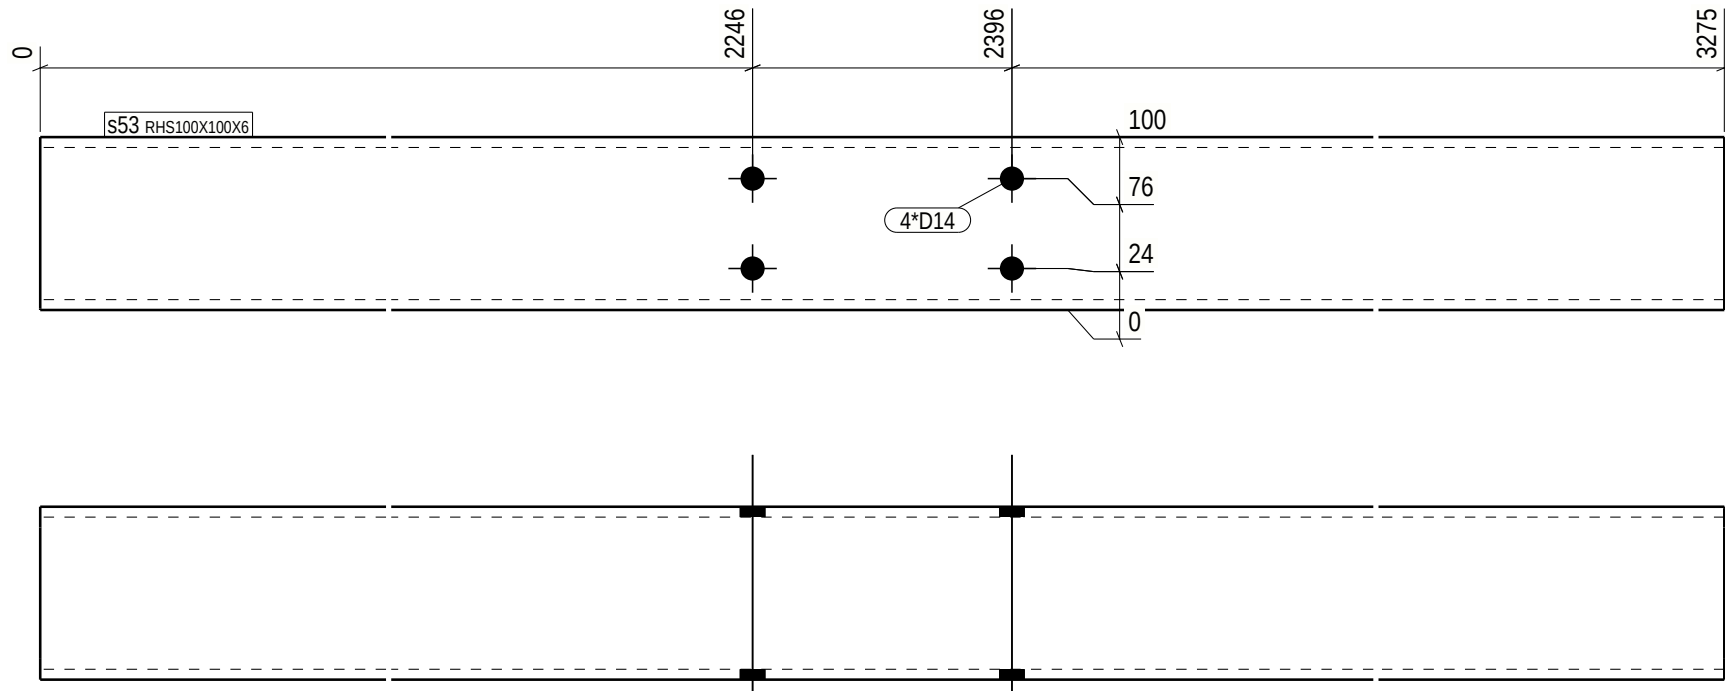

GENERAL NOTES:						
For your safety, check weight before handling:						
0-5kg Light 5-15kg Normal 15+kg Heavy						
MATERIAL LIST FOR PART - S53				1 PARTS REQUIRED		
POS. No.	PROFILE	No.	GRADE	L (mm)	AREA (m ²)	WEIGHT (kg)
s53	RHS100X100X6	1	S355J2H	3275	1.3	55.4 !!
TOTAL WEIGHT FOR				1	PARTS	55.4

Part list	Qty.
GS	1

Execution class: EXC 2	
No utilization on drawings = over 50%	
V-SEAM Utilization under 50% EXC 2=> Acc. to process control EXC 3=> 20% UT Utilization over 50% EXC 2=> 10% UT EXC 3=> 20% UT	

* o 3 0 4 8 0 - 3 *  DS <i>Stalkonstruktion</i> * W s 5 3 *			
PROJECT	Akkasæter Lager- og vedlikeholdshall		PHASE 3 / Phase 3
MEMBER	Søyle	QUANTITY: 1	PROJECT No 30480-3
REVISION		ISSUED: 04.11.2025	DRAWING No. s.53
		DRAFTER: ZLL	BIM control: SST