


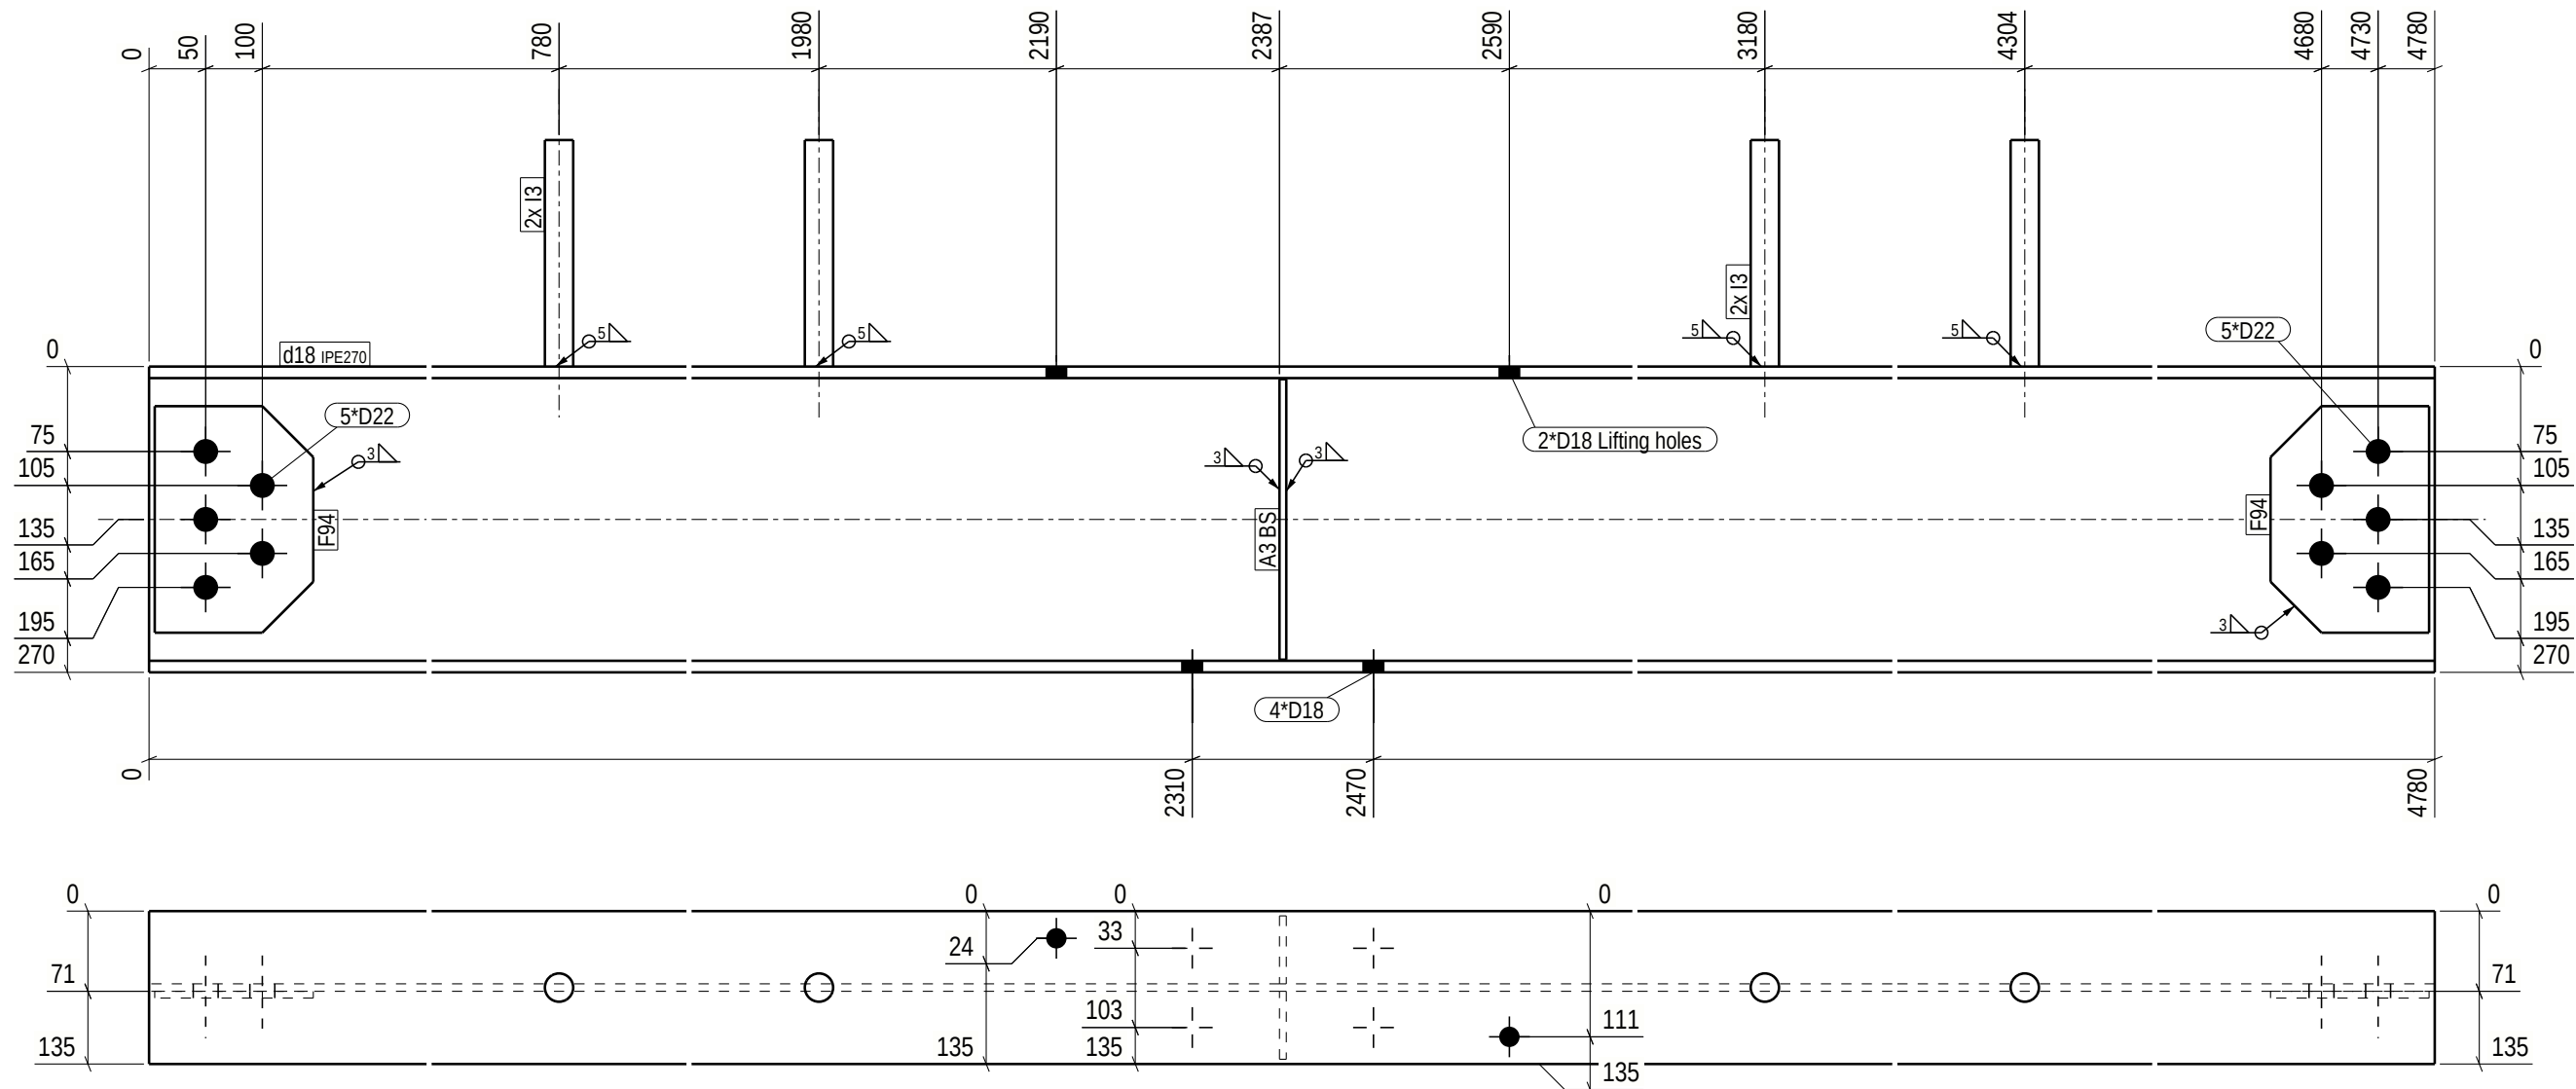

GENERAL NOTES: For your safety, check weight before handling:  
0-5kg Light 5-15kg Normal 15+kg Heavy

ALL WELDS ARE 4 UNLESS NOTED ON DRAWING

MATERIAL LIST FOR ASSEMBLY MK'D **d.18** **1** No. Required

| Mark  | Profile | Material | No. | Length | Area | Weight   |
|-------|---------|----------|-----|--------|------|----------|
| d18   | IPE270  | S355J2   | 1   | 4780   | 5.0  | 172.2 !! |
| A3    | FL6*60  | S355J2   | 2   | 248    | 0.0  | 0.7      |
| F94   | FL6*140 | S355J2   | 2   | 200    | 0.1  | 1.2      |
| I3    | REBAR25 | B550B    | 4   | 200    | 0.0  | 0.7      |
| Total |         |          |     |        | 5.2  | 179.0    |

Finish Class  
Standard

|                         |                                 |     |
|-------------------------|---------------------------------|-----|
| Surface treatment info: | Thickness/start point--> length | No. |
| Overall Painting        | Primerµm whole asse***          | 1   |



Special  
surface treatment



weld a = 4

| PHASE | QUANTITY |
|-------|----------|
| 1     | 1        |

|   |                                      |              |             |
|---|--------------------------------------|--------------|-------------|
| * o 3 0 4 8 0 - 1 *  <b>DS</b> <i>Stalkonstruktion</i> * A d 1 8 * |                                      |              |             |
| PROJECT   | Akkasæter Lager- og vedlikeholdshall |              | EXEC. CLASS |
| MEMBER   | Drager                               |              | PROJECT No  |
| REVISION   | ISSUED: 07.11.2025                   |              | DRAWING No. |
| QUANTITY: 1   |                                      | DRAFTER: ZLL | 30480-1     |
| BIM control: SST   |                                      | d.18         |             |