


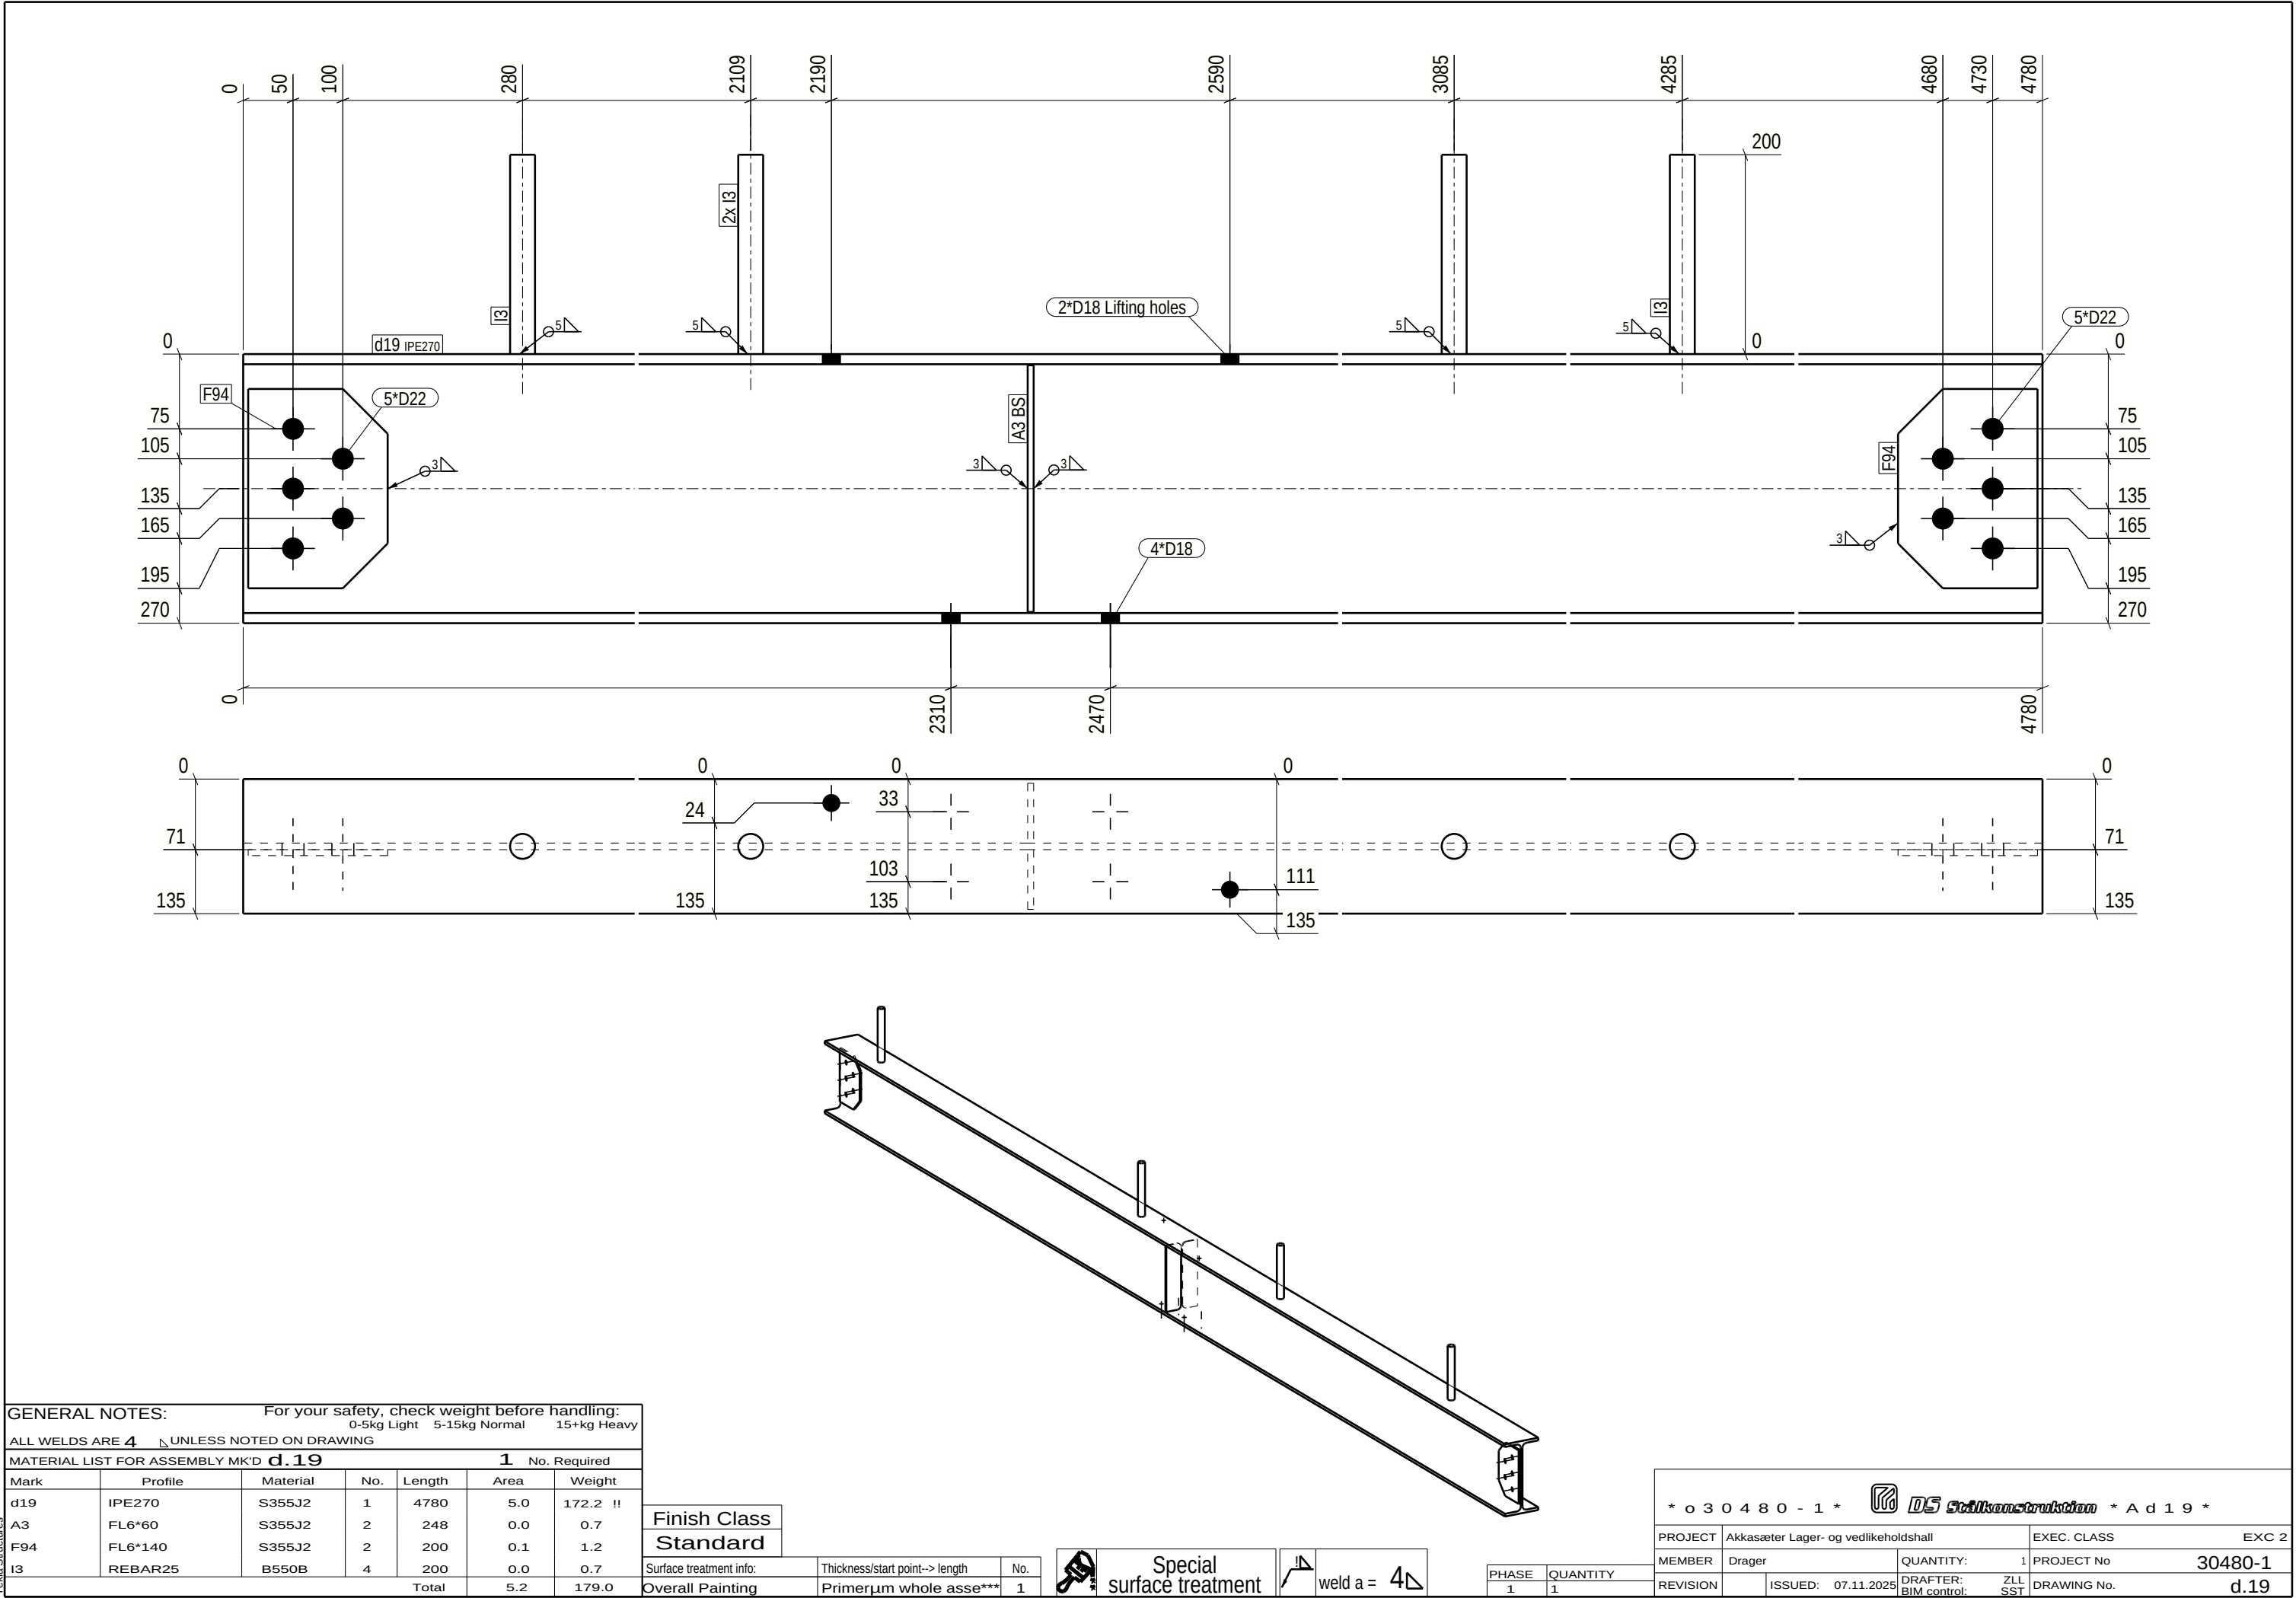

GENERAL NOTES: For your safety, check weight before handling:						
ALL WELDS ARE 4 UNLESS NOTED ON DRAWING						
MATERIAL LIST FOR ASSEMBLY MK'D d.19						
Mark	Profile	Material	No.	Length	Area	Weight
d19	IPE270	S355J2	1	4780	5.0	172.2 !!
A3	FL6*60	S355J2	2	248	0.0	0.7
F94	FL6*140	S355J2	2	200	0.1	1.2
I3	REBAR25	B550B	4	200	0.0	0.7
Total					5.2	179.0

Finish Class
Standard

Surface treatment info:	Thickness/start point-> length	No.
Overall Painting	Primerµm whole asse***	1

Special
surface treatment

weld a = 4

PHASE	QUANTITY
1	1

* o 3 0 4 8 0 - 1 * DS Steelkonstruktion * A d 1 9 *			
PROJECT	Akkasæter Lager- og vedlikeholdshall	EXEC. CLASS	EXC 2
MEMBER	Drager	QUANTITY:	1
REVISION	ISSUED: 07.11.2025	DRAFTER: ZLL	PROJECT No 30480-1
		BIM control: SST	DRAWING No. d.19