
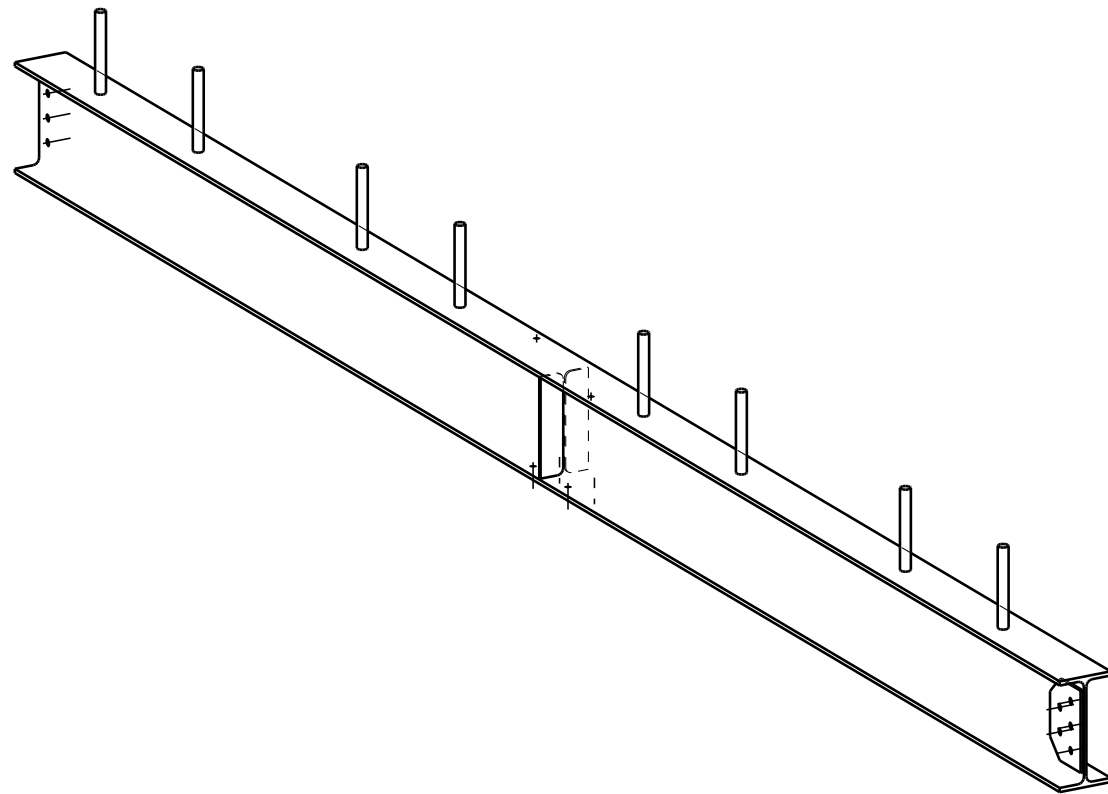


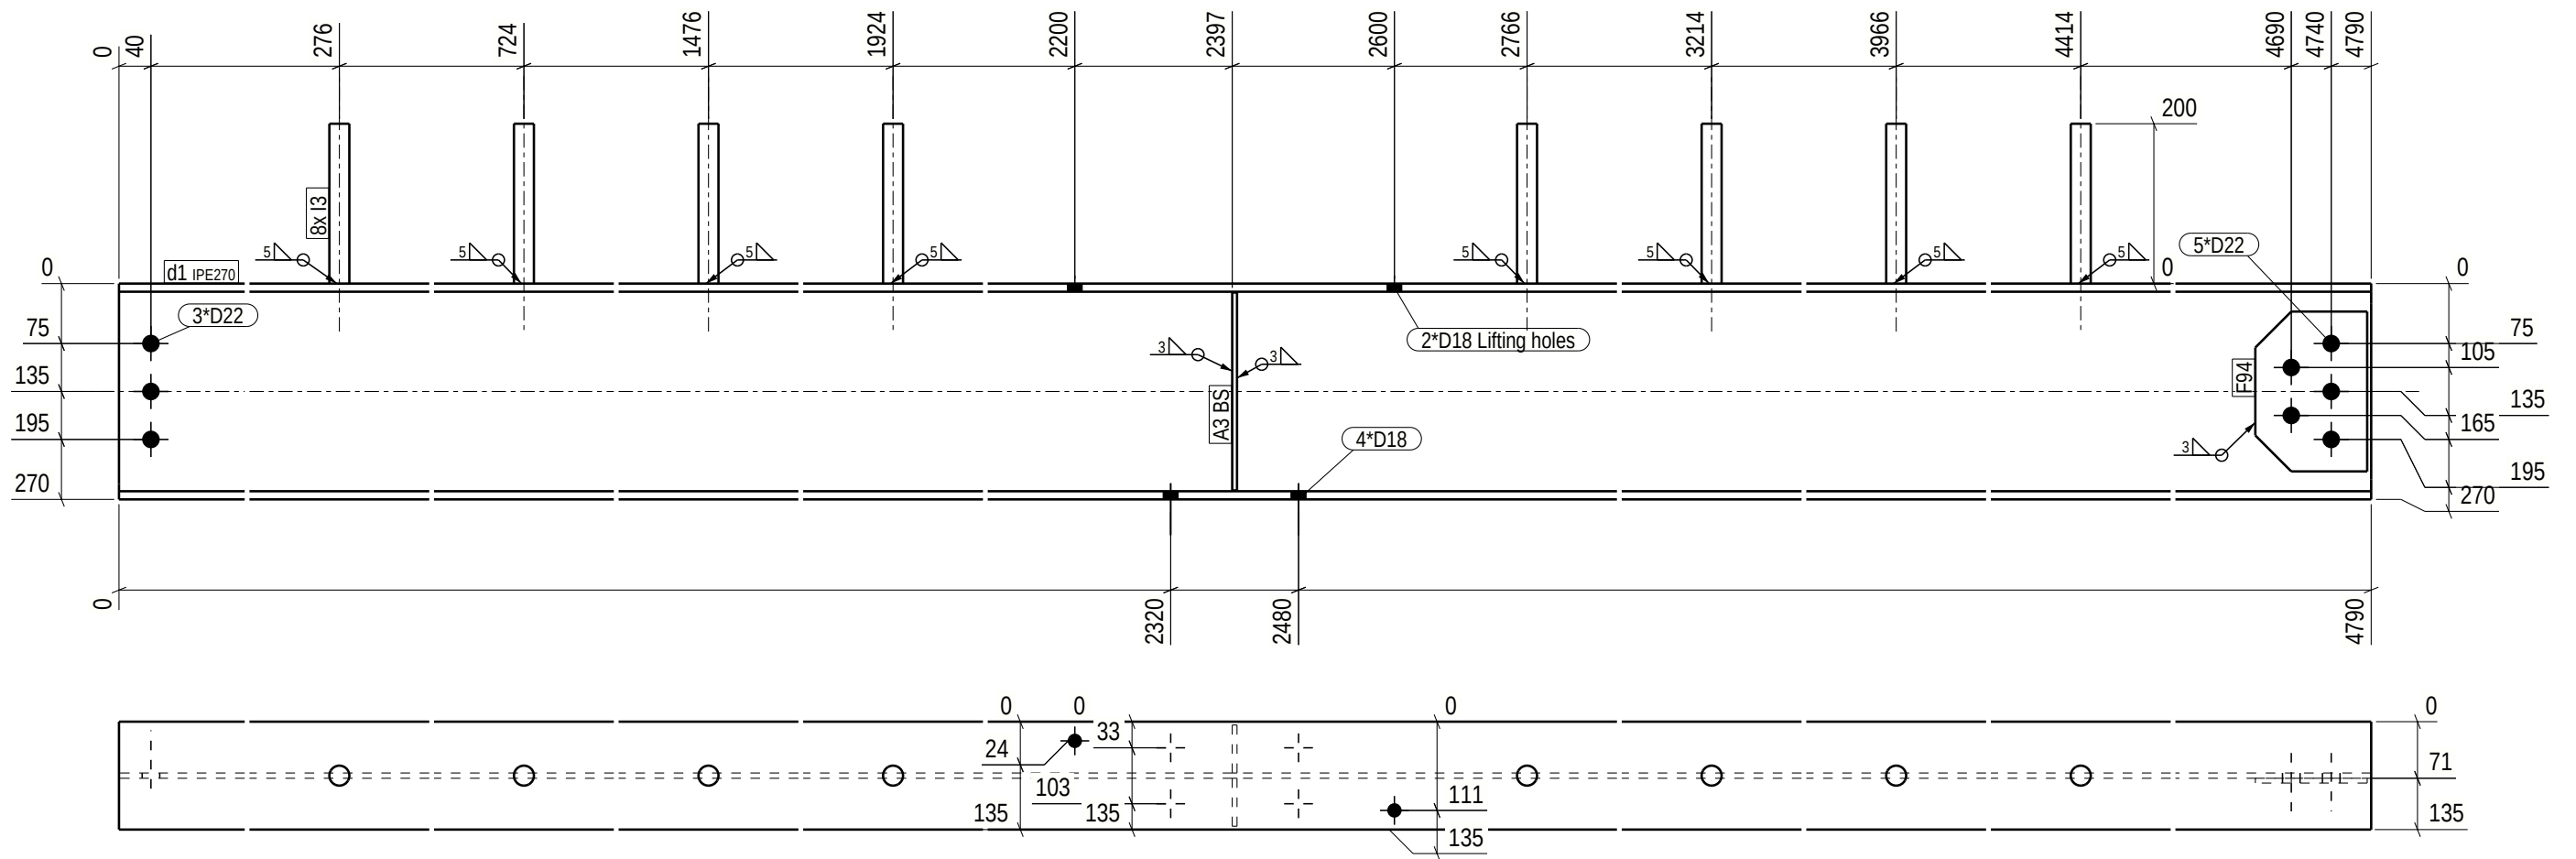

GENERAL NOTES: For your safety, check weight before handling:
0-5kg Light 5-15kg Normal 15+kg Heavy

ALL WELDS ARE **4** UNLESS NOTED ON DRAWING

MATERIAL LIST FOR ASSEMBLY MK'D d.1						1 No. Required
Mark	Profile	Material	No.	Length	Area	Weight
d1	IPE270	S355J2	1	4790	5.0	172.6 !!
A3	FL6*60	S355J2	2	248	0.0	0.7
F94	FL6*140	S355J2	1	200	0.1	1.2
I3	REBAR25	B550B	8	200	0.0	0.7
Total					5.2	181.1

Finish Class
Standard

Surface treatment info:	Thickness/start point-> length	No.
Overall Painting	C2M RAL7016µm whole	**1



Special
surface treatment



weld a = 4

PHASE	QUANTITY
1	1

* o 3 0 4 8 0 - 1 *  DS <i>Stalkonstruktion</i> * A d 1 *			
PROJECT	Akkasæter Lager- og vedlikeholdshall		EXEC. CLASS EXC 2
MEMBER	Drager	QUANTITY: 1	PROJECT No 30480-1
REVISION		ISSUED: 07.11.2025	DRAWING No. d.1
		DRAFTER: ZLL	
		BIM control: SST	