
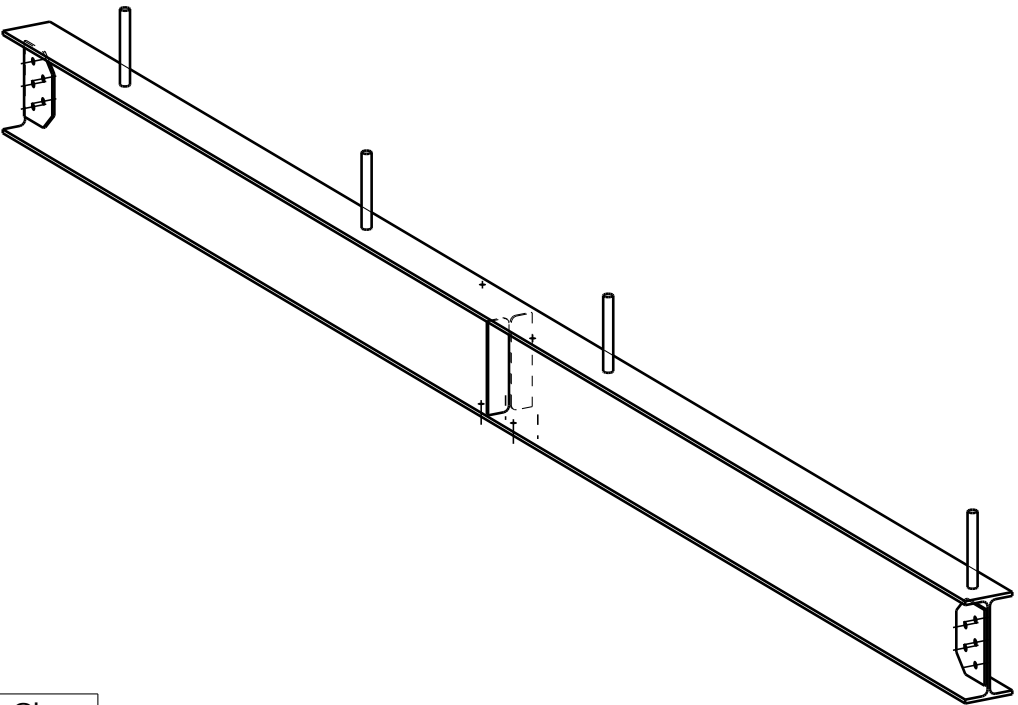


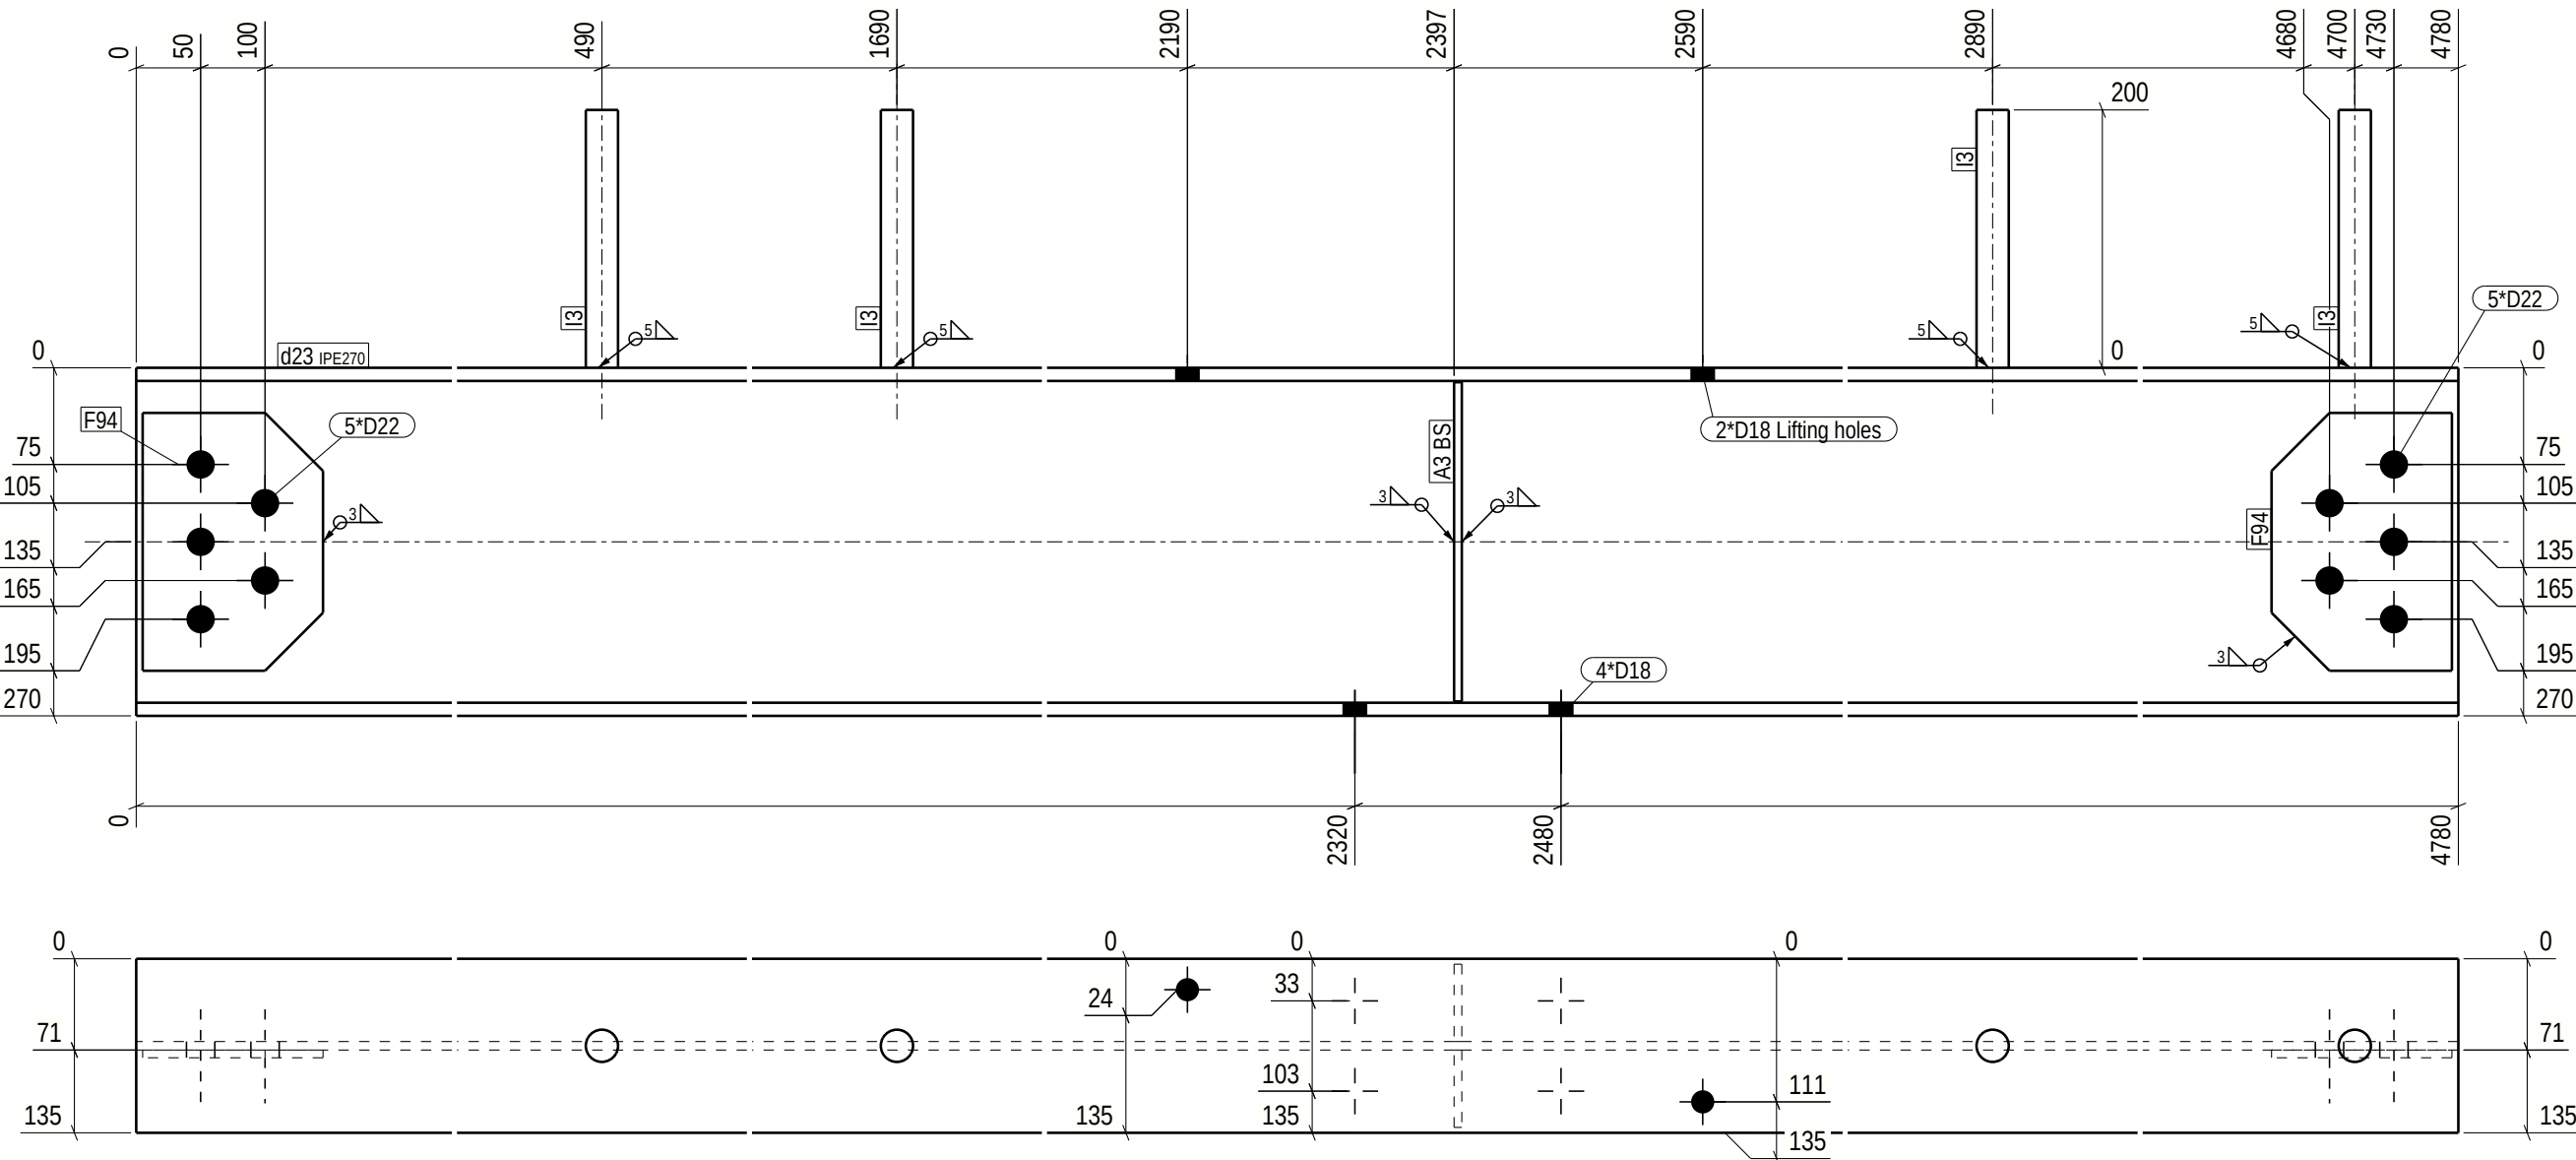

GENERAL NOTES: For your safety, check weight before handling:
0-5kg Light 5-15kg Normal 15+kg Heavy

ALL WELDS ARE 4 UNLESS NOTED ON DRAWING

MATERIAL LIST FOR ASSEMBLY MK'D **d.23** **1** No. Required

Mark	Profile	Material	No.	Length	Area	Weight
d23	IPE270	S355J2	1	4780	5.0	172.2 !!
A3	FL6*60	S355J2	2	248	0.0	0.7
F94	FL6*140	S355J2	2	200	0.1	1.2
I3	REBAR25	B550B	4	200	0.0	0.7
Total					5.2	179.0

Finish Class
Standard

Surface treatment info:	Thickness/start point-> length	No.
Overall Painting	Primerµm whole asse***	1



Special
surface treatment



weld a = 4

PHASE	QUANTITY
1	1

* o 3 0 4 8 0 - 1 *  DS <i>Stalkonstruktion</i> * A d 2 3 *			
PROJECT	Akkasæter Lager- og vedlikeholdshall	EXEC. CLASS	EXC 2
MEMBER	Drager	QUANTITY:	1
REVISION		ISSUED:	07.11.2025
		DRAFTER:	ZLL
		BIM control:	SST
PROJECT No		30480-1	
DRAWING No.		d.23	