
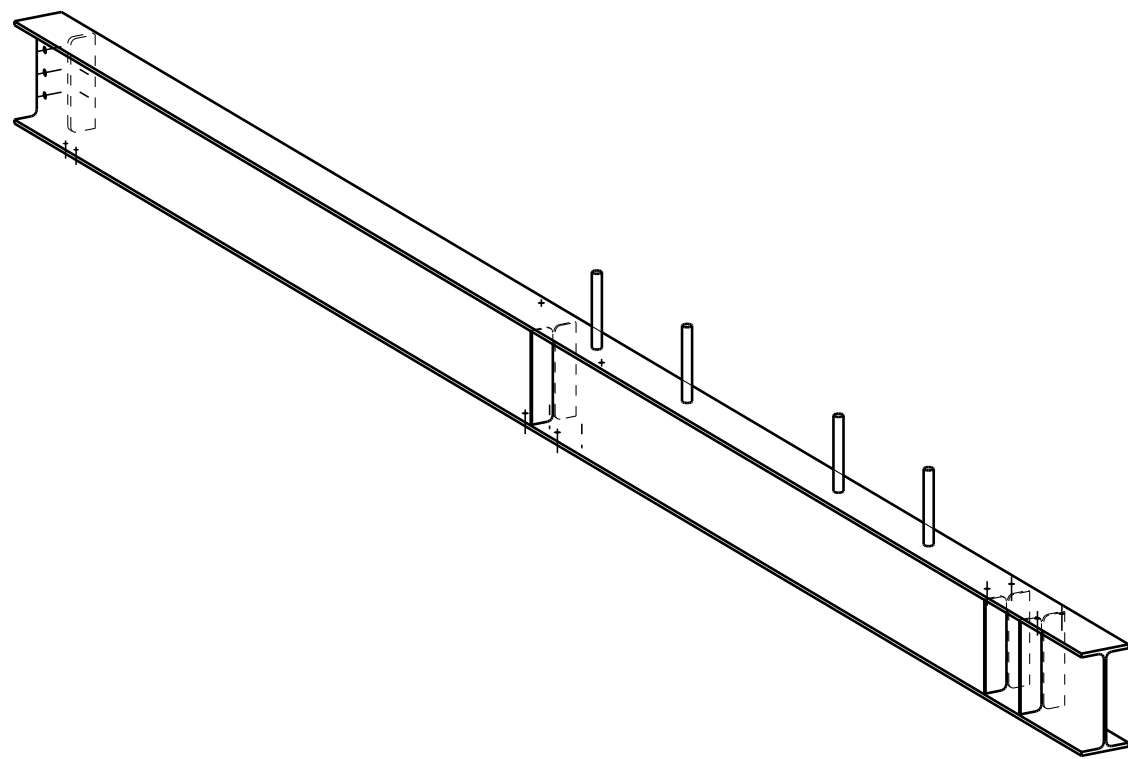


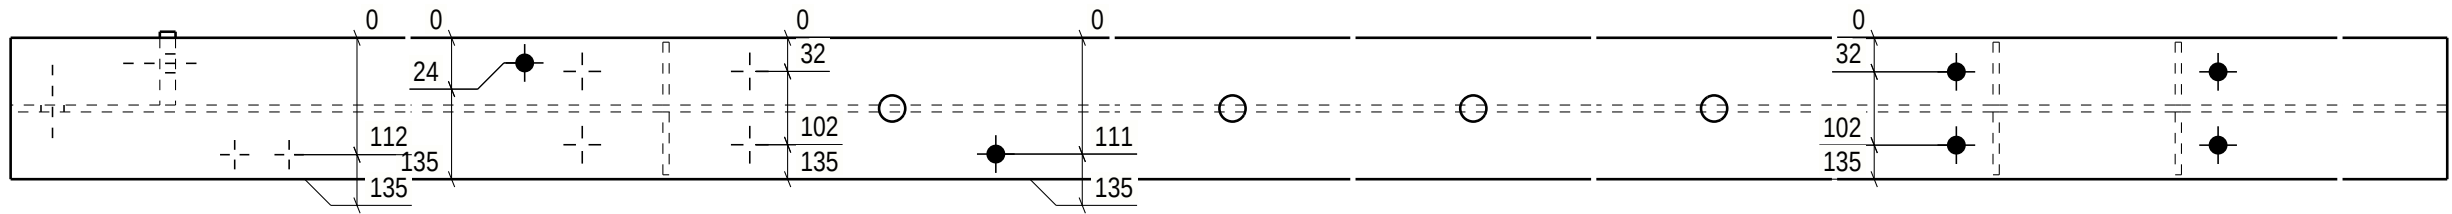

* o 3 0 4 8 0 - 1 *				 DS <i>Stilkonstruktion</i>		* A d 3 *	
PROJECT	Akkasæter Lager- og vedlikeholdshall				EXEC. CLASS	EXC 2	
MEMBER	Drager		QUANTITY:	1	PROJECT No	30480-1	
REVISION	ISSUED: 07.11.2025		DRAFTER: ZLL BIM control:		DRAWING No.	d.3	