
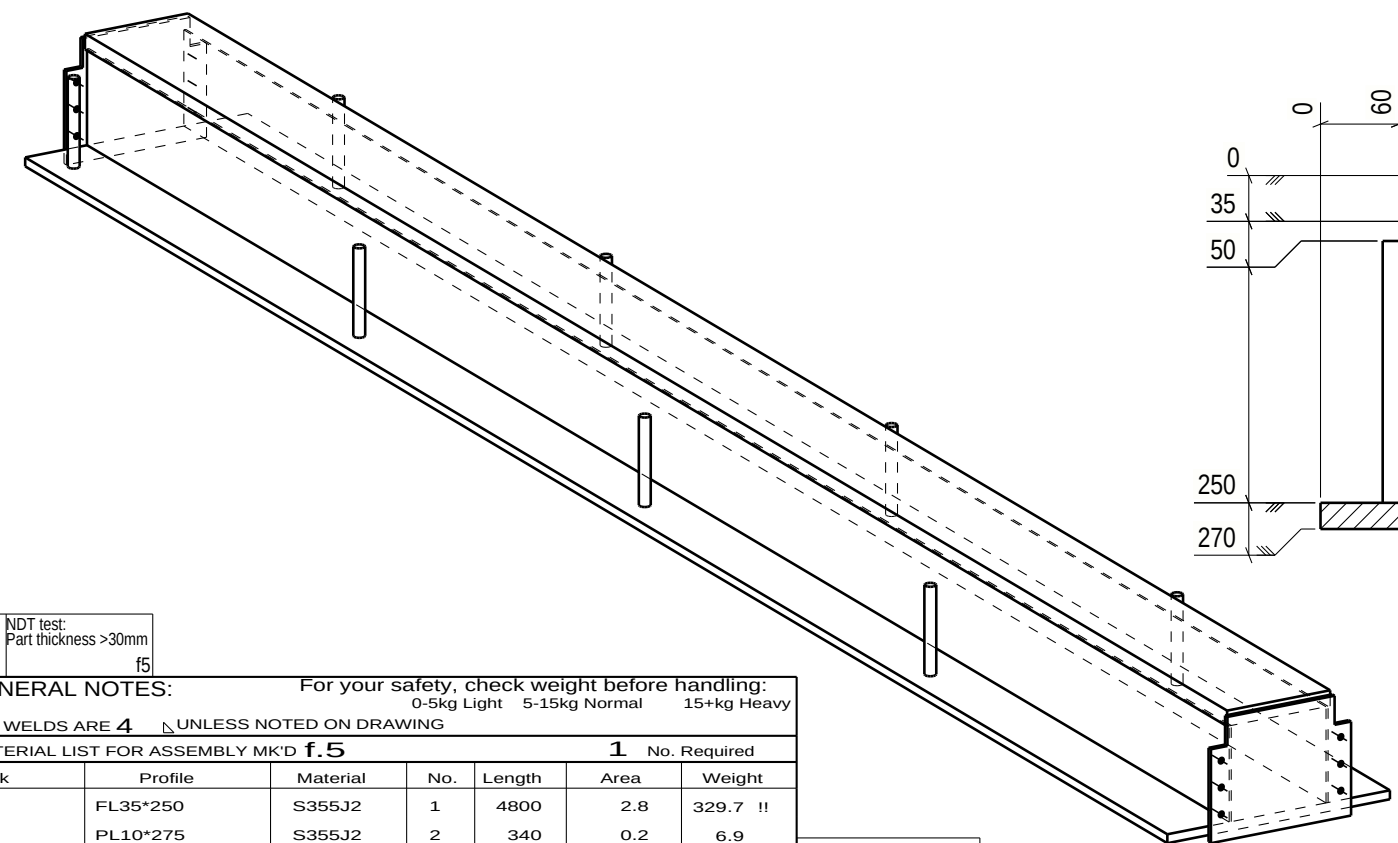
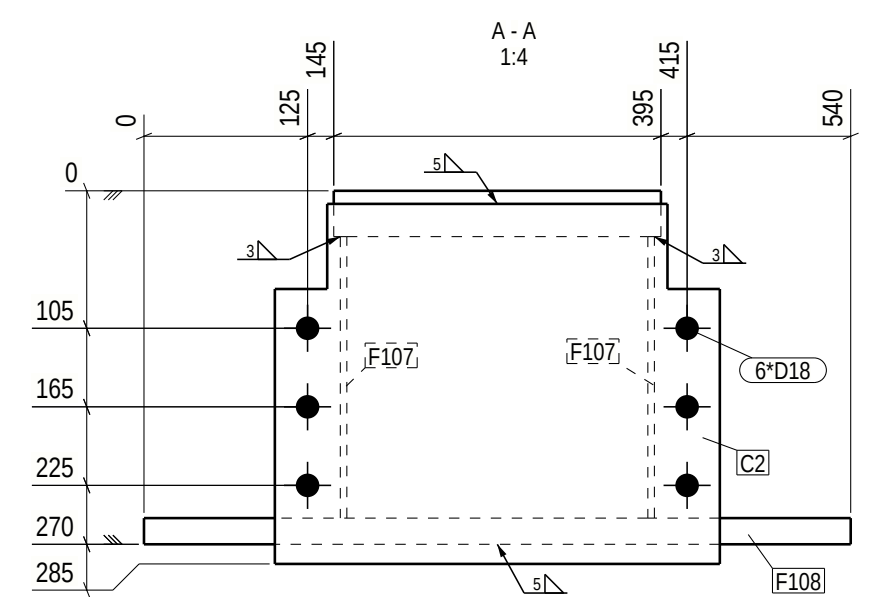
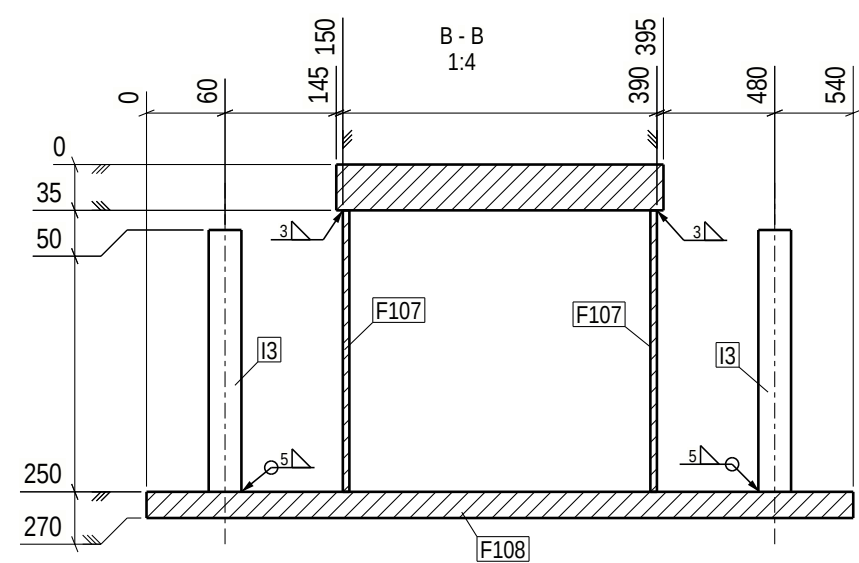
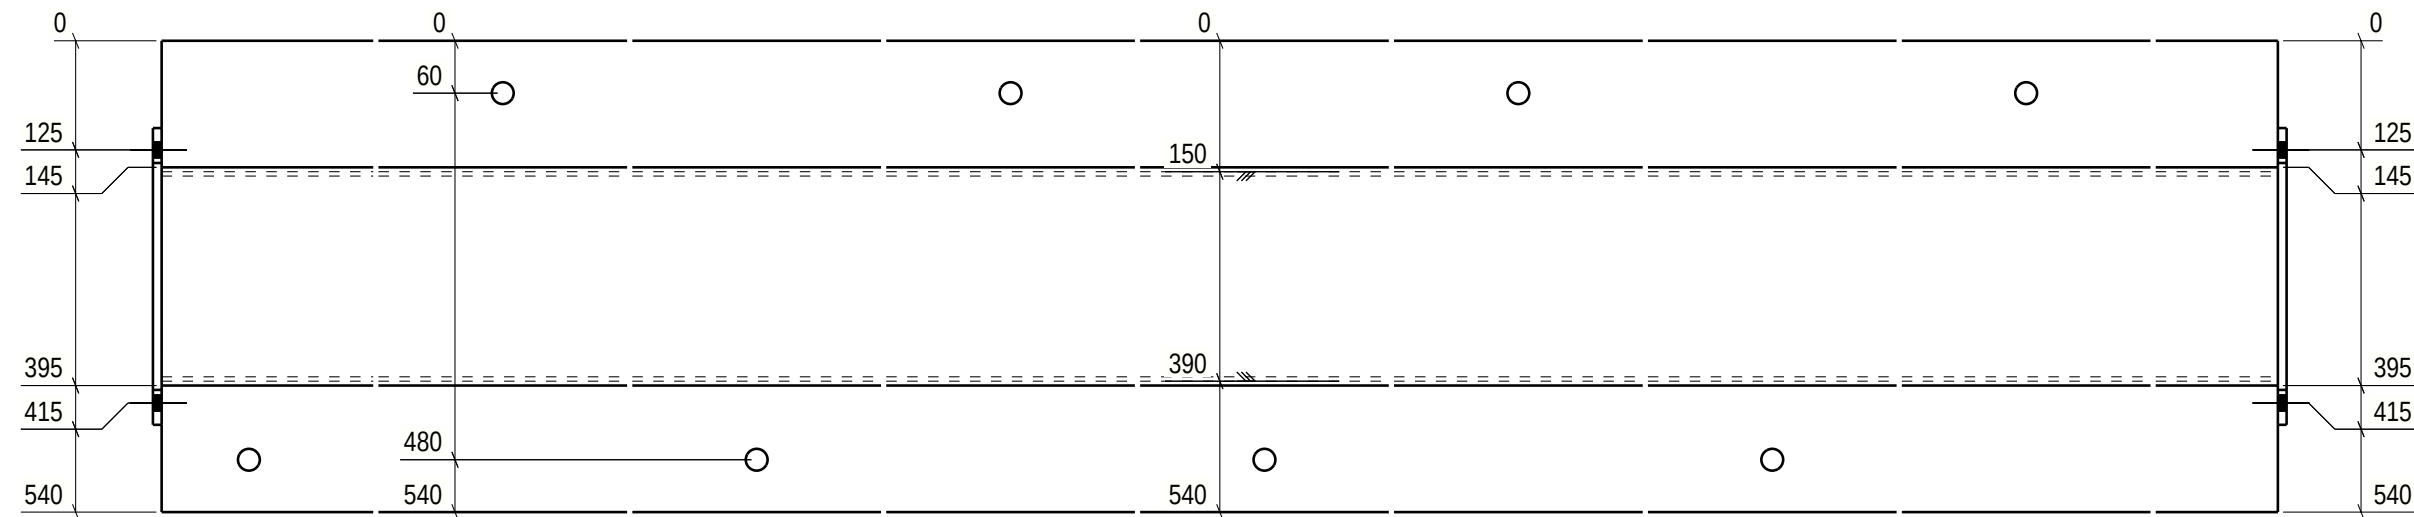


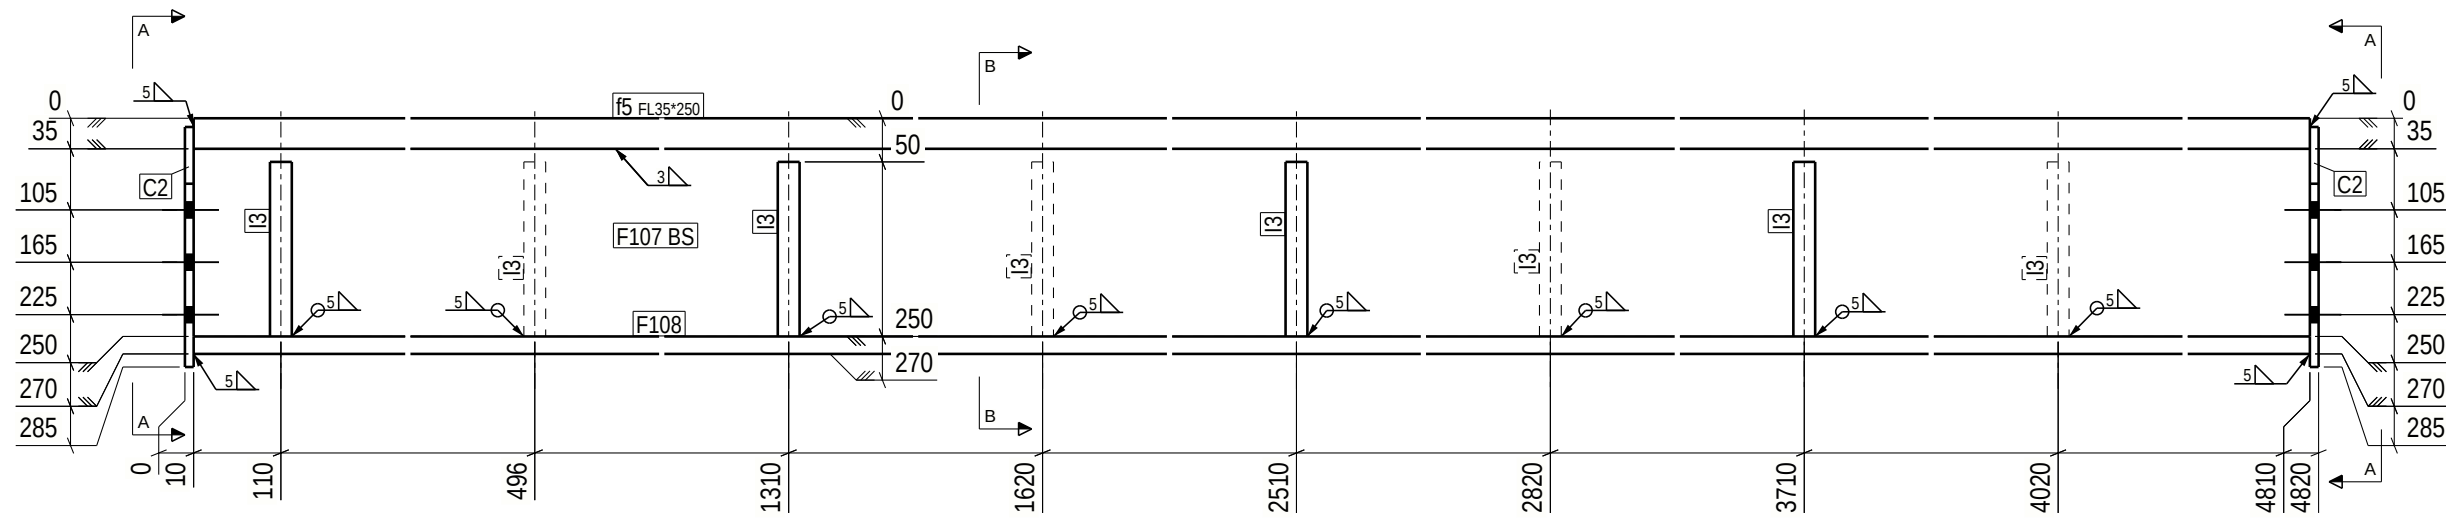

! NDT test:  
Part thickness >30mm  
f5

GENERAL NOTES: For your safety, check weight before handling:  
0-5kg Light 5-15kg Normal 15+kg Heavy

| MATERIAL LIST FOR ASSEMBLY MK'D f.5 |          |          |     |        |      | 1        | No. Required |
|-------------------------------------|----------|----------|-----|--------|------|----------|--------------|
| Mark                                | Profile  | Material | No. | Length | Area | Weight   |              |
| f5                                  | FL35*250 | S355J2   | 1   | 4800   | 2.8  | 329.7 !! |              |
| C2                                  | PL10*275 | S355J2   | 2   | 340    | 0.2  | 6.9      |              |
| F107                                | FL5*215  | S355J2   | 2   | 4800   | 2.1  | 40.5 !!  |              |
| F108                                | FL20*540 | S355J2   | 1   | 4800   | 5.4  | 406.9 !! |              |
| I3                                  | REBAR25  | B550B    | 8   | 200    | 0.0  | 0.7      |              |
| Total                               |          |          |     |        |      | 12.9     | 837.4        |

Finish Class  
Standard

|                         |                                |     |
|-------------------------|--------------------------------|-----|
| Surface treatment info: | Thickness/start point-> length | No. |
| Overall Painting        | Primerµm whole asse***         | 1   |

Special surface treatment weld a = 4

OPSVEJST EMNE

|                                                   |                                      |                  |                      |
|---------------------------------------------------|--------------------------------------|------------------|----------------------|
| * o 3 0 4 8 0 - 1 * DS Skalkonstruktion * A f 5 * |                                      |                  |                      |
| PROJECT                                           | Akkasæter Lager- og vedlikeholdshall | EXEC. CLASS      | EXC 2                |
| MEMBER                                            | HSQ                                  | QUANTITY:        | 1 PROJECT No 30480-1 |
| REVISION                                          | ISSUED: 07.11.2025                   | DRAFTER: ZLL SST | DRAWING No. f.5      |