



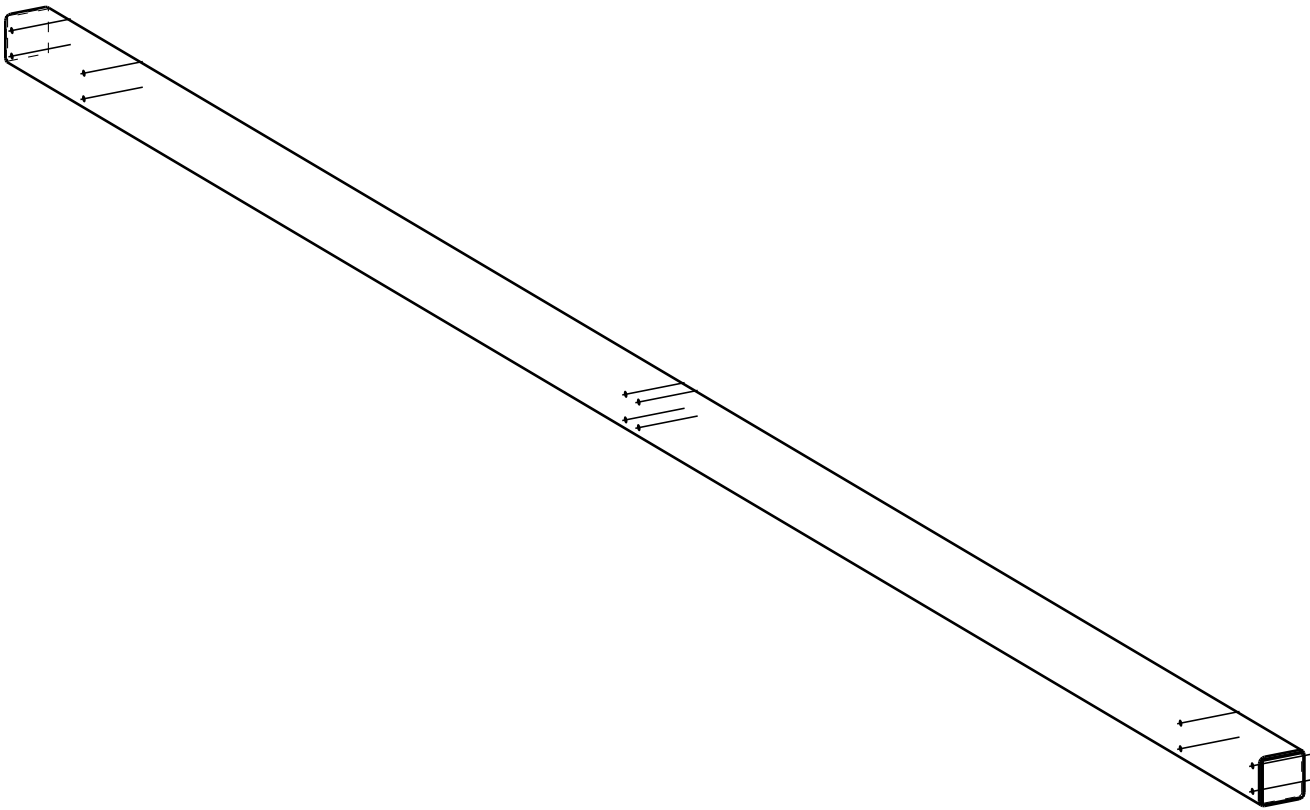

GENERAL NOTES:						
For your safety, check weight before handling:						
0-5kg Light 5-15kg Normal 15+kg Heavy						
ALL WELDS ARE 4 UNLESS NOTED ON DRAWING						
MATERIAL LIST FOR ASSEMBLY MK'D p.12						
4 No. Required						
Mark	Profile	Material	No.	Length	Area	Weight
p12	RHS100X100X6	S355J2H	1	4790	1.8	81.0 !!
F51	FL5*90	S355J2	2	90	0.0	0.3
Total				1.9	81.7	

Finish Class
Standard

Surface treatment info:	Thickness/start point-> length	No.
Overall Painting	C2M RAL7016µm whole***4	

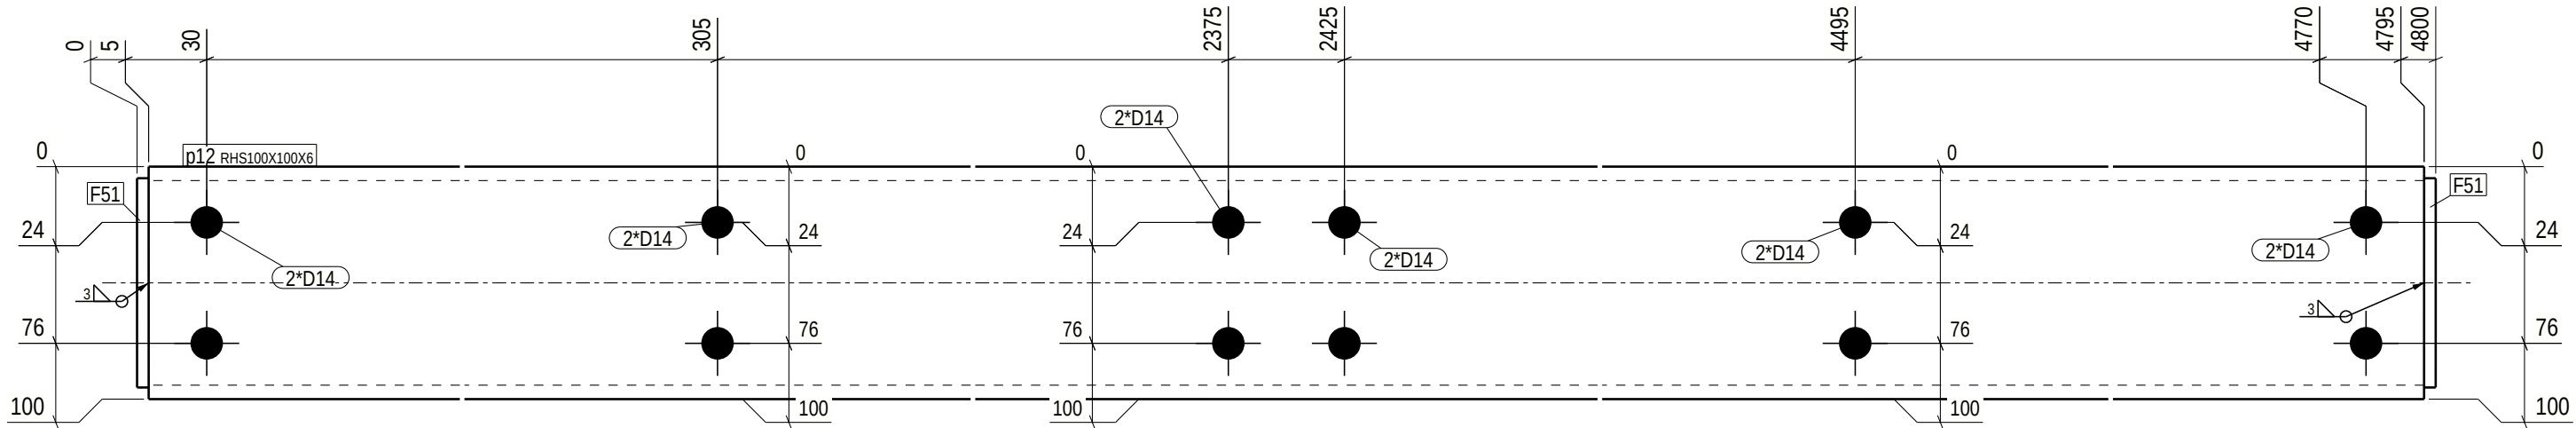

Special
surface treatment



weld a = 4

PHASE	QUANTITY
1	4

* o 3 0 4 8 0 - 1 *				 DS Stålkonstruktion		* A p 1 2 *	
PROJECT	Akkasæter Lager- og vedlikeholdshall				EXEC. CLASS		EXC 2
MEMBER	Portomfatning		QUANTITY: 4		PROJECT No		30480-1
REVISION		ISSUED: 07.11.2025	DRAFTER: ZLL BIM control: SST		DRAWING No.		p.12