
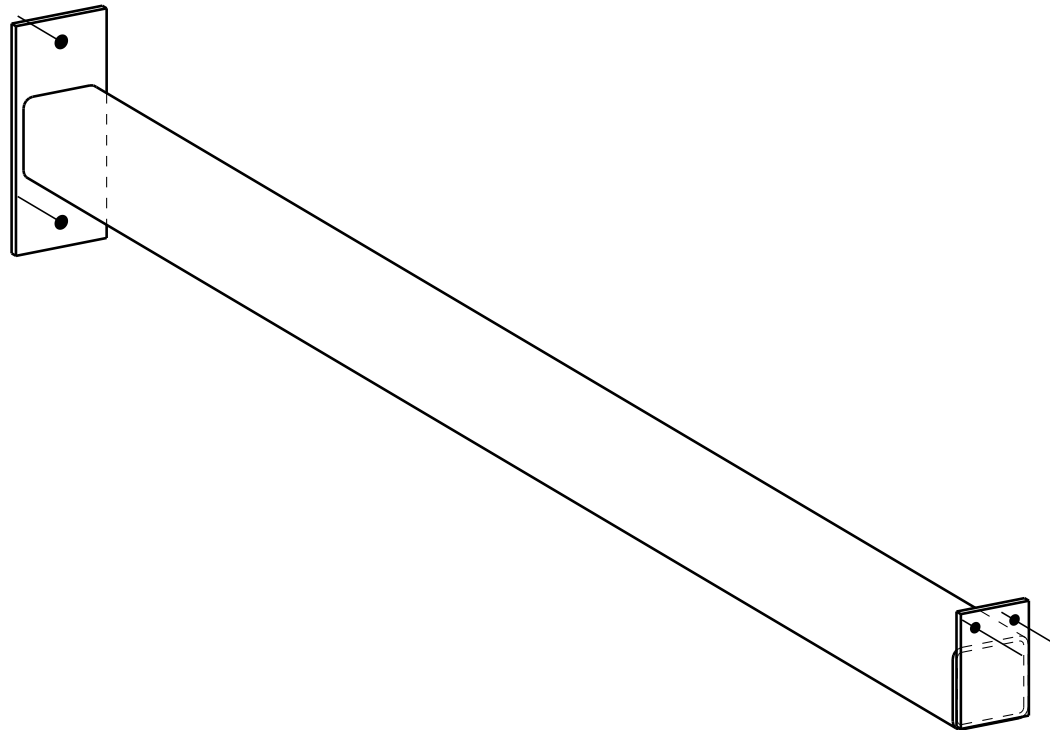
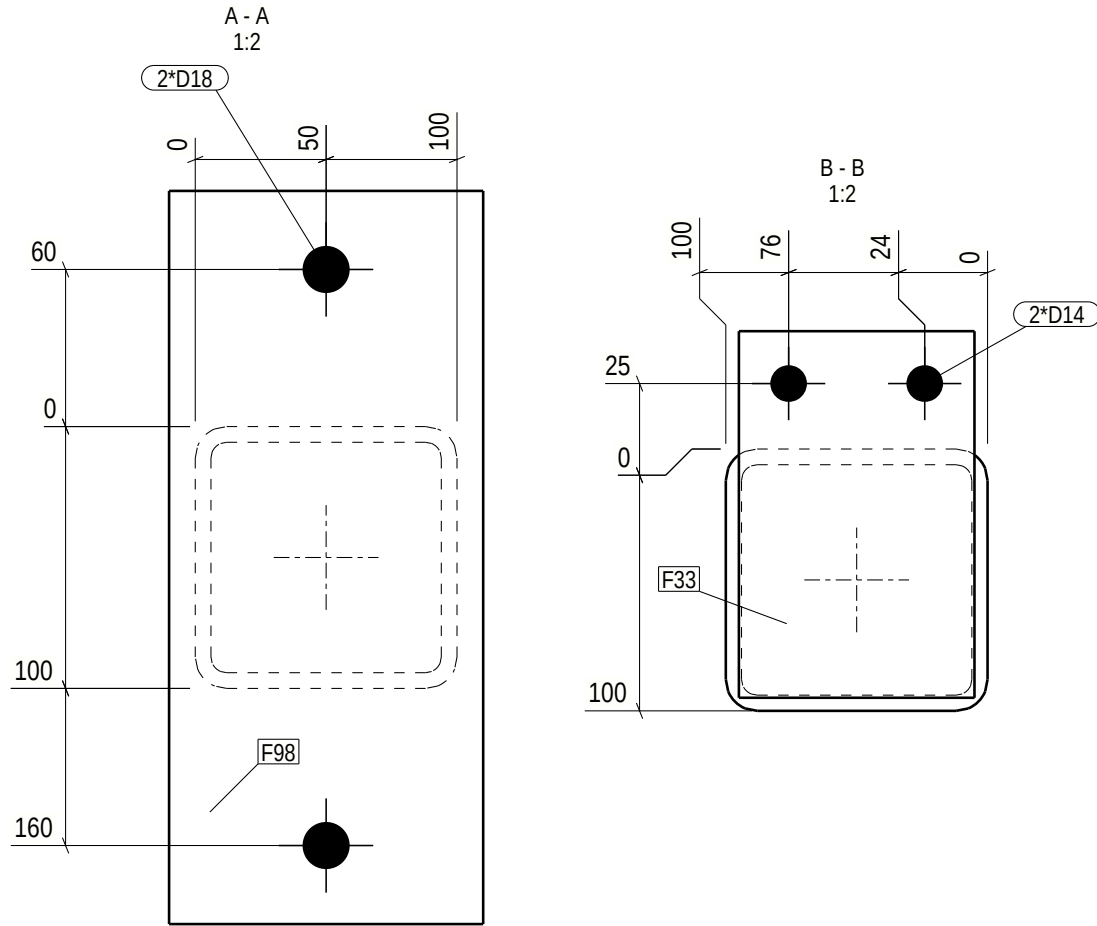


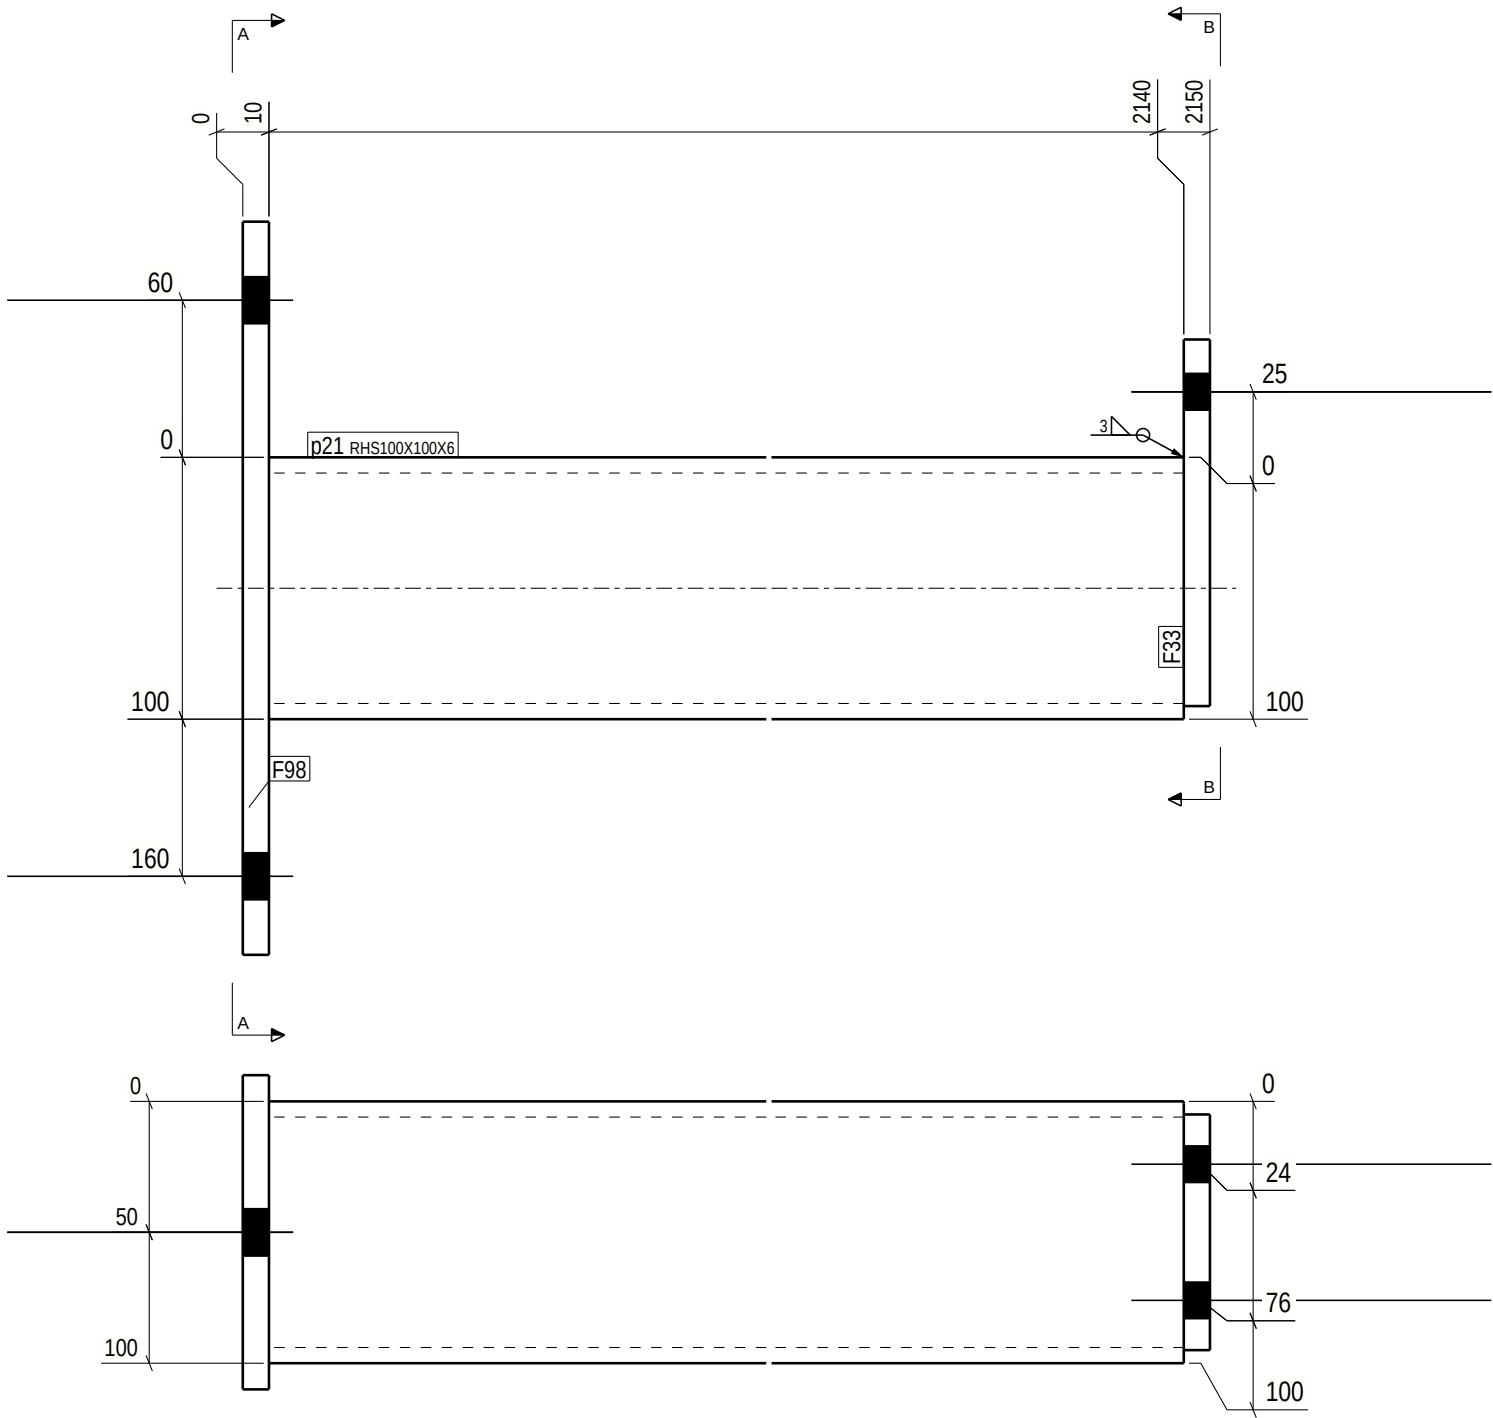

GENERAL NOTES: For your safety, check weight before handling:

ALL WELDS ARE 4 UNLESS NOTED ON DRAWING

MATERIAL LIST FOR ASSEMBLY MK'D p.21 5 No. Required

Mark	Profile	Material	No.	Length	Area	Weight
p21	RHS100X100X6	S355J2H	1	2130	0.8	36.0 !!
F33	FL10*90	S355J2	1	140	0.0	1.0
F98	FL10*120	S355J2	1	280	0.1	2.6
Total					0.9	39.7

Finish Class
Standard

Surface treatment info:

Overall Painting

Thickness/start point--> length	No.
Primerµm whole asse***	5



Special
surface treatment



weld a = 4

PHASE	QUANTITY
1	5

* o 3 0 4 8 0 - 1 * DS Steelkonstruktion * A p 2 1 *			
PROJECT	Akkasæter Lager- og vedlikeholdshall	EXEC. CLASS	EXC 2
MEMBER	Portomfatning	QUANTITY:	5
REVISION	ISSUED: 07.11.2025	DRAFTER: ZLL	PROJECT No 30480-1
		BIM control: SST	DRAWING No. p.21