


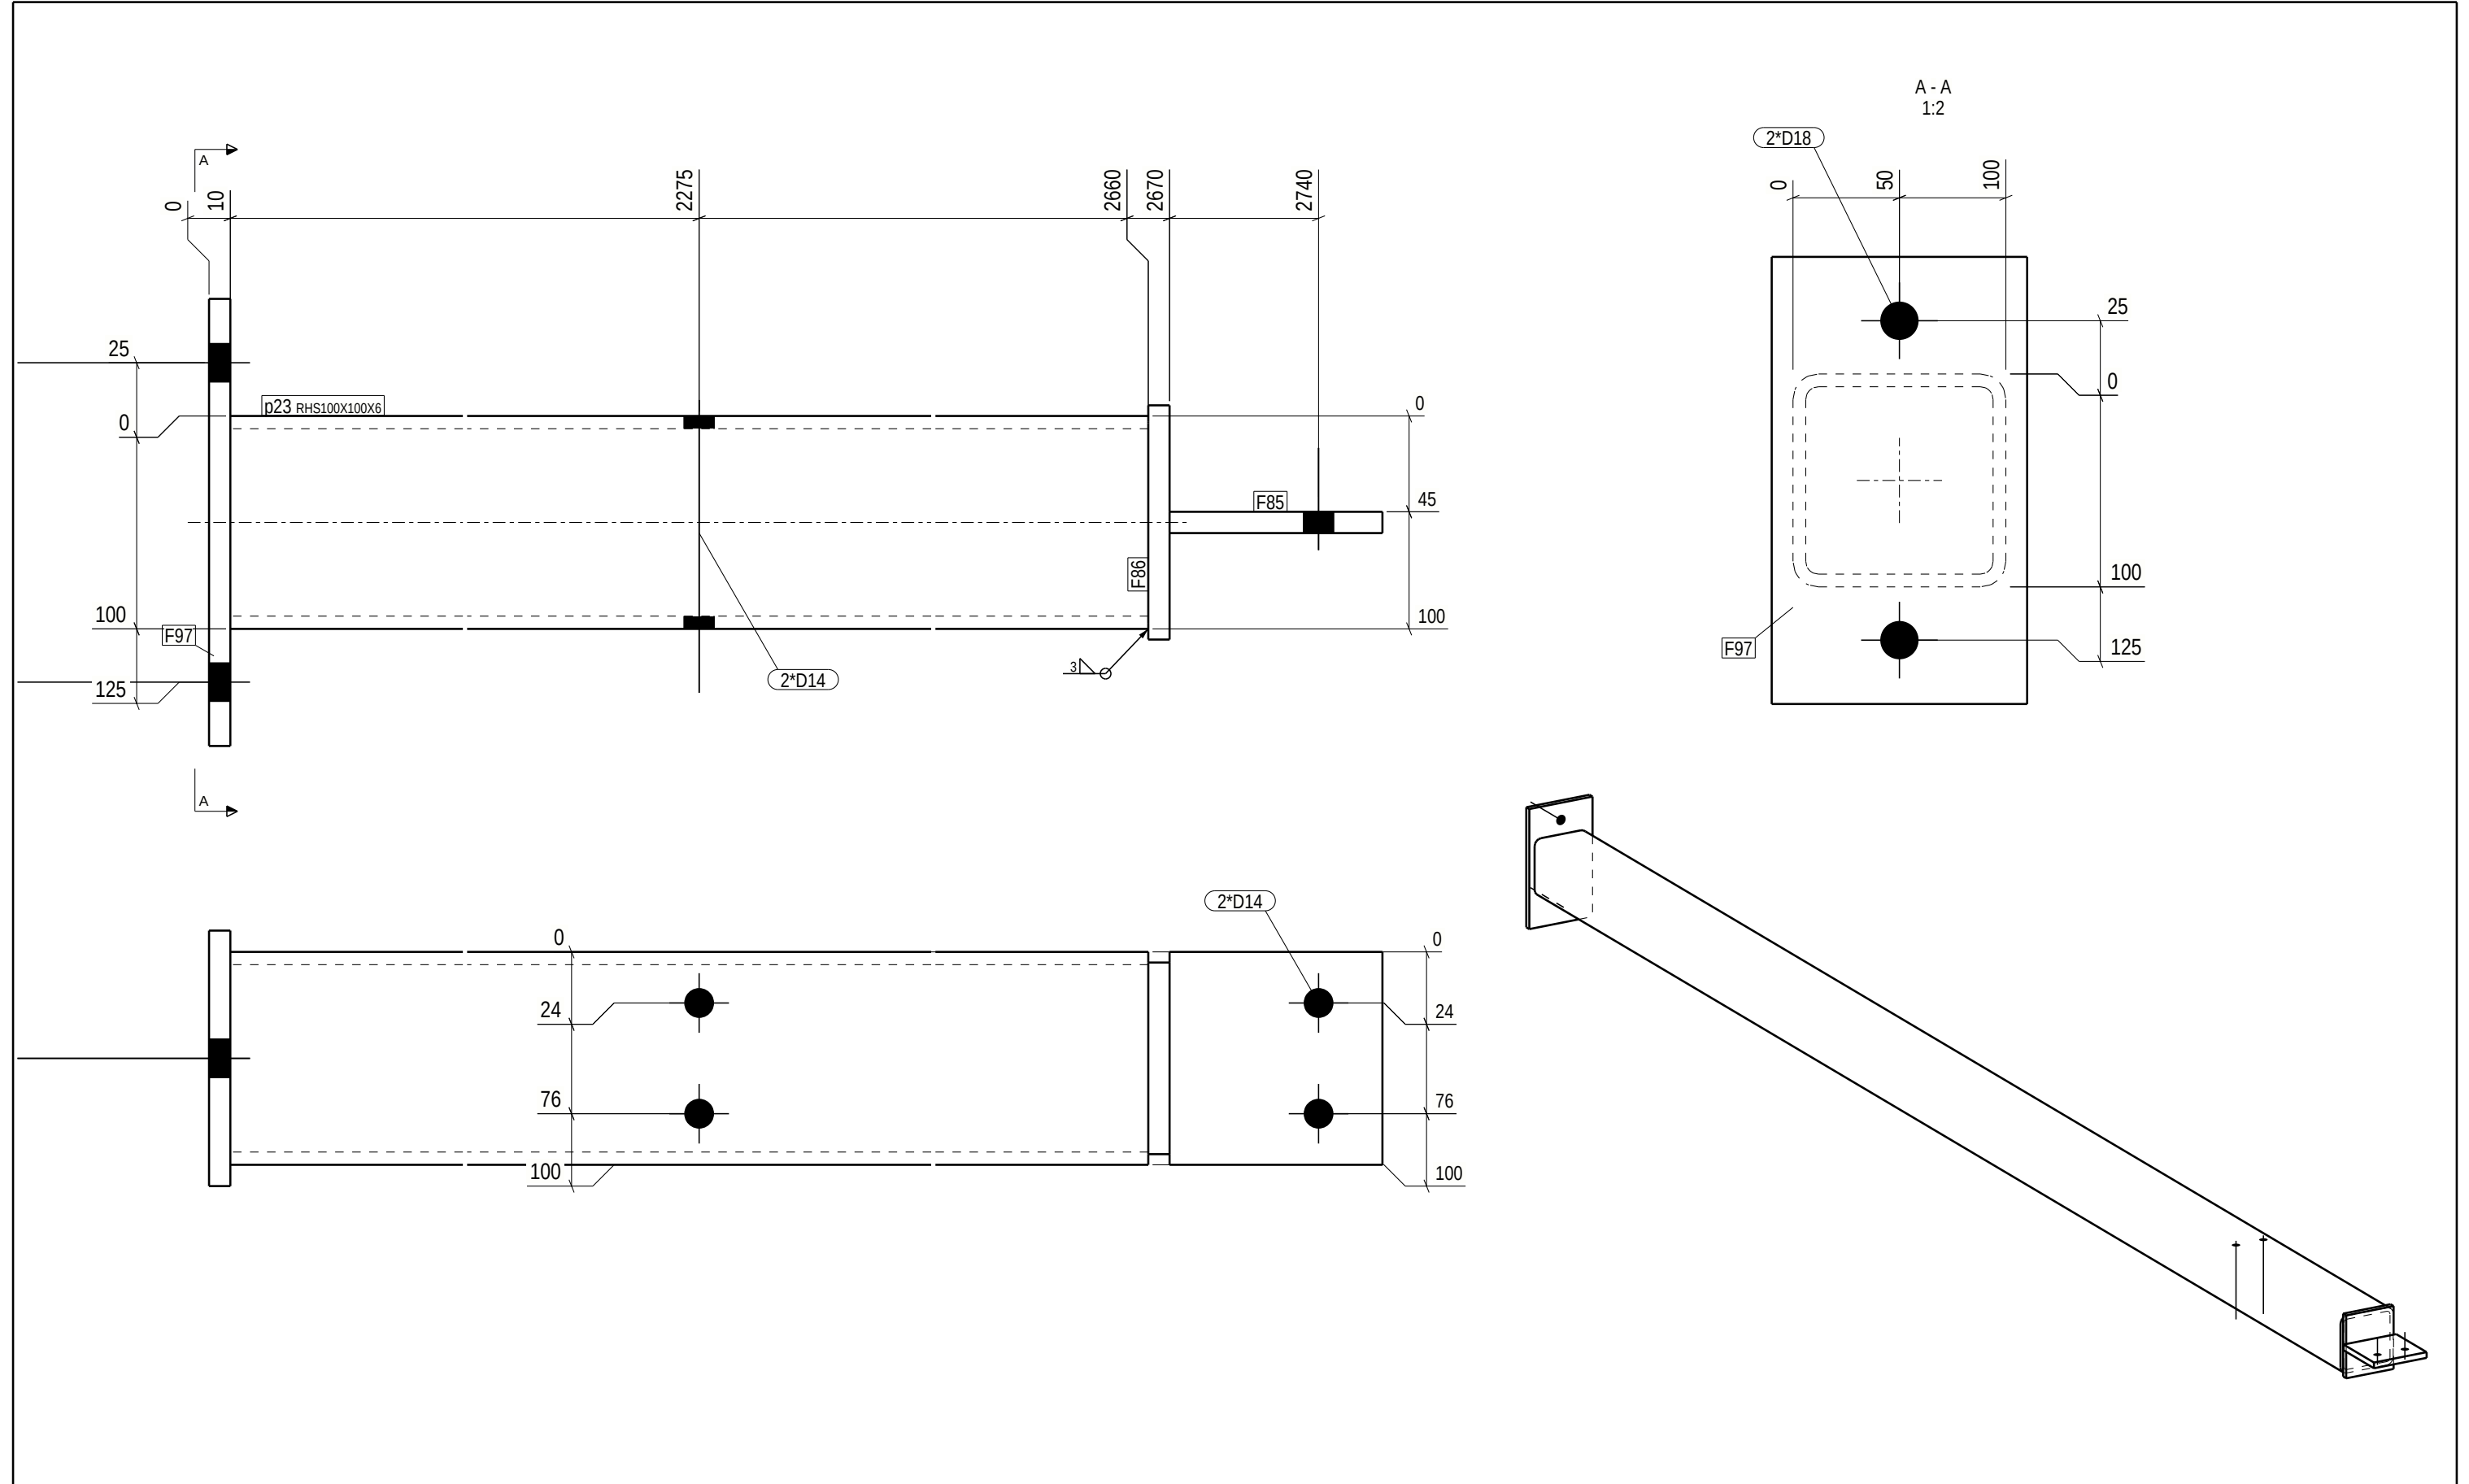

GENERAL NOTES: For your safety, check weight before handling:
ALL WELDS ARE 4 UNLESS NOTED ON DRAWING

MATERIAL LIST FOR ASSEMBLY MK'D p.23						
Mark	Profile	Material	No.	Length	Area	Weight
p23	RHS100X100X6	S355J2H	1	2650	1.0	44.8 !!
F85	FL10*100	S355J2	1	100	0.0	0.8
F86	FL10*90	S355J2	1	110	0.0	0.8
F97	FL10*120	S355J2	1	210	0.1	2.0
Total					1.1	48.4

Finish Class
Standard

Surface treatment info:	Thickness/start point-> length	No.
Overall Painting	C2M RAL7016µm whole	**1

Special surface treatment

weld a = 4

PHASE	QUANTITY
1	1

* o 3 0 4 8 0 - 1 * DS Steelkonstruktion * A p 2 3 *			
PROJECT	Akkasæter Lager- og vedlikeholdshall	EXEC. CLASS	EXC 2
MEMBER	Portomfatning	QUANTITY:	1
REVISION	ISSUED: 07.11.2025	DRAFTER: ZLL	PROJECT No. 30480-1
		BIM control: SST	DRAWING No. p.23