
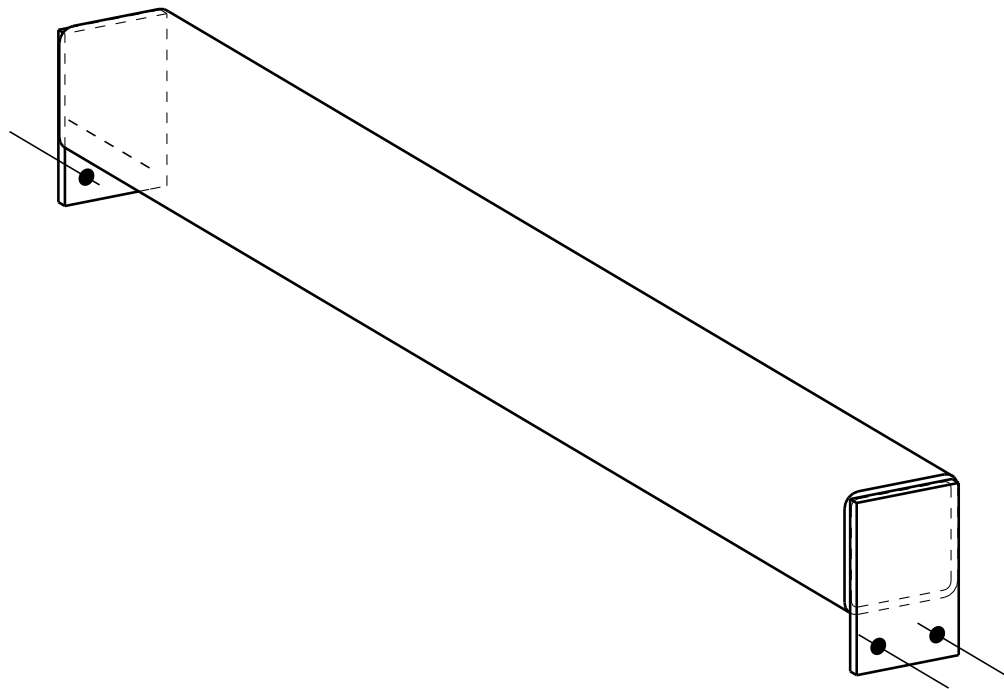
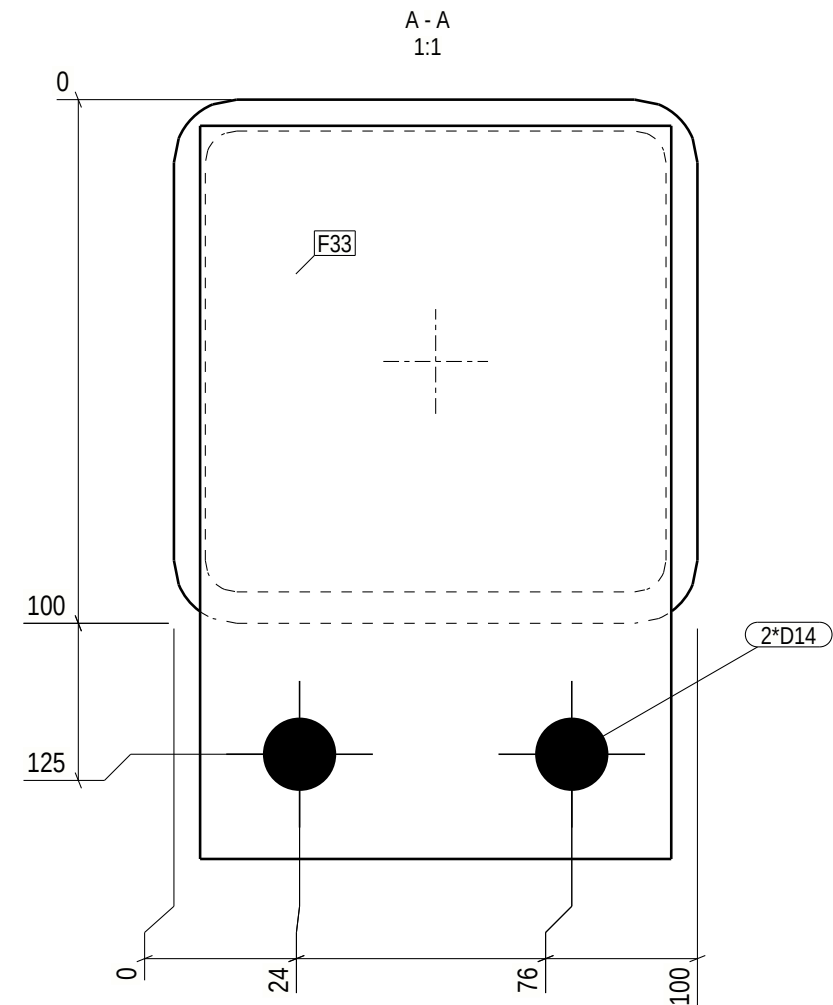


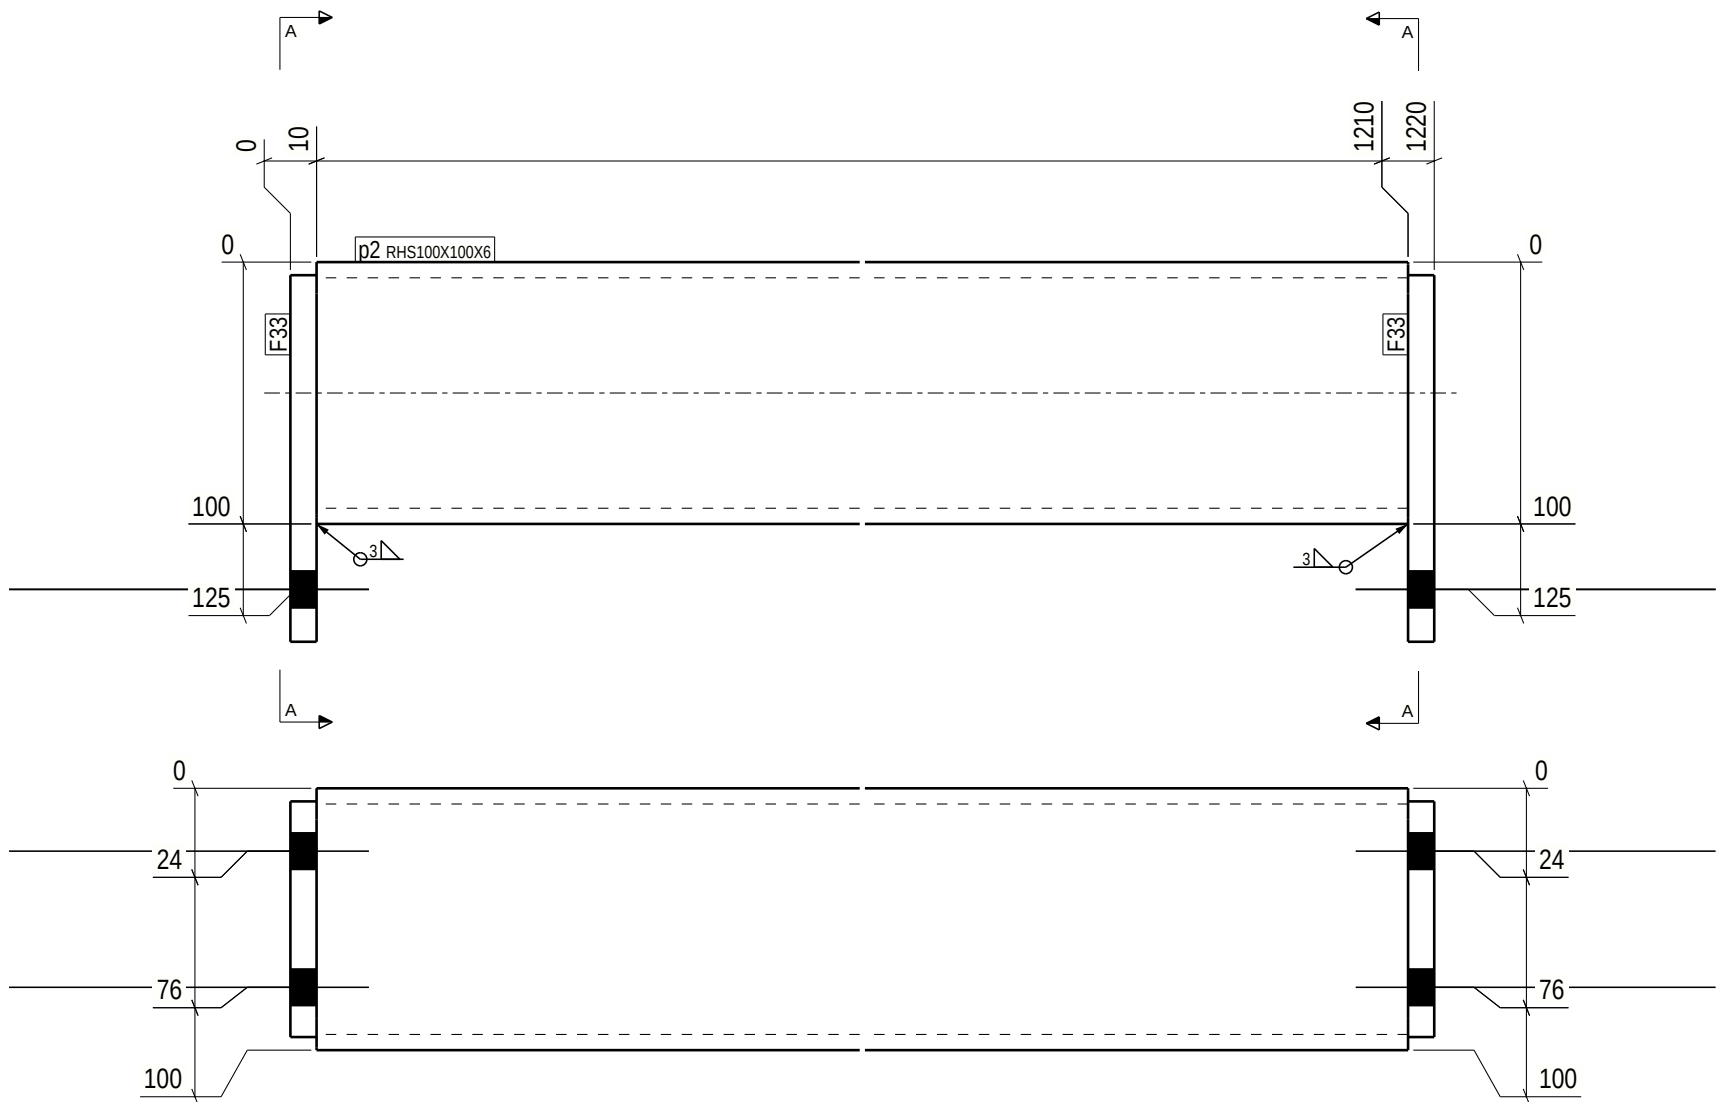

GENERAL NOTES: For your safety, check weight before handling:
0-5kg Light 5-15kg Normal 15+kg Heavy

ALL WELDS ARE 4 UNLESS NOTED ON DRAWING

MATERIAL LIST FOR ASSEMBLY MK'D p.2						
24 No. Required						
Mark	Profile	Material	No.	Length	Area	Weight
p2	RHS100X100X6	S355J2H	1	1200	0.5	20.3 !!
F33	FL10*90	S355J2	2	140	0.0	1.0
Total					0.5	22.3

Finish Class
Standard

Surface treatment info:	Thickness/start point-> length	No.
Overall Painting	C2M RAL7016µm whole	24



Special
surface treatment



weld a = 4

PHASE	QUANTITY
1	24

* o 3 0 4 8 0 - 1 * DS Steelkonstruktion * A p 2 *			
PROJECT	Akkasæter Lager- og vedlikeholdshall		EXEC. CLASS
MEMBER	Portomfatning	QUANTITY: 24	PROJECT No
REVISION	ISSUED: 07.11.2025	DRAFTER: ZLL	DRAWING No.
		BIM control: SST	
			30480-1
			p.2