


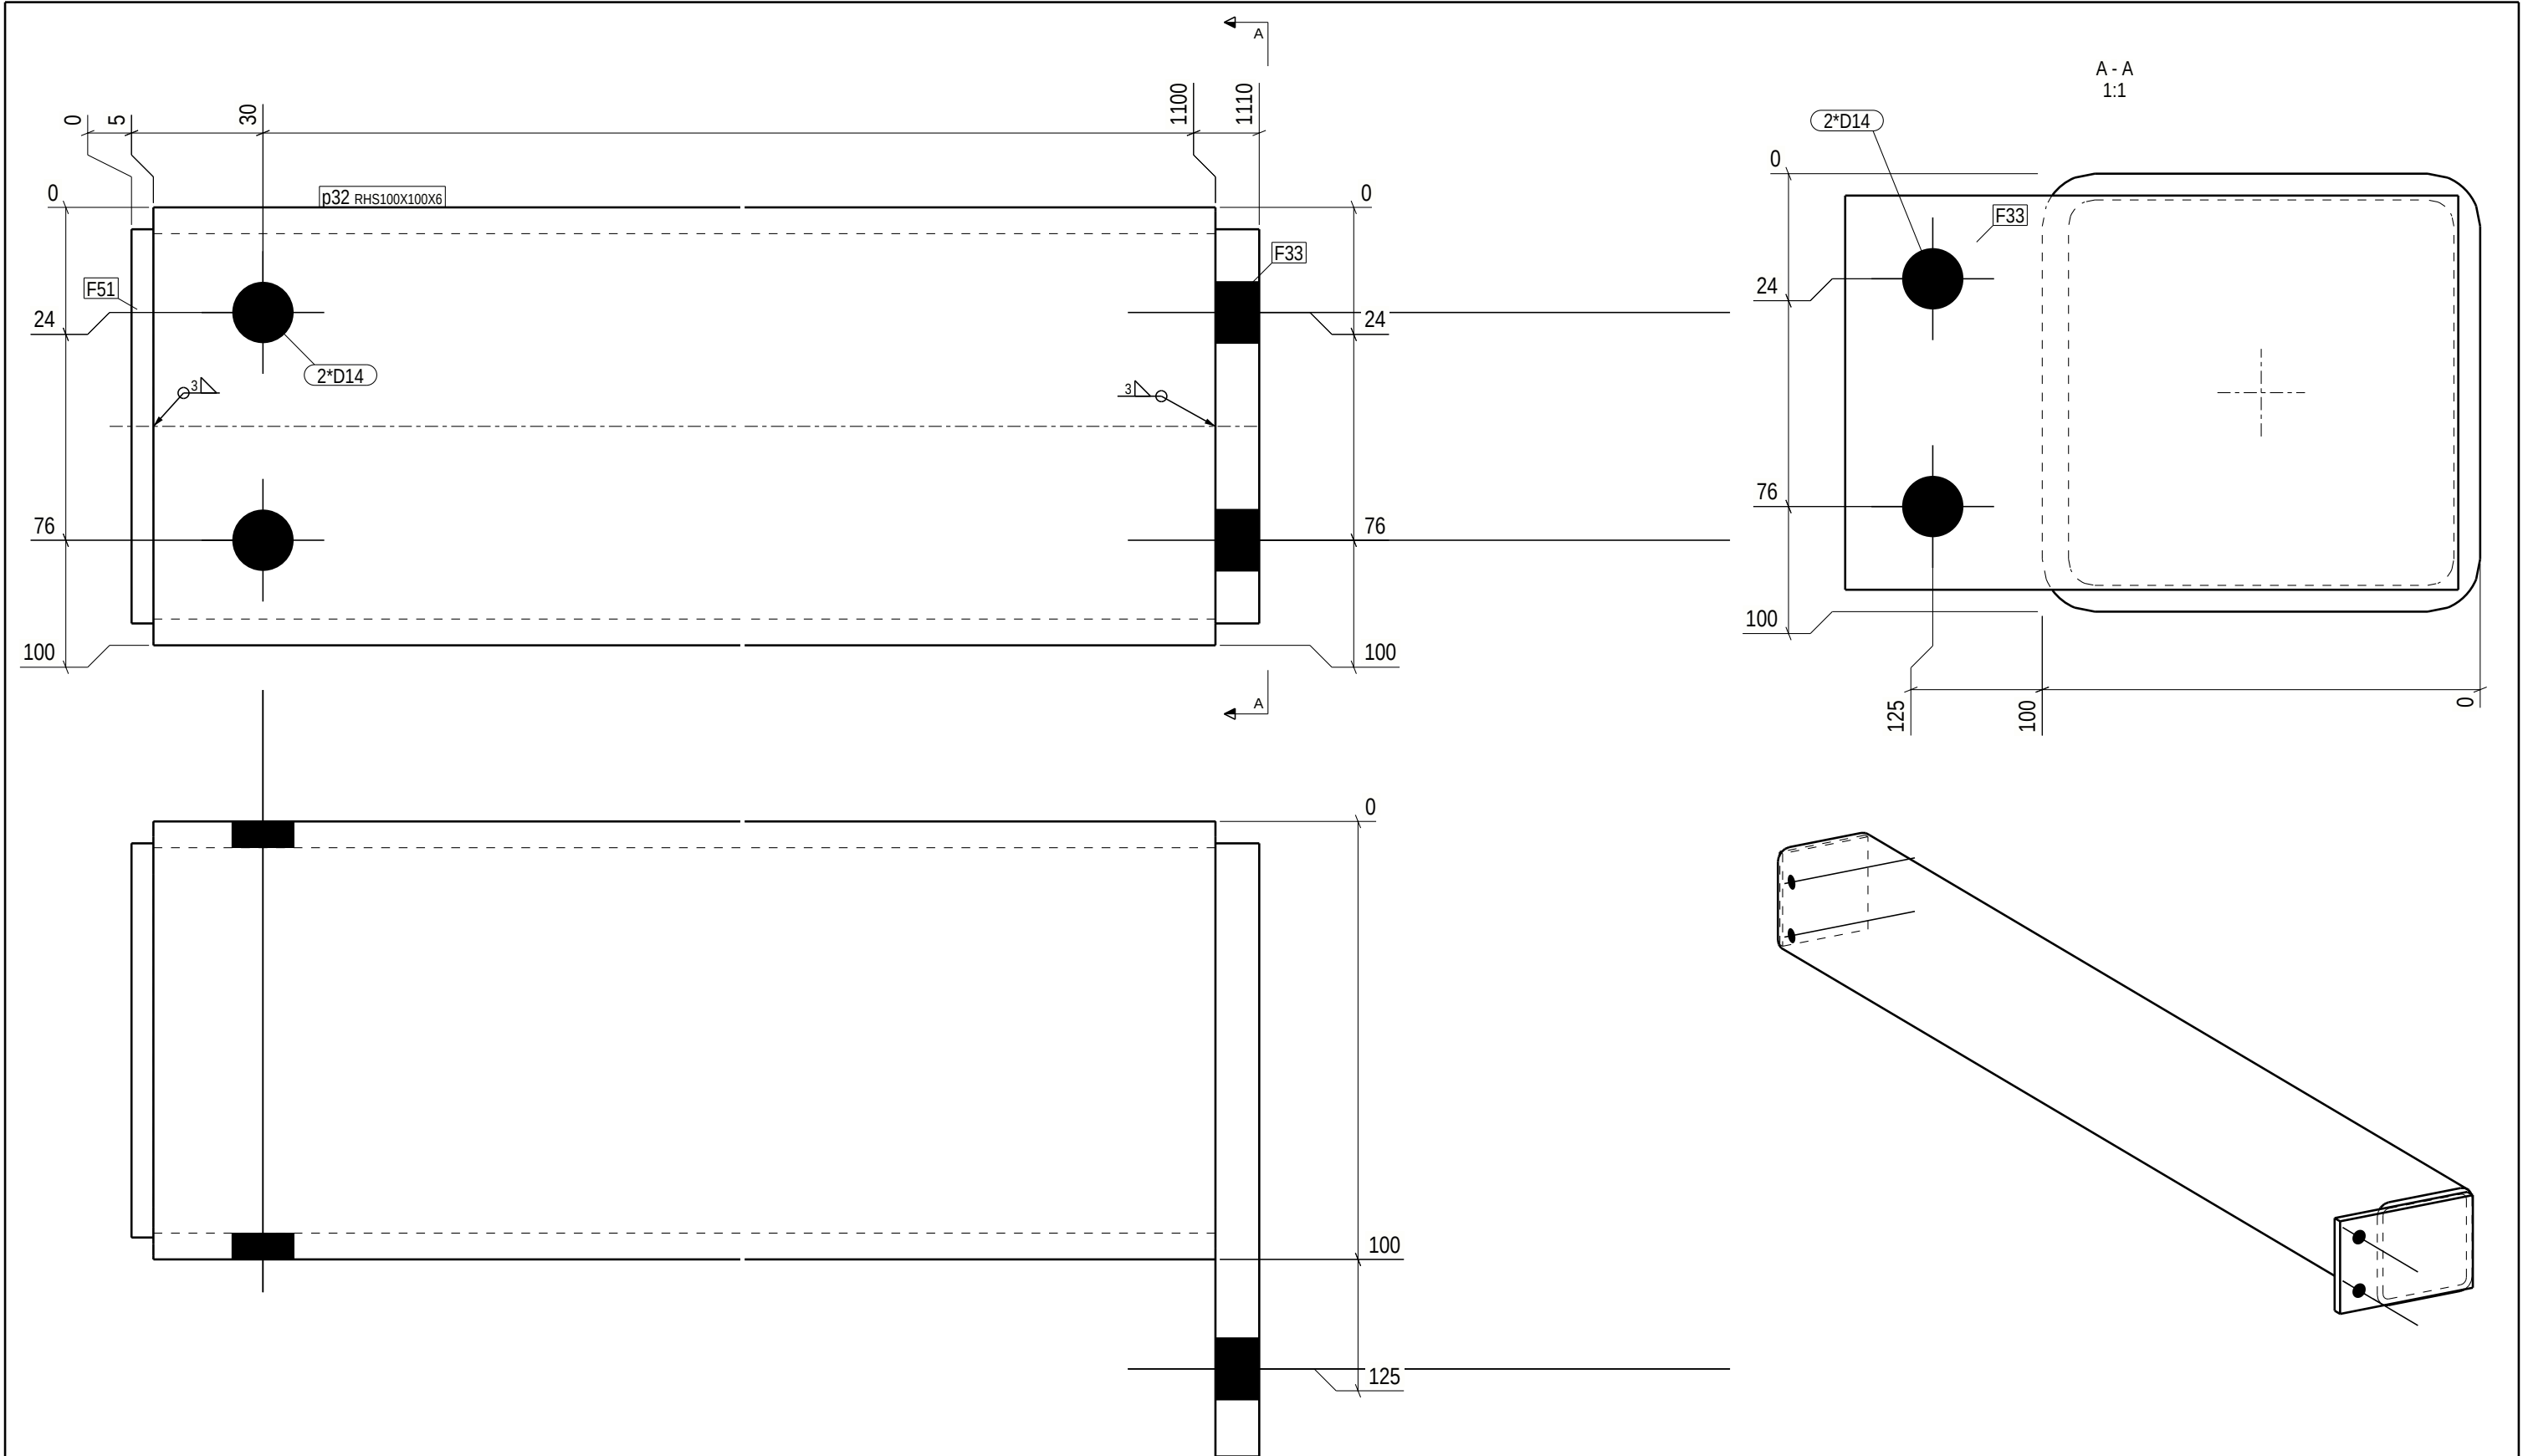

GENERAL NOTES: For your safety, check weight before handling:

ALL WELDS ARE 4 UNLESS NOTED ON DRAWING

MATERIAL LIST FOR ASSEMBLY MK'D **p.32** **1** No. Required

Mark	Profile	Material	No.	Length	Area	Weight
p32	RHS100X100X6	S355J2H	1	1095	0.4	18.5 !!
F33	FL10*90	S355J2	1	140	0.0	1.0
F51	FL5*90	S355J2	1	90	0.0	0.3
Total					0.5	19.8

Finish Class
Standard

Surface treatment info:	Thickness/start point-> length	No.
Overall Painting	C2M RAL7016µm whole	**1

Special surface treatment weld a = 4

PHASE	QUANTITY
1	1

* o 3 0 4 8 0 - 1 * DS Stahlkonstruktion * A p 3 2 *			
PROJECT	Akkasæter Lager- og vedlikeholdshall	EXEC. CLASS	EXC 2
MEMBER	Portomfatning	QUANTITY:	1
REVISION	ISSUED: 07.11.2025	DRAFTER: ZLL	PROJECT No 30480-1
		BIM control: SST	DRAWING No. p.32