
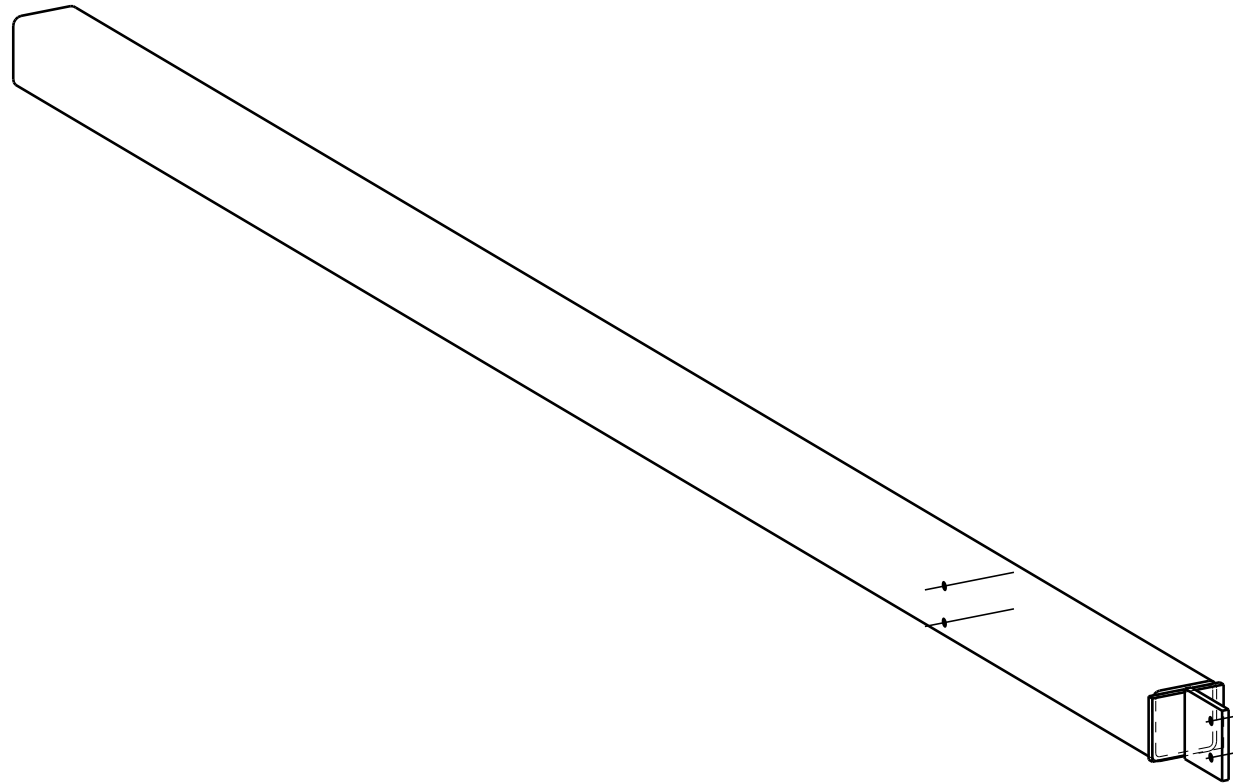


Tekla Structures

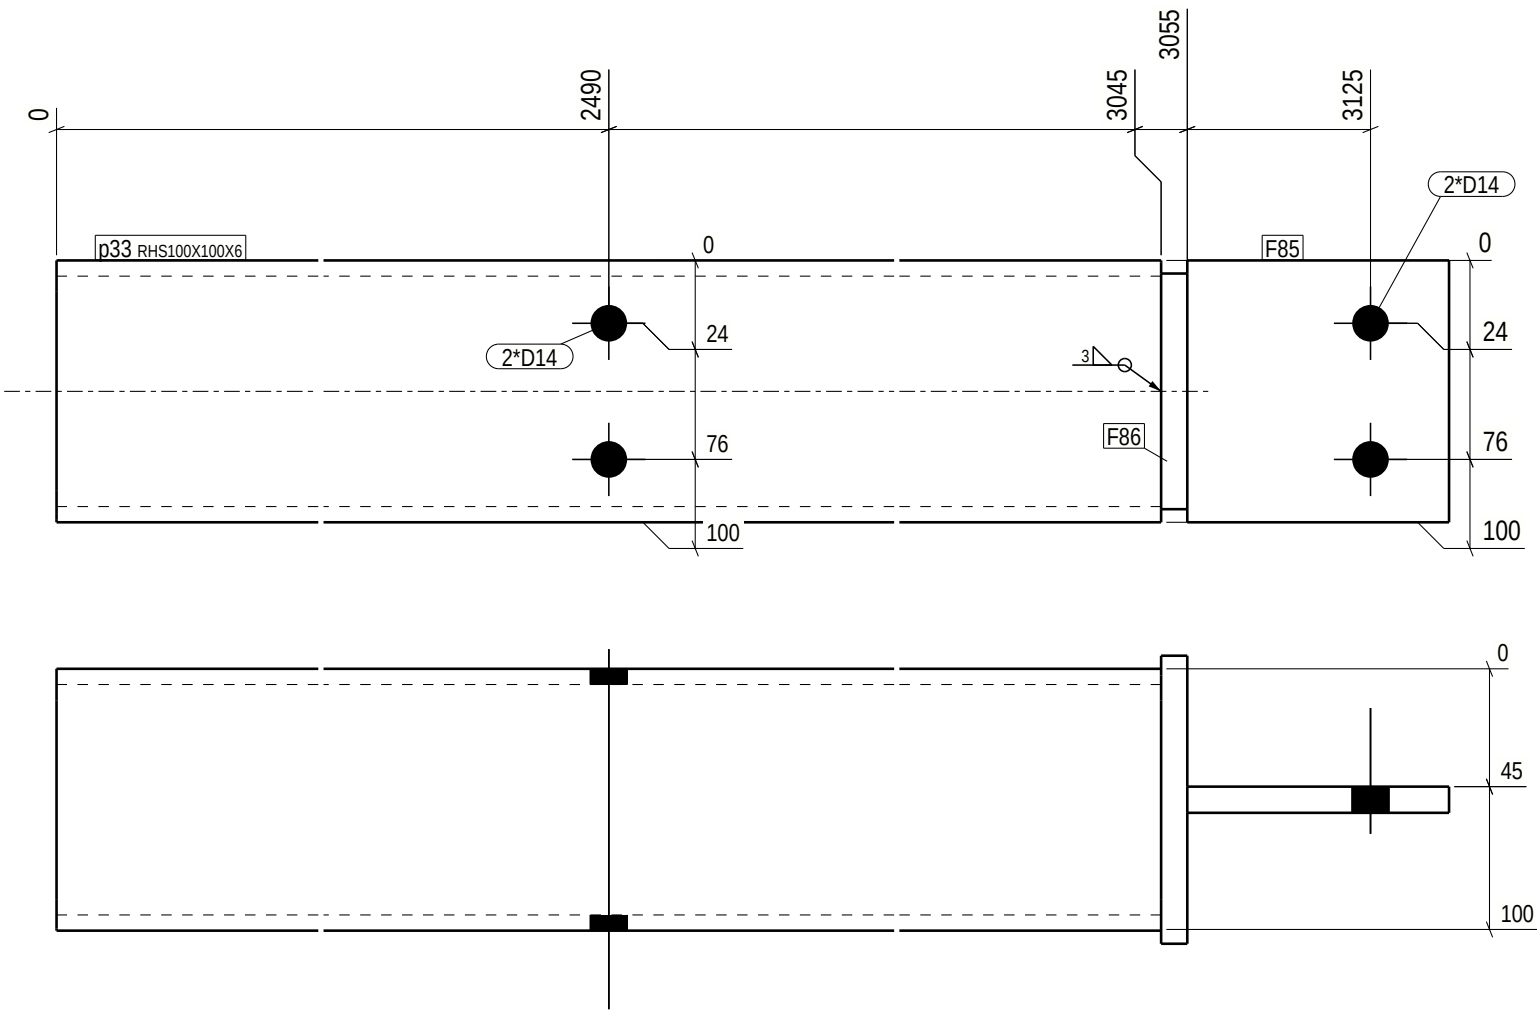

GENERAL NOTES:						
For your safety, check weight before handling:						
0-5kg Light 5-15kg Normal 15+kg Heavy						
ALL WELDS ARE 4 UNLESS NOTED ON DRAWING						
MATERIAL LIST FOR ASSEMBLY MK'D p.33 1 No. Required						
Mark	Profile	Material	No.	Length	Area	Weight
p33	RHS100X100X6	S355J2H	1	3045	1.2	51.5 !!
F85	FL10*100	S355J2	1	100	0.0	0.8
F86	FL10*90	S355J2	1	110	0.0	0.8
Total				1.2	53.1	

Finish Class
Standard

Surface treatment info:	Thickness/start point-> length	No.
Overall Painting	C2M RAL7016µm whole	**1



Special
surface treatment



weld a = 4

PHASE	QUANTITY
1	1

* o 3 0 4 8 0 - 1 * DS Steelkonstruktion * A p 3 3 *			
PROJECT	Akkasæter Lager- og vedlikeholdshall	EXEC. CLASS	EXC 2
MEMBER	Portomfatning	QUANTITY:	1
REVISION	ISSUED: 07.11.2025	DRAFTER: ZLL	PROJECT No 30480-1
		BIM control: SST	DRAWING No. p.33