
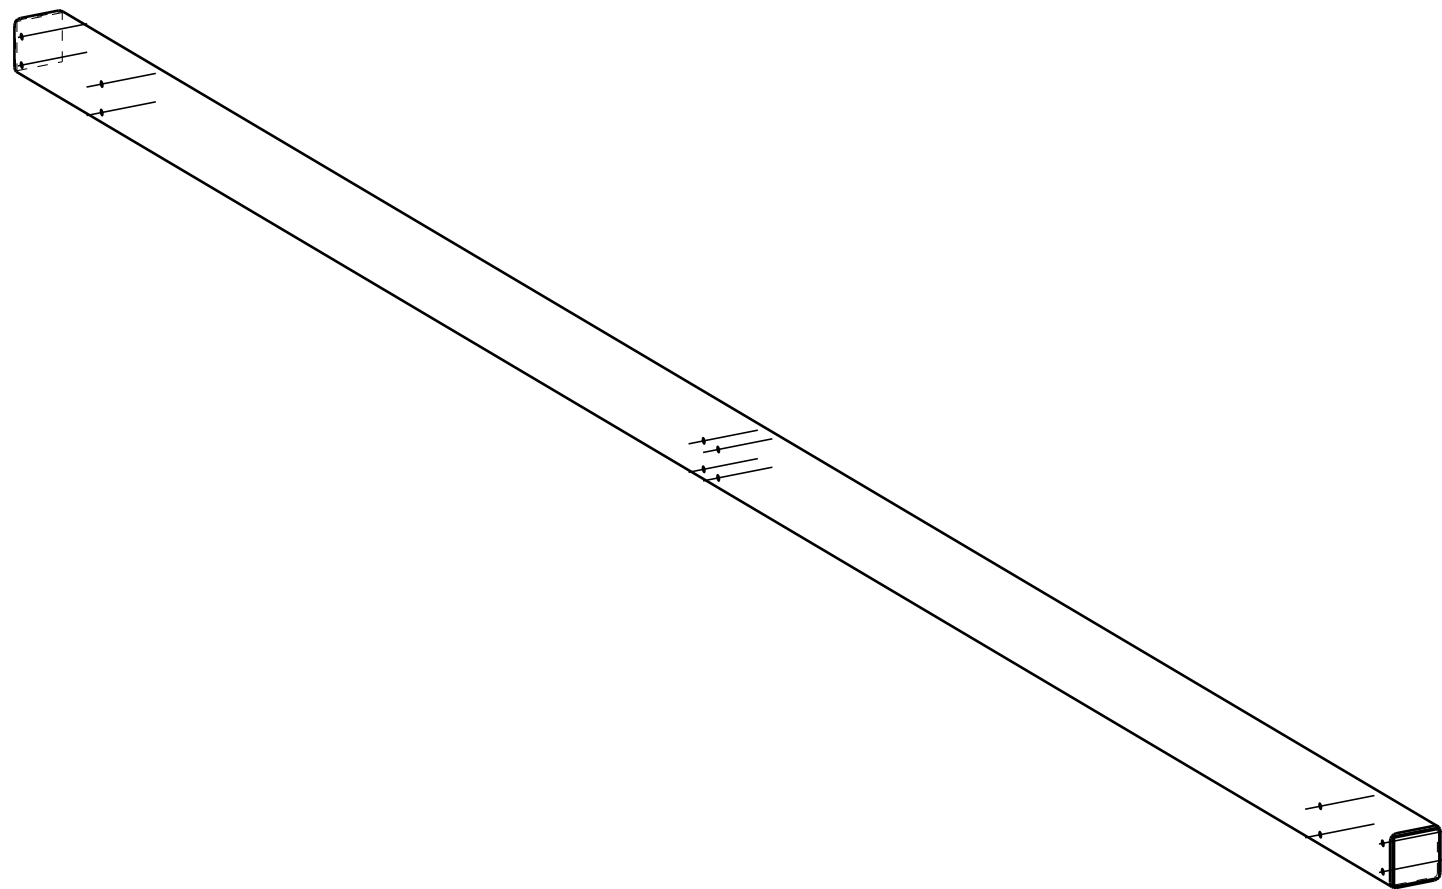


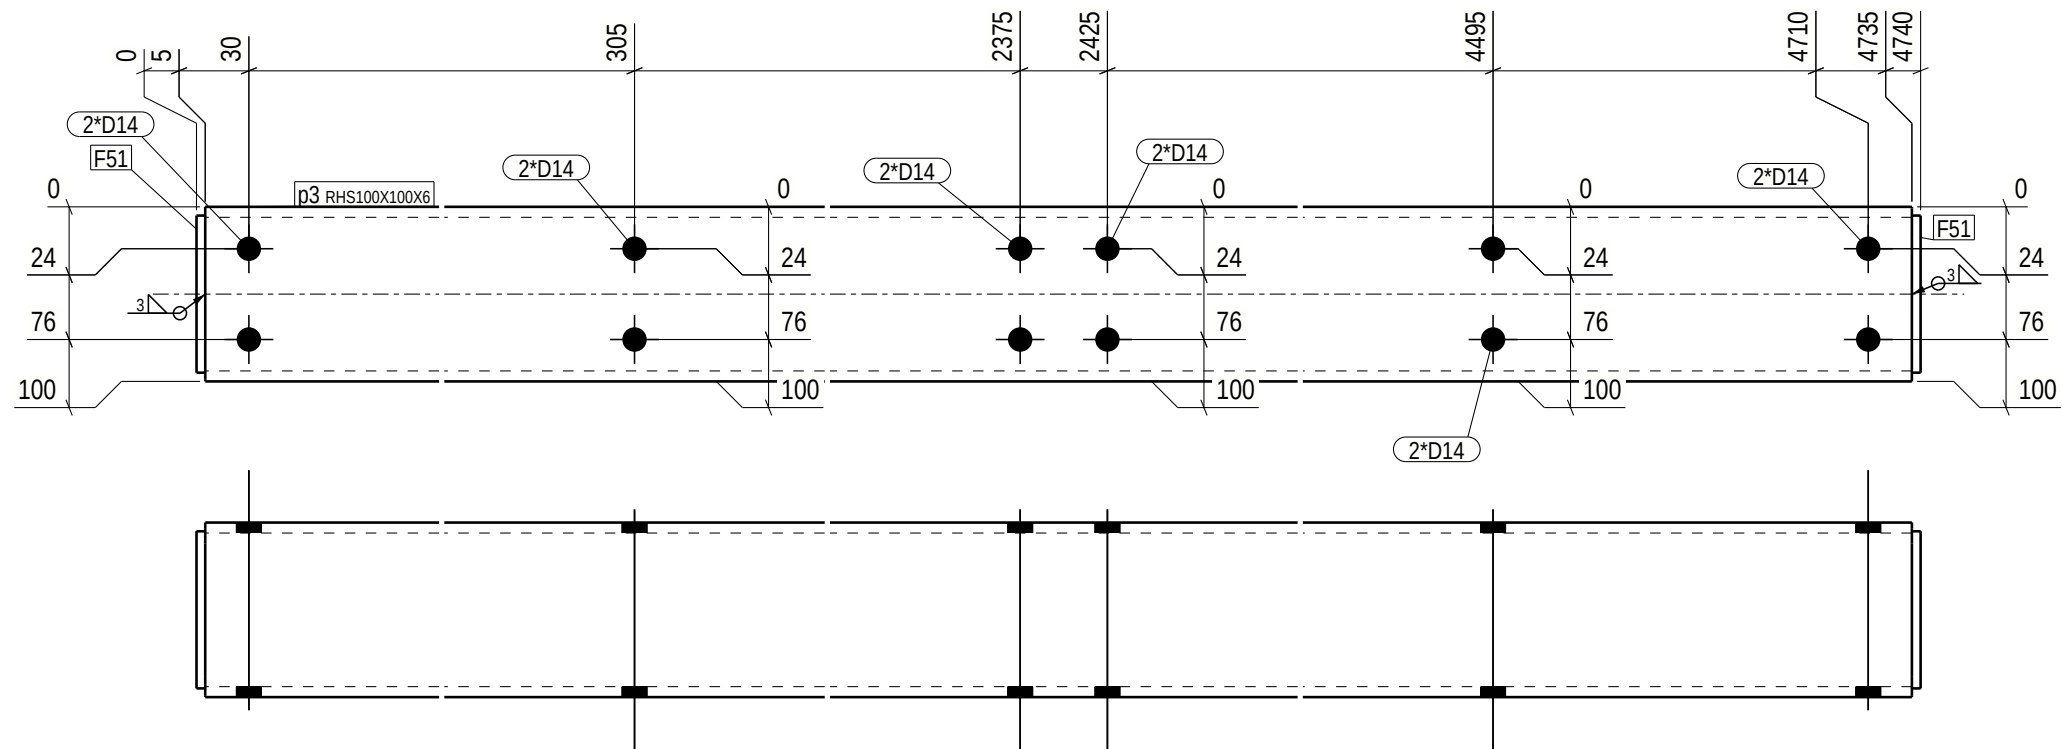

GENERAL NOTES: For your safety, check weight before handling:
0-5kg Light 5-15kg Normal 15+kg Heavy

ALL WELDS ARE 4 UNLESS NOTED ON DRAWING

MATERIAL LIST FOR ASSEMBLY MK'D p.3						
Mark	Profile	Material	No.	Length	Area	Weight
p3	RHS100X100X6	S355J2H	1	4730	1.8	80.0 !!
F51	FL5*90	S355J2	2	90	0.0	0.3
Total				1.9	80.6	

Finish Class
Standard

Surface treatment info:	Thickness/start point--> length	No.
Overall Painting	C2M RAL7016µm whole***4	



Special
surface treatment



weld a = 4

PHASE	QUANTITY
1	4

* o 3 0 4 8 0 - 1 *  DS <i>Stålkonstruktion</i> * A p 3 *			
PROJECT	Akkasæter Lager- og vedlikeholdshall	EXEC. CLASS	EXC 2
MEMBER	Portomfatning	QUANTITY:	4
REVISION	ISSUED: 07.11.2025	DRAFTER: ZLL	PROJECT No. 30480-1
		BIM control: SST	DRAWING No. p.3