

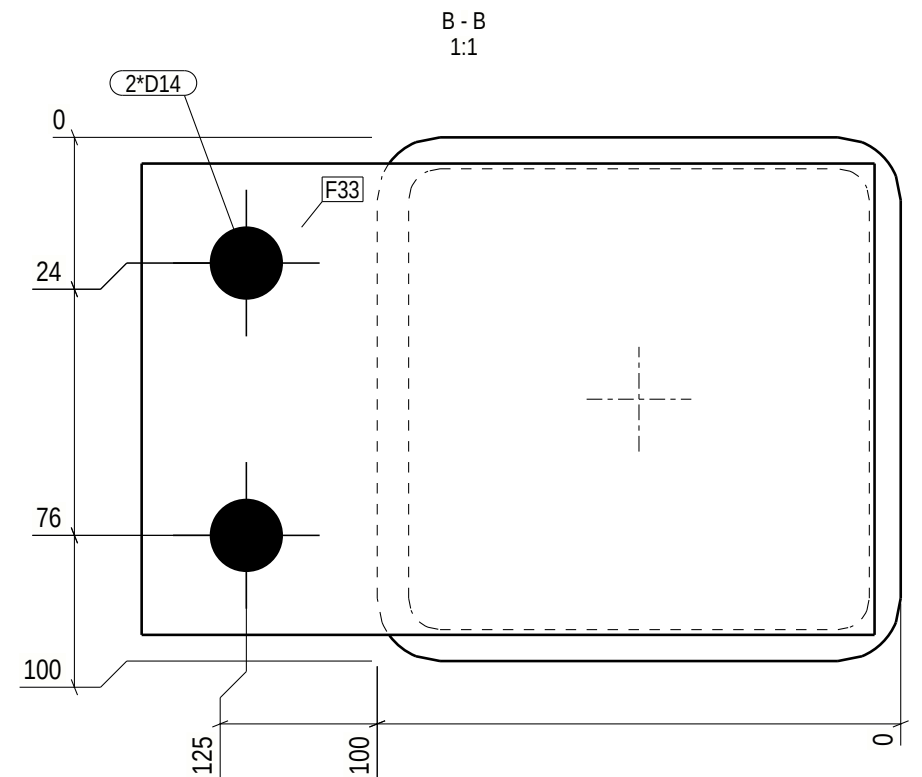


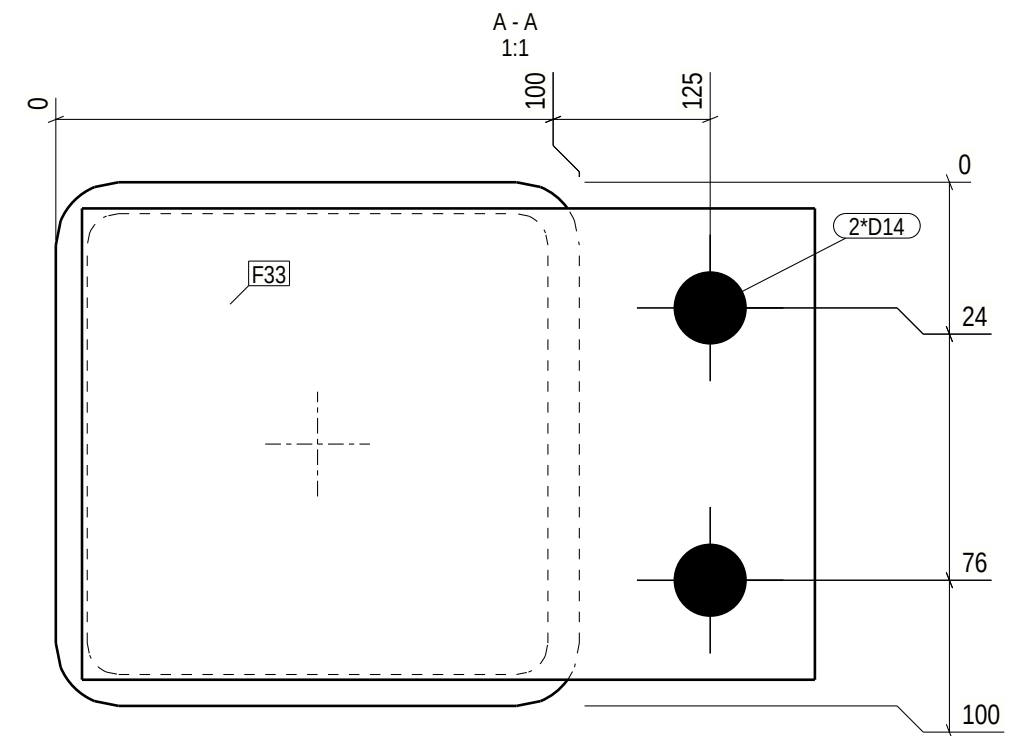

GENERAL NOTES:						
For your safety, check weight before handling:						
0-5kg Light 5-15kg Normal 15+kg Heavy						
ALL WELDS ARE 4 UNLESS NOTED ON DRAWING						
MATERIAL LIST FOR ASSEMBLY MK'D p.4						
Mark	Profile	Material	No.	Length	Area	Weight
p4	RHS100X100X6	S355J2H	1	3450	1.3	58.4 !!
F33	FL10*90	S355J2	2	140	0.0	1.0
Total				1.4	60.3	

Finish Class
Standard

Surface treatment info:	Thickness/start point--> length	No.
Overall Painting	Primerµm whole asse***	2

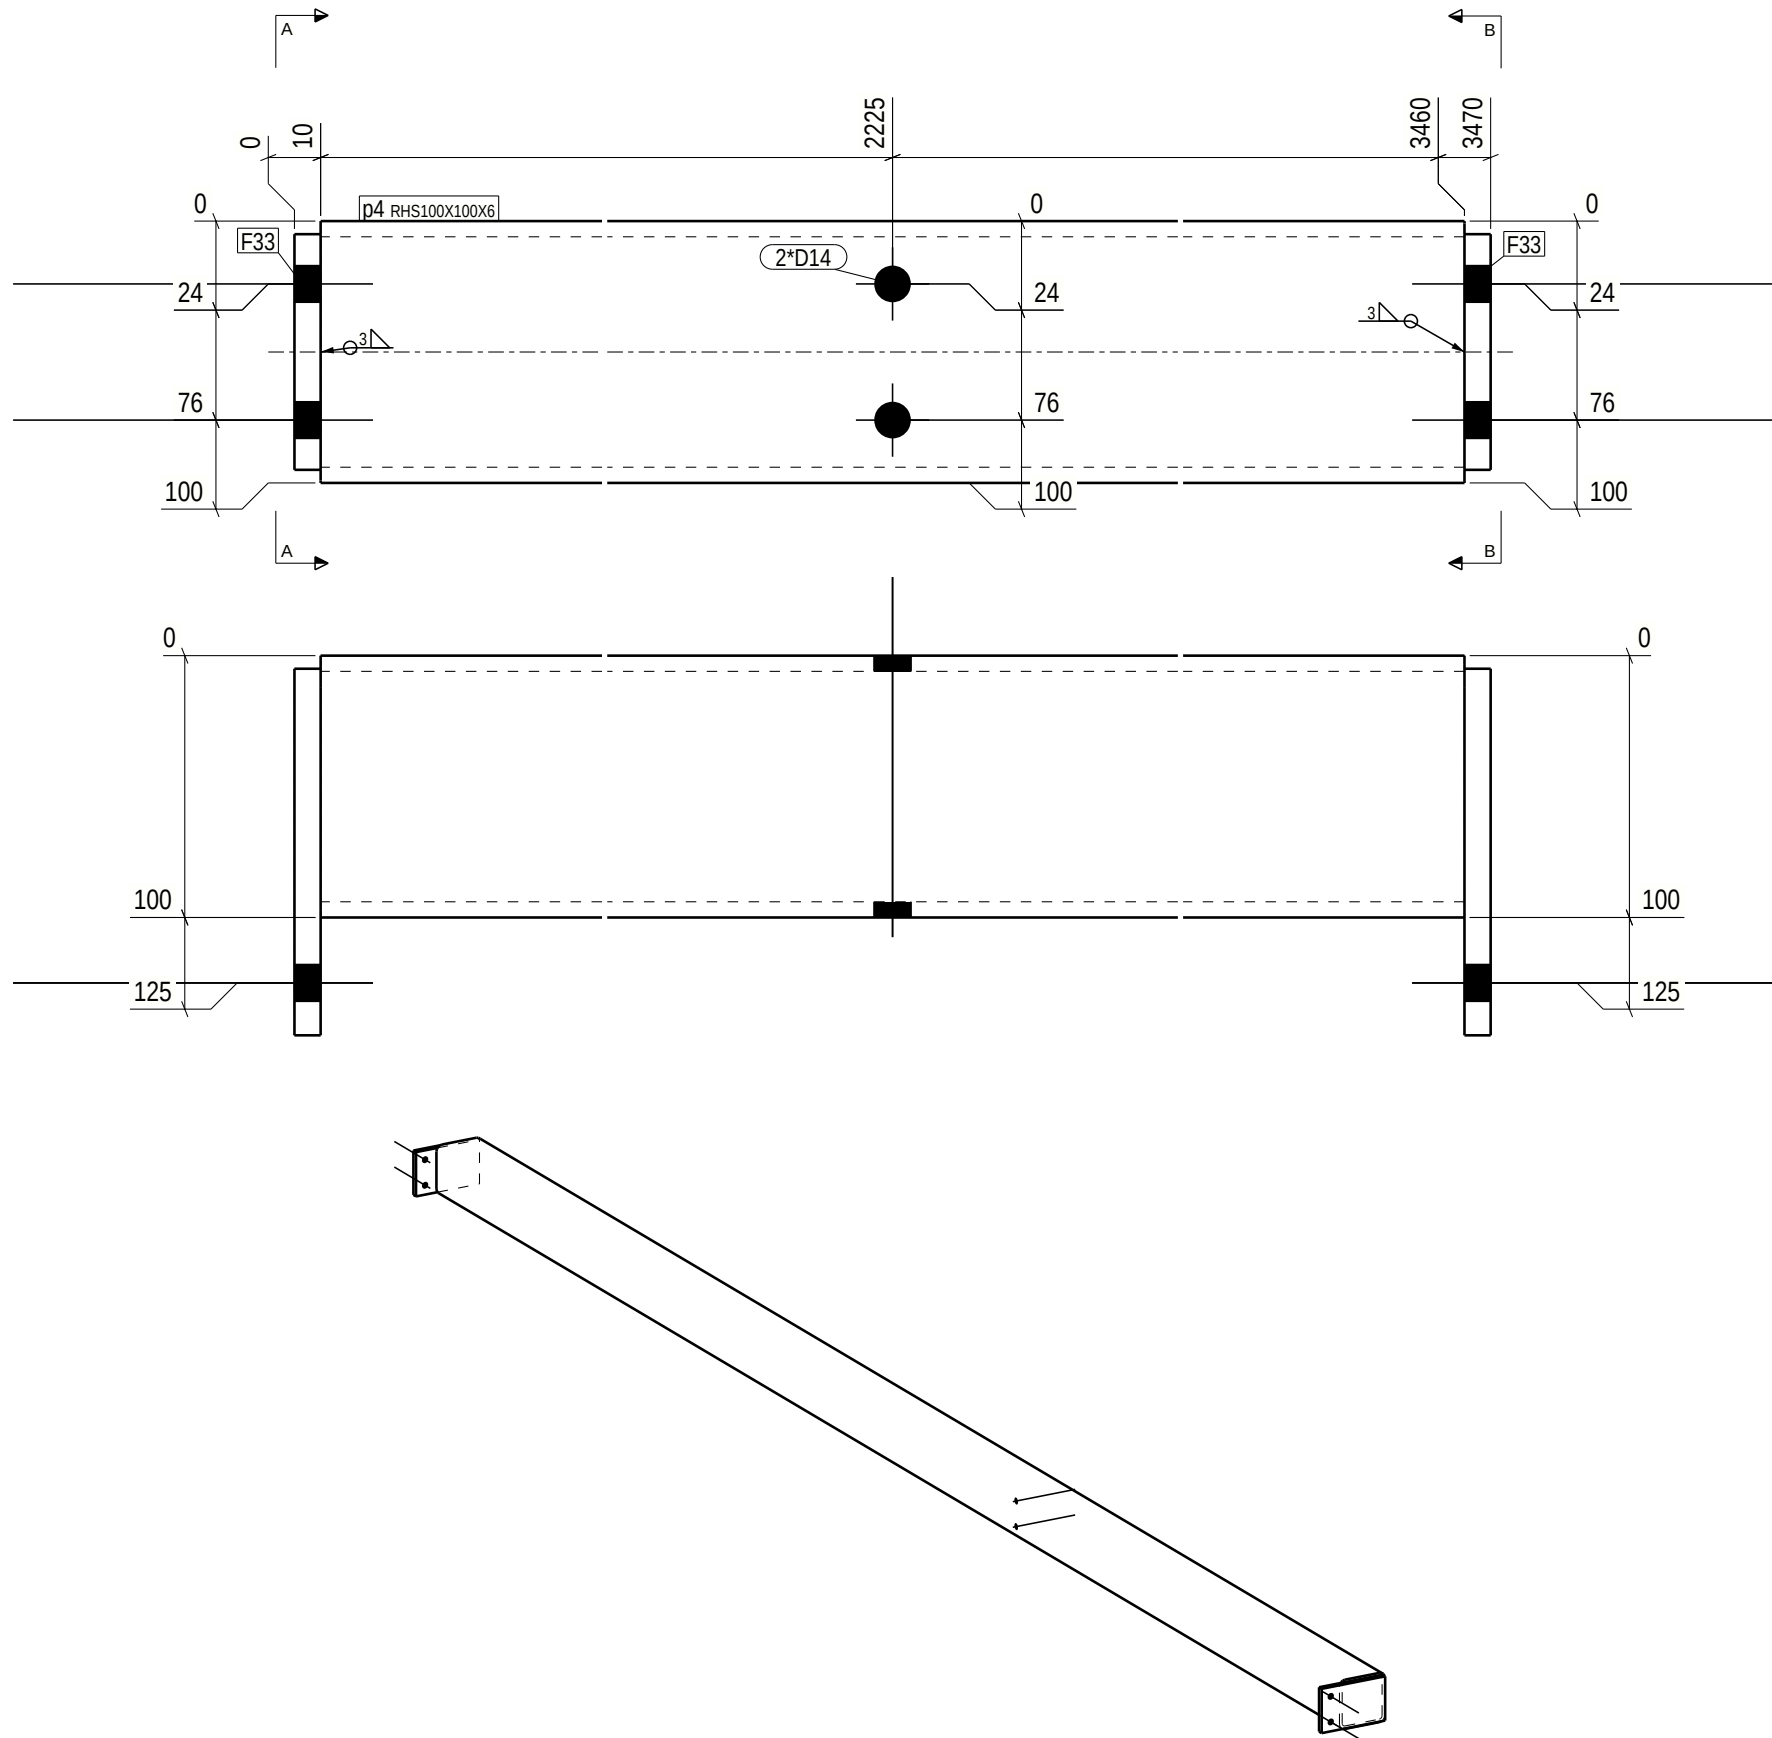

Special
surface treatment



weld a = 4mm

PHASE	QUANTITY
1	2

* o 3 0 4 8 0 - 1 *							DS		Skalkonstruktion		* A p 4 *	
PROJECT		Akkasæter Lager- og vedlikeholdshall					EXEC. CLASS			EXC 2		
MEMBER		Portomfatning			QUANTITY:		2		PROJECT No		30480-1	
REVISION		ISSUED: 07.11.2025			DRAFTER:		ZLL		DRAWING No.		p.4	
					BIM control:		SST					