
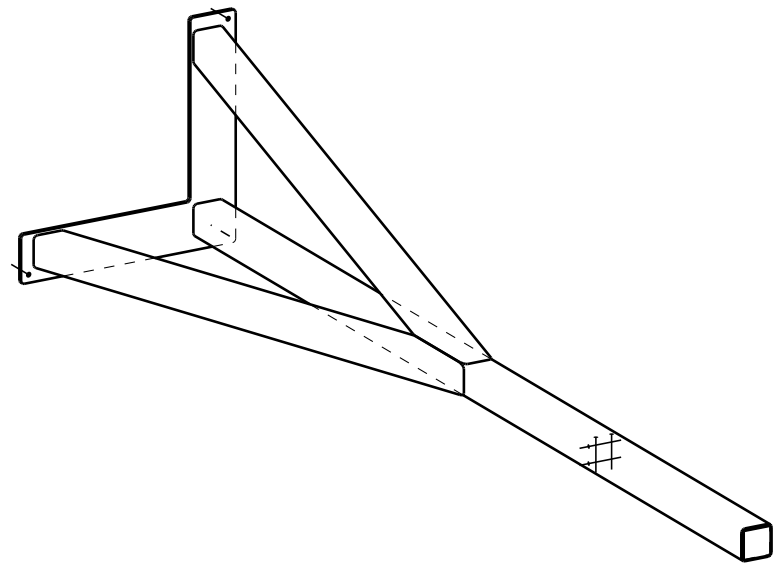
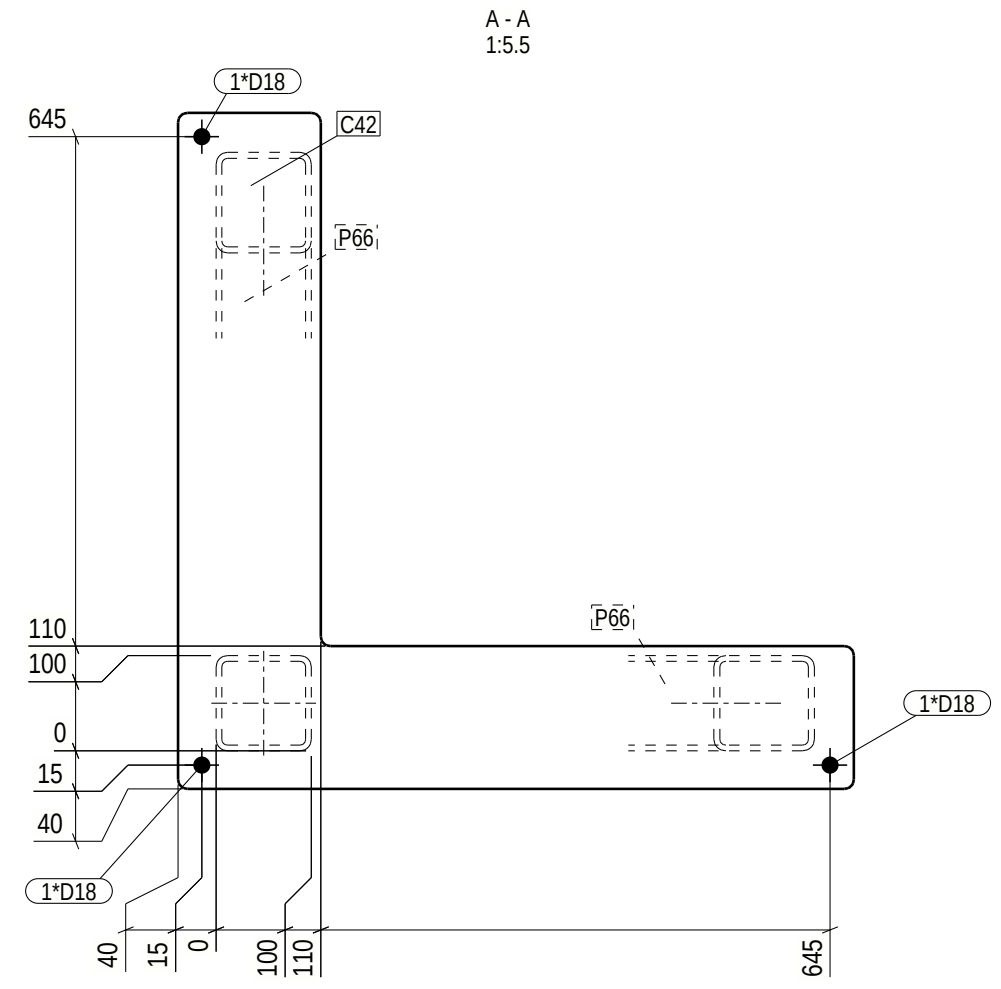


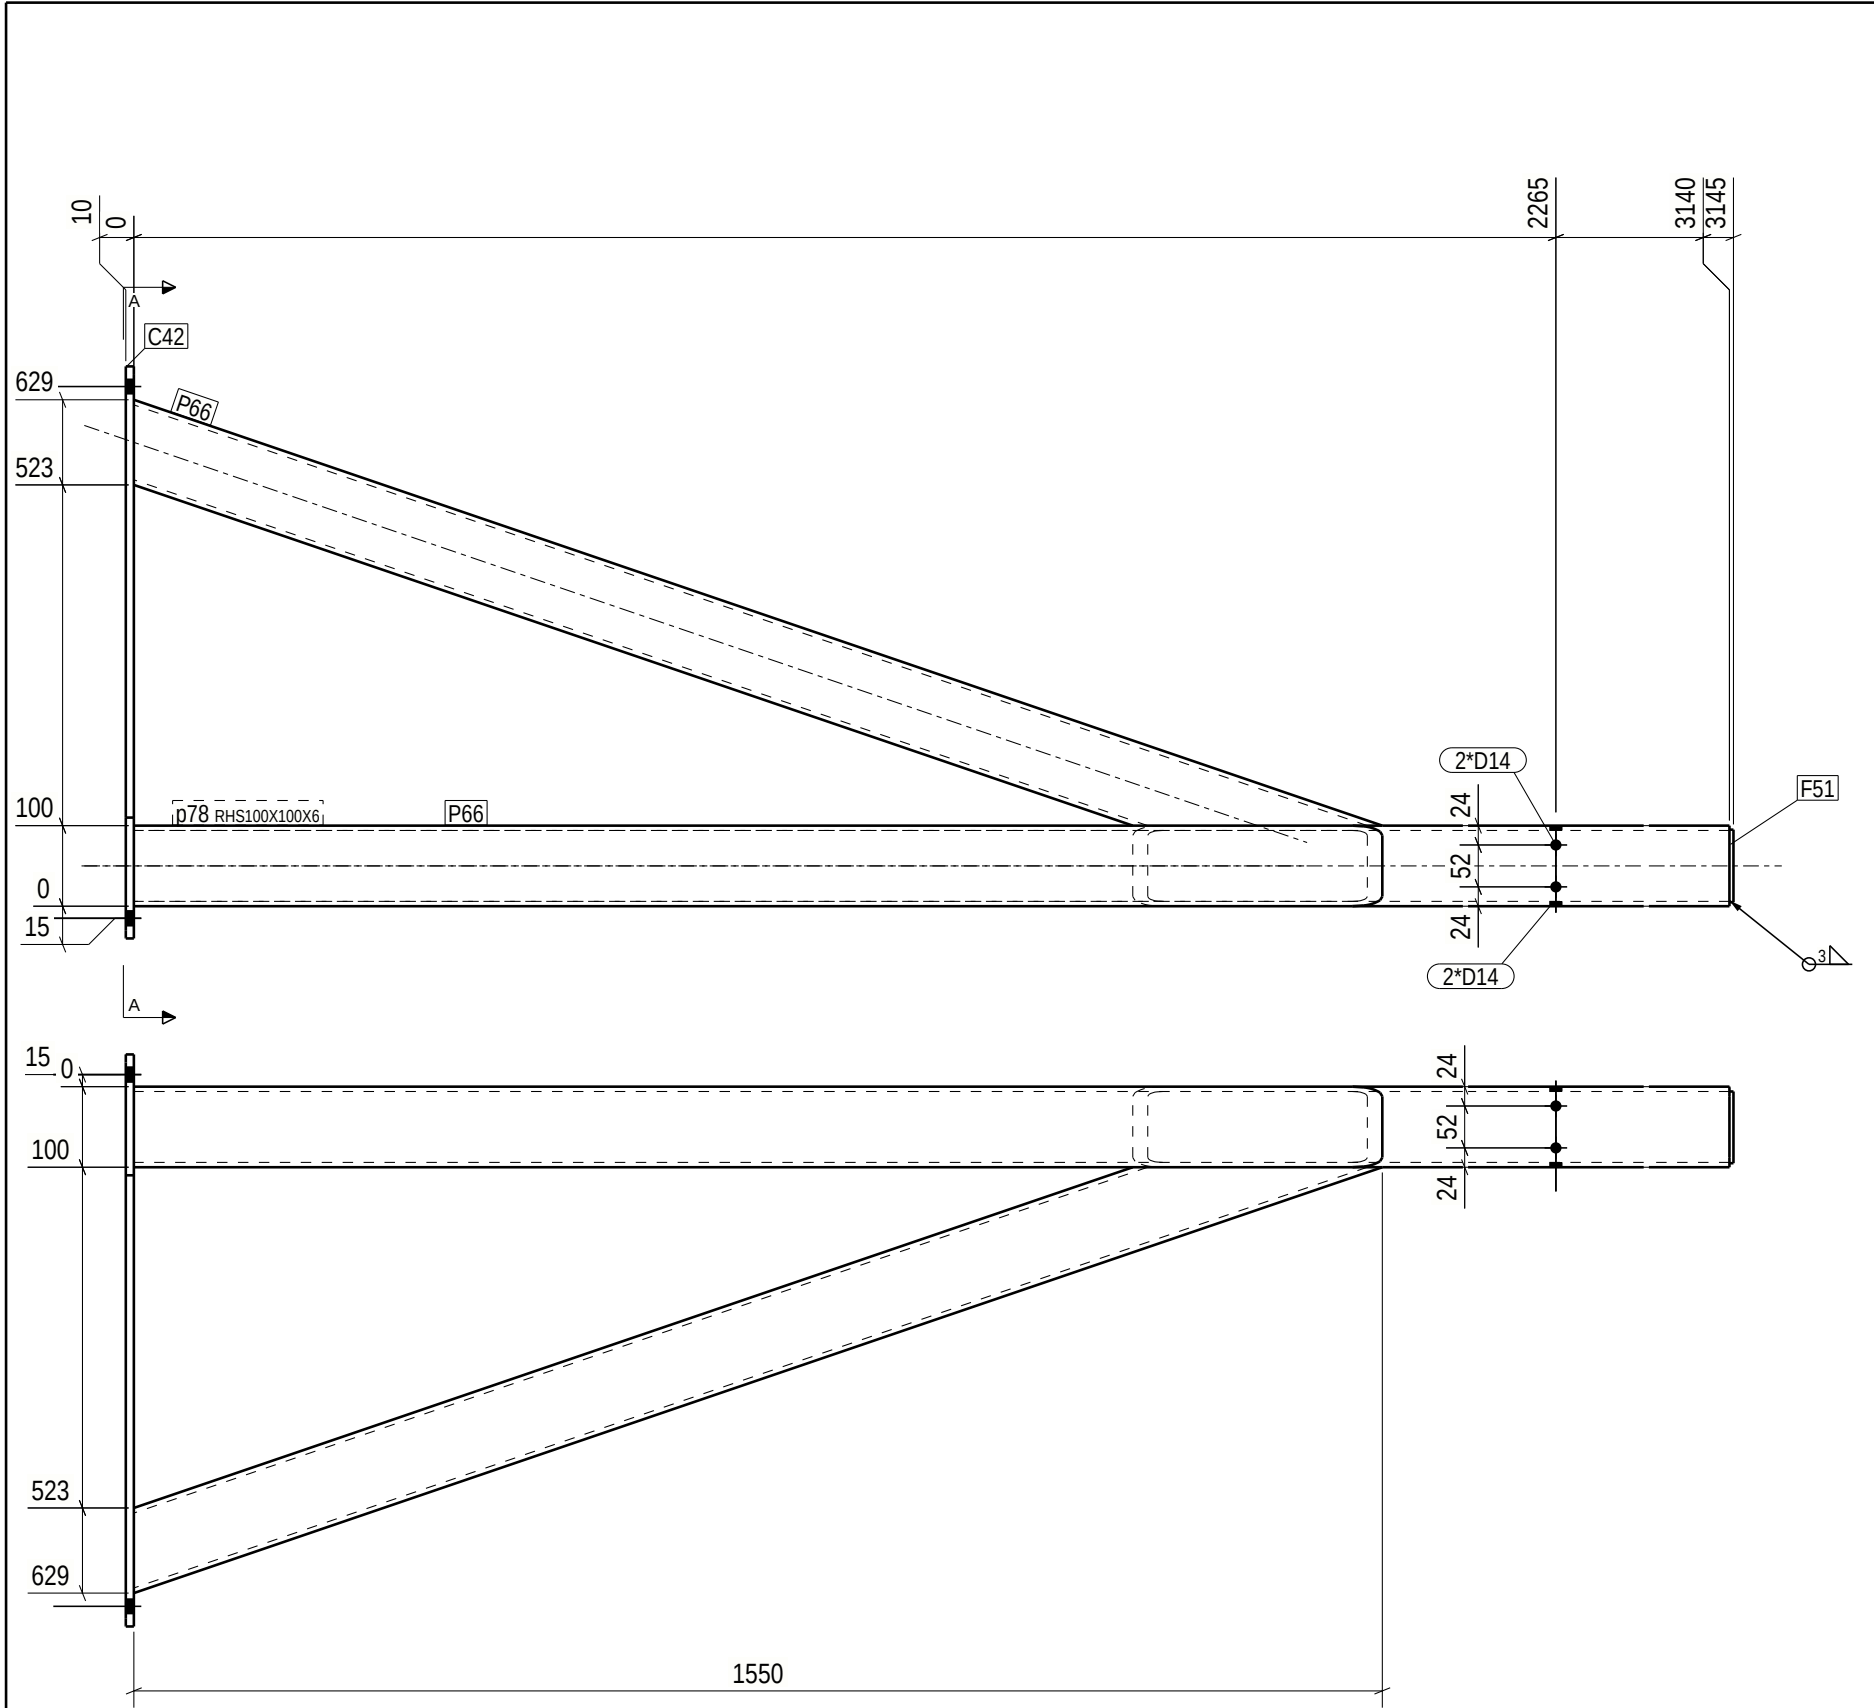

GENERAL NOTES: For your safety, check weight before handling:
0-5kg Light 5-15kg Normal 15+kg Heavy

ALL WELDS ARE 4 UNLESS NOTED ON DRAWING

MATERIAL LIST FOR ASSEMBLY MK'D p.78						
Mark	Profile	Material	No.	Length	Area	Weight
p78	RHS100X100X6	S355J2H	1	3140	1.2	53.1 !!
C42	PL10*710	S355J2	1	710	0.4	14.9
F51	FL5*89	S355J2	1	90	0.0	0.3
P66	RHS100X100X6	S355J2H	2	1638	0.6	24.9 !!
Total					2.8	118.2

Finish Class
Standard

Surface treatment info:	Thickness/start point-> length	No.
Overall Painting	Primerµm whole asse***	2

Special surface treatment weld a = 4

PHASE	QUANTITY
1	2

* o 3 0 4 8 0 - 1 * DS Steelkonstruktion * A p 7 8 *			
PROJECT	Akkasæter Lager- og vedlikeholdshall	EXEC. CLASS	EXC 2
MEMBER	Portomfatning	QUANTITY:	2
REVISION	ISSUED: 07.11.2025	DRAFTER: ZLL	PROJECT No 30480-1
	BIM control: SST		DRAWING No. p.78