


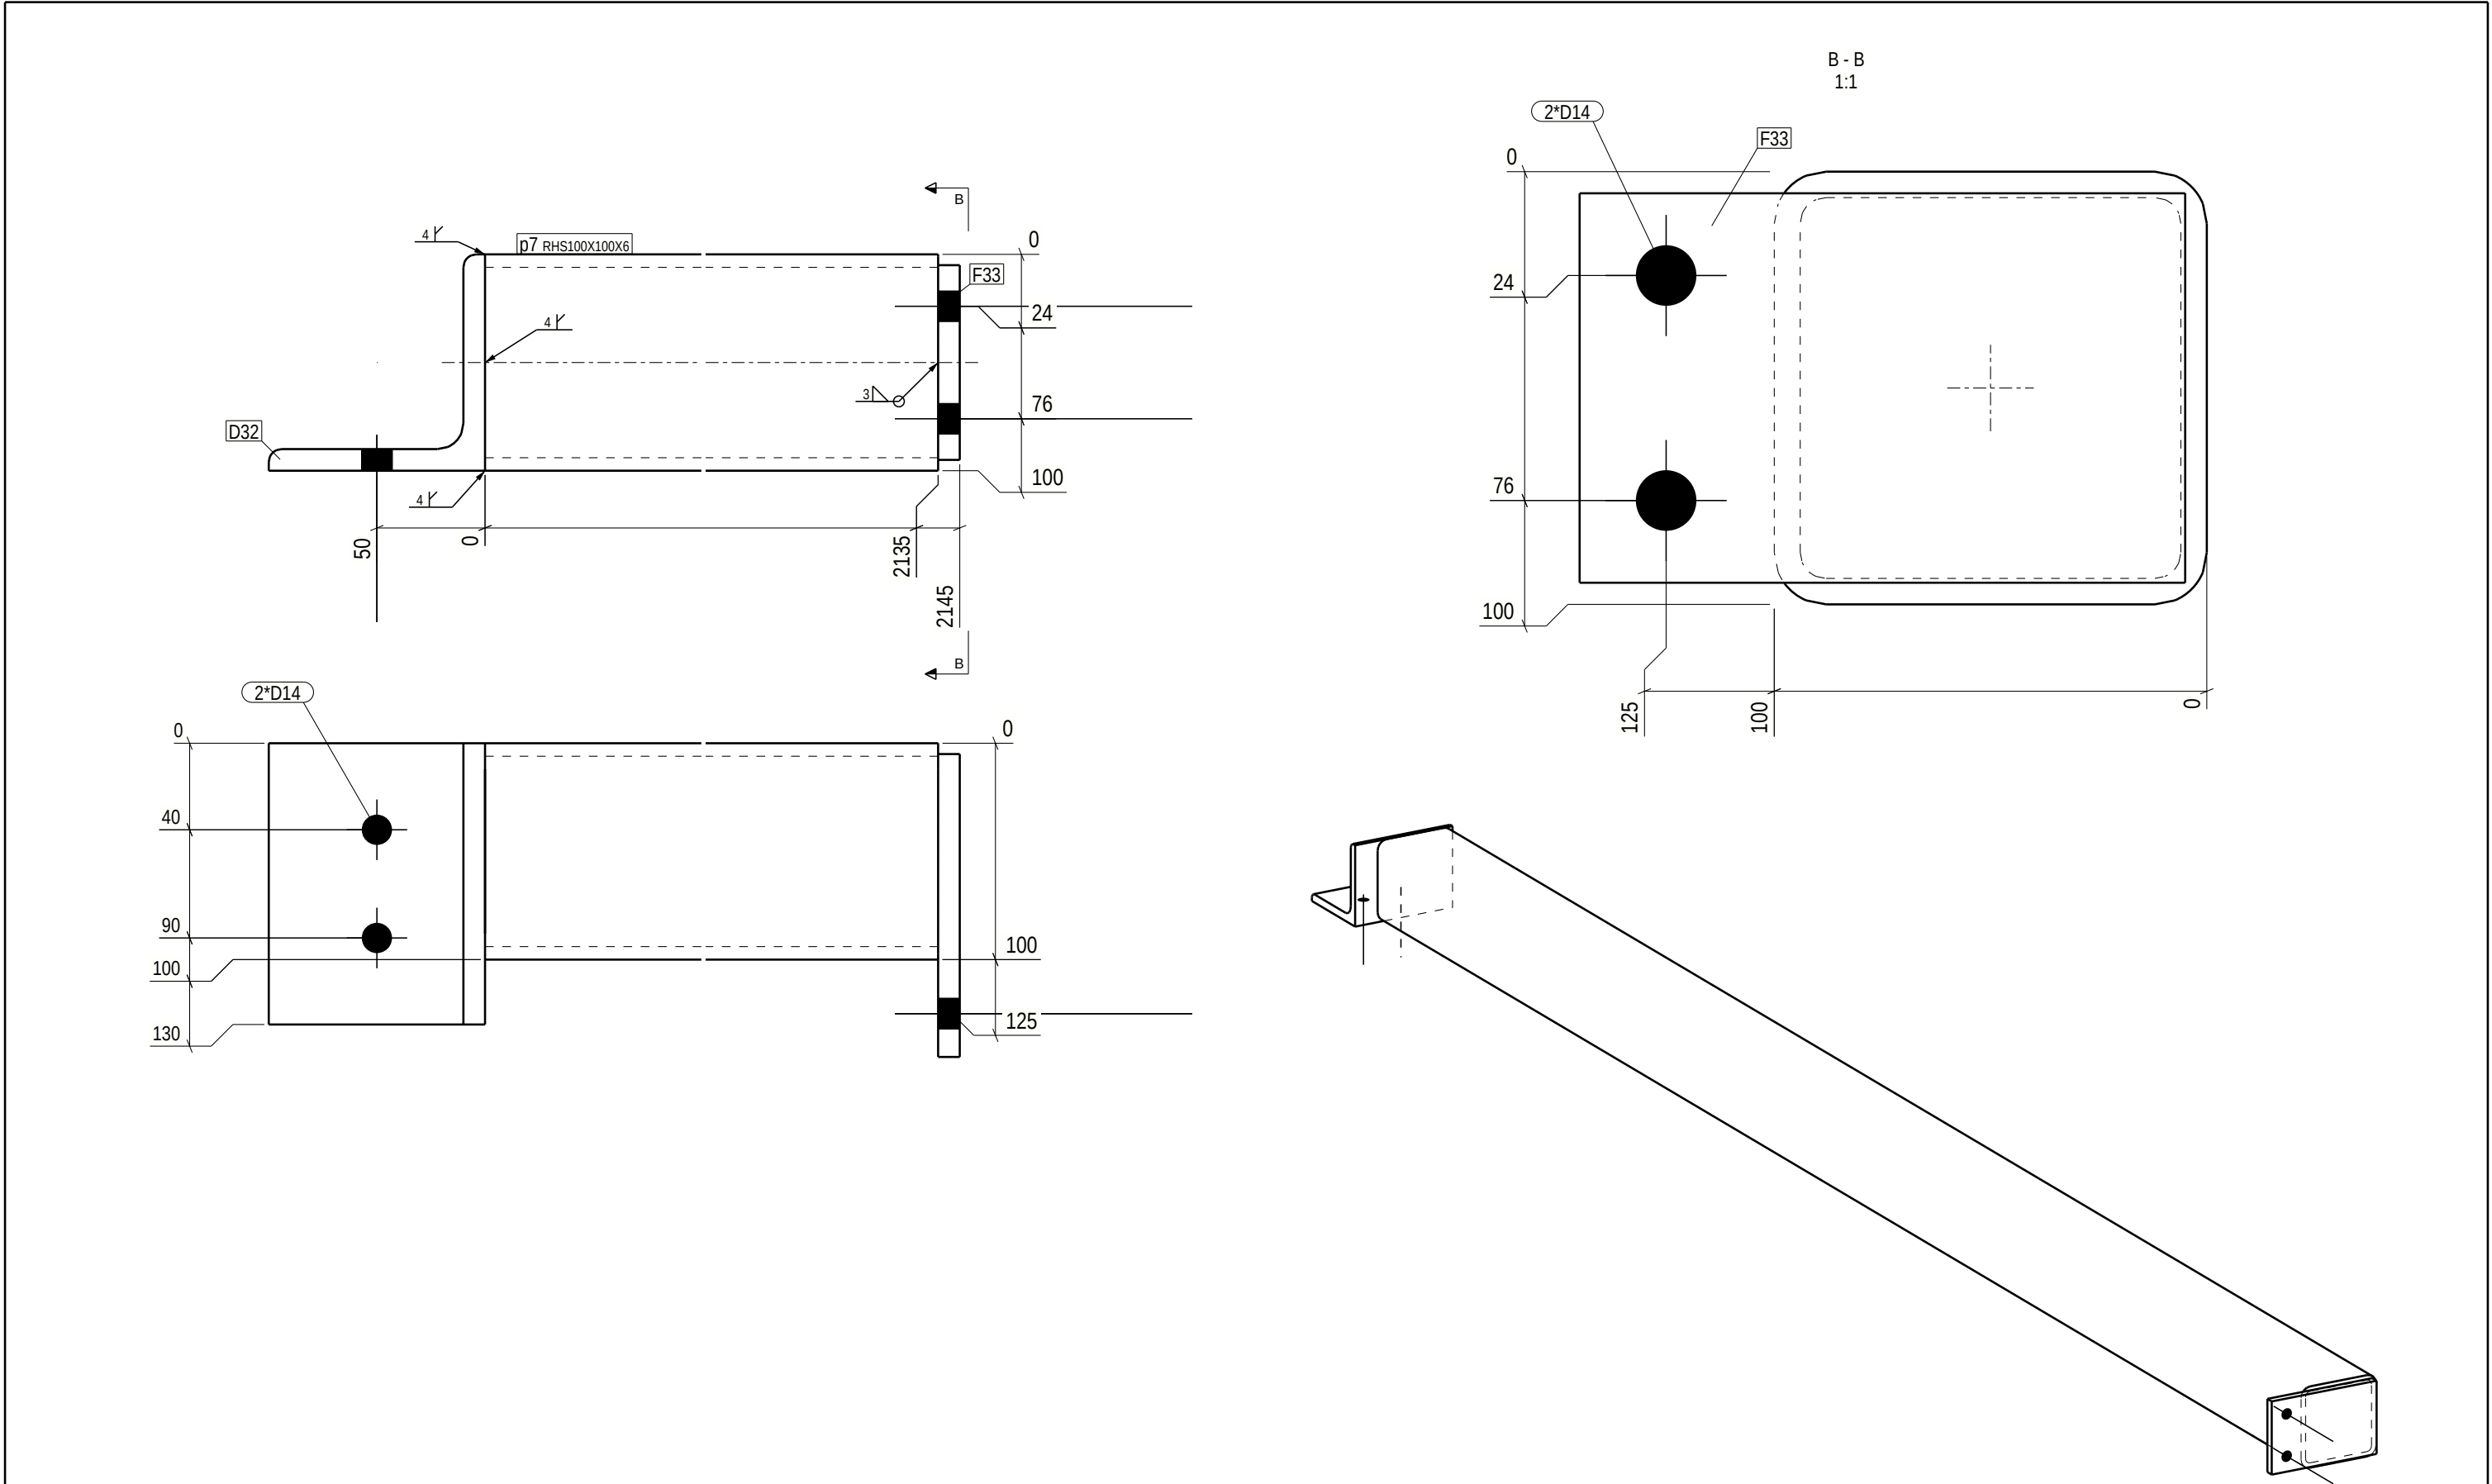

GENERAL NOTES: For your safety, check weight before handling:

ALL WELDS ARE 4 UNLESS NOTED ON DRAWING

MATERIAL LIST FOR ASSEMBLY MK'D p.7 2 No. Required

Mark	Profile	Material	No.	Length	Area	Weight
p7	RHS100X100X6	S355J2H	1	2135	0.8	36.1 !!
D32	L100*10	S355J2	1	130	0.1	2.0
F33	FL10*90	S355J2	1	140	0.0	1.0
Total					0.9	39.1

Finish Class
Standard

Surface treatment info:	Thickness/start point-> length	No.
Overall Painting	C2M RAL7016µm whole**2	

Special surface treatment weld a = 4

PHASE	QUANTITY
1	2

* o 3 0 4 8 0 - 1 * DS Steelkonstruktion * A p 7 *			
PROJECT	Akkasæter Lager- og vedlikeholdshall	EXEC. CLASS	EXC 2
MEMBER	Portomfatning	QUANTITY:	2 PROJECT No 30480-1
REVISION	ISSUED: 07.11.2025	DRAFTER: ZLL SST	DRAWING No. p.7