


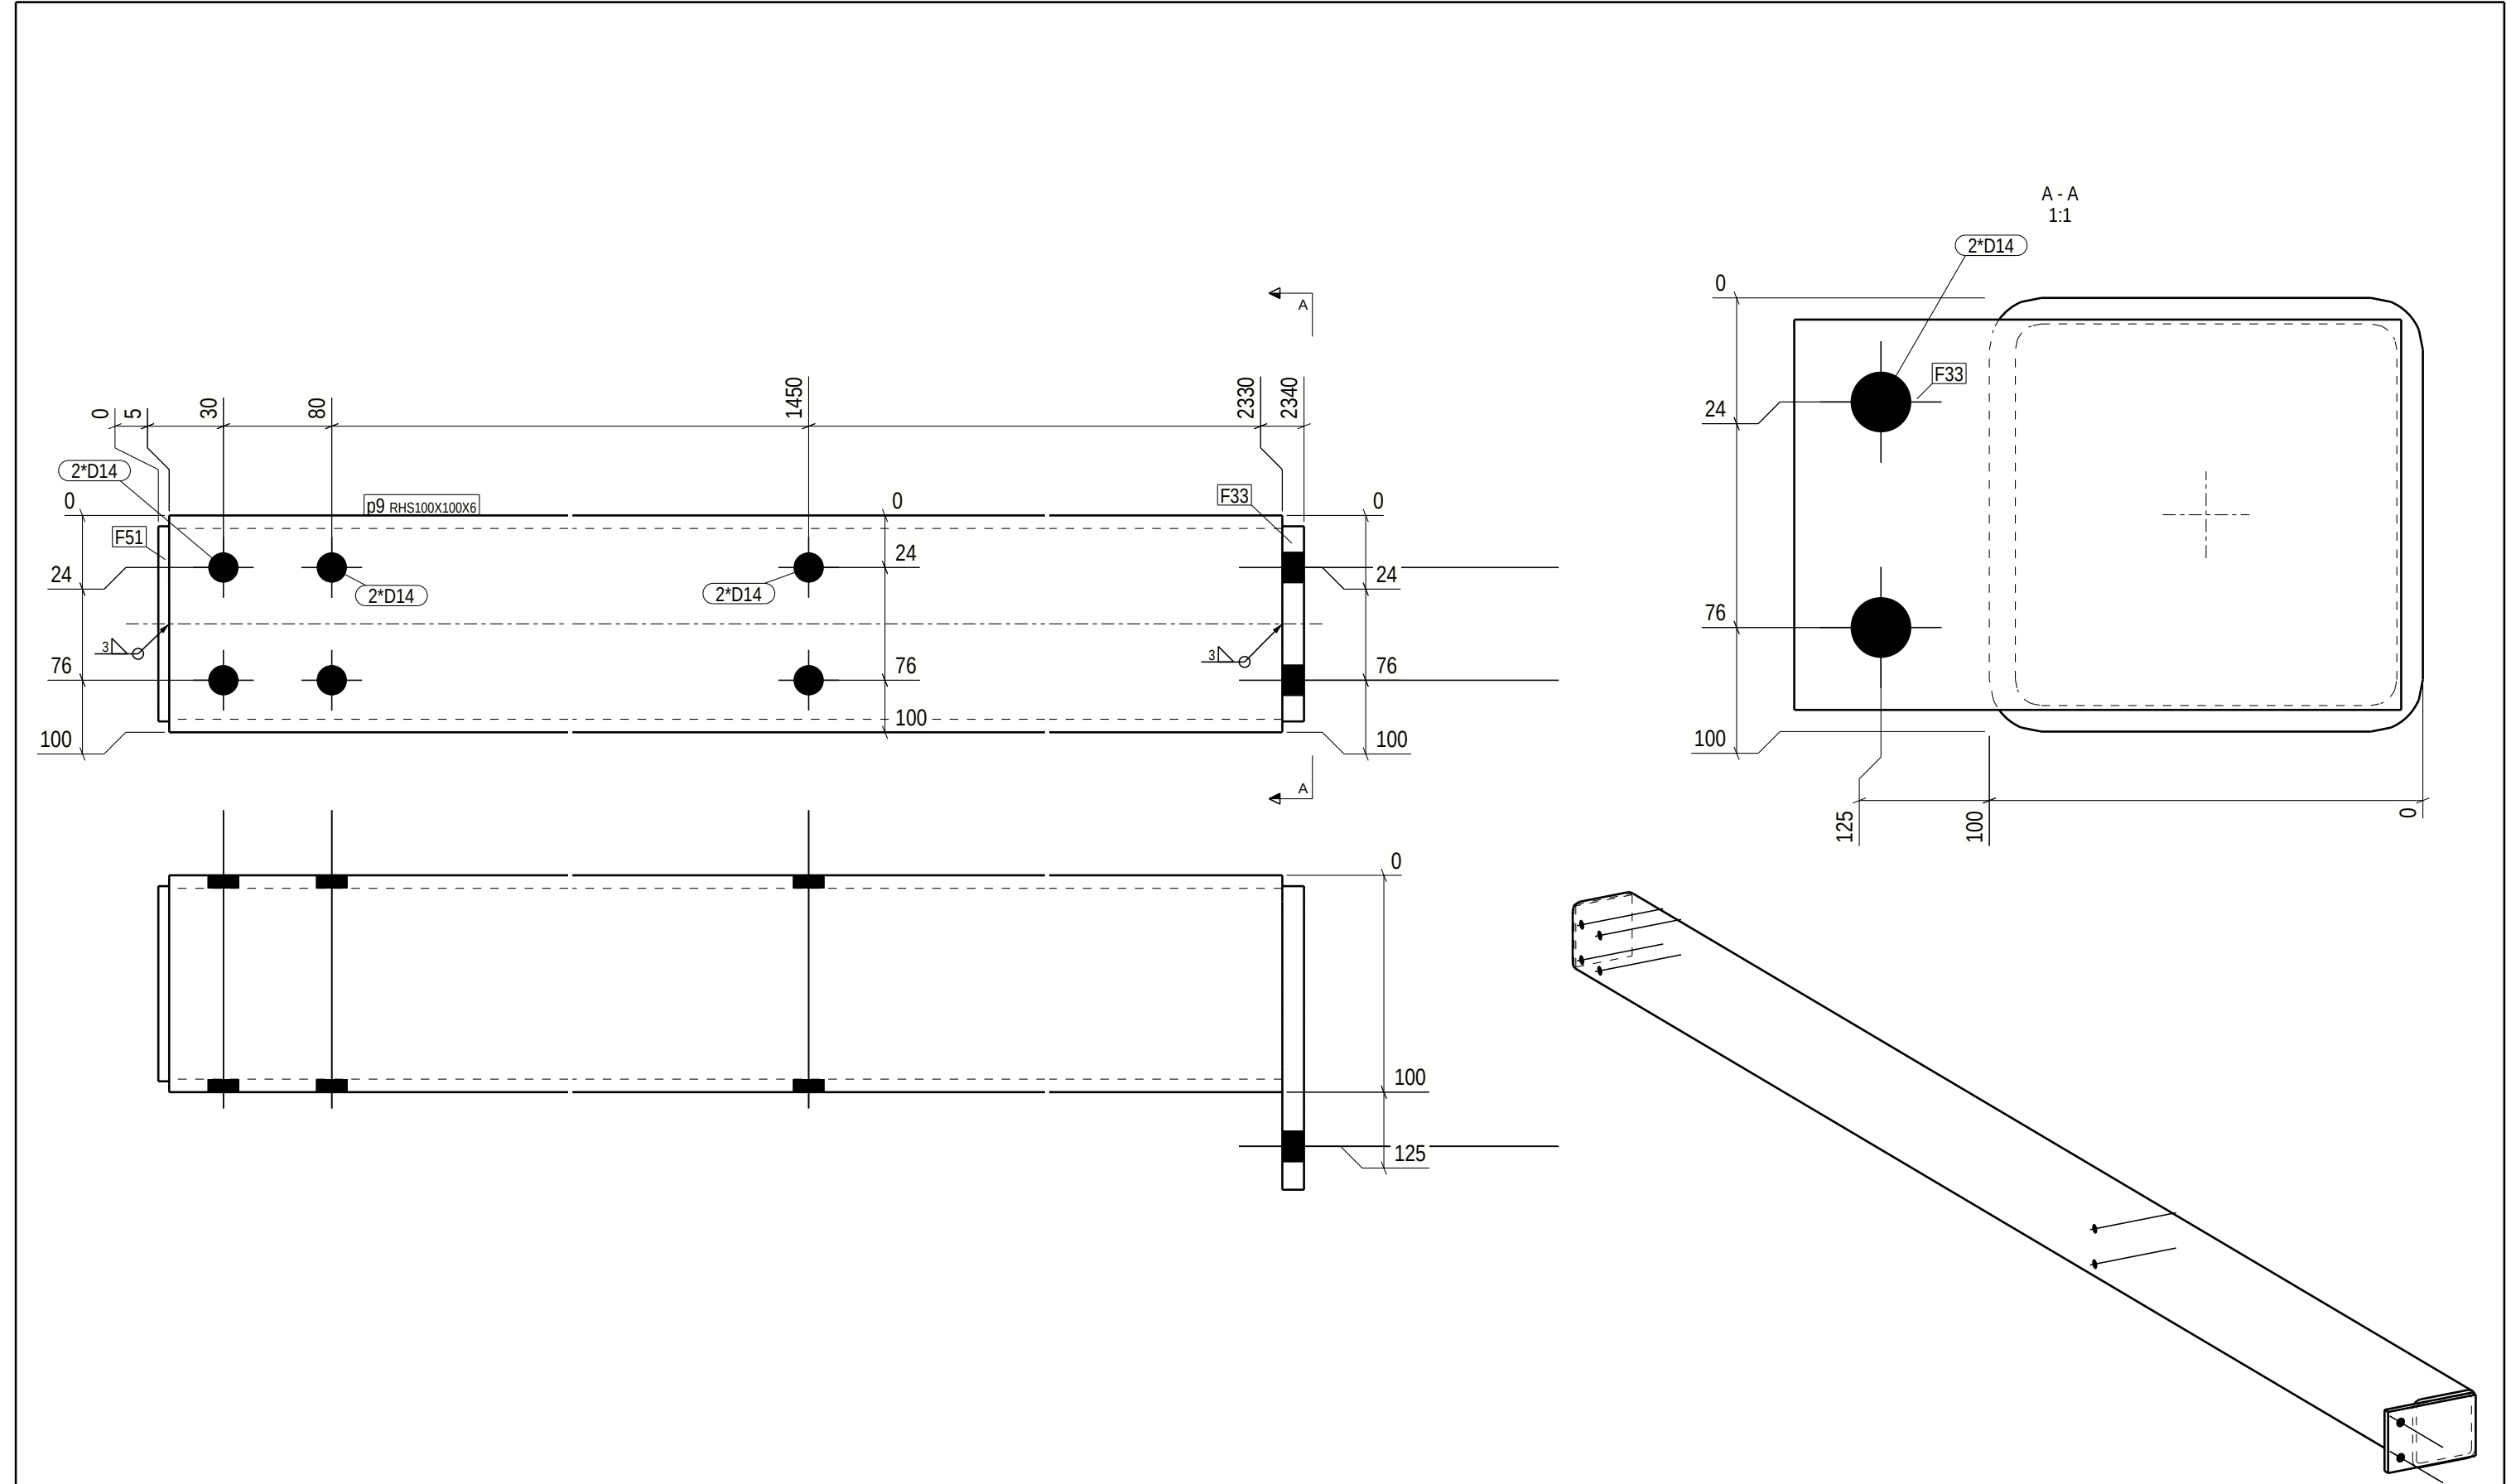

|                                                    |              |          |     |        |      |         |
|----------------------------------------------------|--------------|----------|-----|--------|------|---------|
| GENERAL NOTES:                                     |              |          |     |        |      |         |
| For your safety, check weight before handling:     |              |          |     |        |      |         |
| 0-5kg Light 5-15kg Normal 15+kg Heavy              |              |          |     |        |      |         |
| ALL WELDS ARE 4 UNLESS NOTED ON DRAWING            |              |          |     |        |      |         |
| MATERIAL LIST FOR ASSEMBLY MK'D p.9 1 No. Required |              |          |     |        |      |         |
| Mark                                               | Profile      | Material | No. | Length | Area | Weight  |
| p9                                                 | RHS100X100X6 | S355J2H  | 1   | 2325   | 0.9  | 39.3 !! |
| F33                                                | FL10*90      | S355J2   | 1   | 140    | 0.0  | 1.0     |
| F51                                                | FL5*90       | S355J2   | 1   | 90     | 0.0  | 0.3     |
| Total                                              |              |          |     |        | 0.9  | 40.6    |

Finish Class  
Standard

|                         |                                |     |
|-------------------------|--------------------------------|-----|
| Surface treatment info: | Thickness/start point-> length | No. |
| Overall Painting        | C2M RAL7016µm whole            | **1 |



Special  
surface treatment



weld a = 4

|       |          |
|-------|----------|
| PHASE | QUANTITY |
| 1     | 1        |

|                                                    |                                      |                  |                    |
|----------------------------------------------------|--------------------------------------|------------------|--------------------|
| * o 3 0 4 8 0 - 1 * DS Stahlkonstruktion * A p 9 * |                                      |                  |                    |
| PROJECT                                            | Akkasæter Lager- og vedlikeholdshall | EXEC. CLASS      | EXC 2              |
| MEMBER                                             | Portomfatning                        | QUANTITY:        | 1                  |
| REVISION                                           | ISSUED: 07.11.2025                   | DRAFTER: ZLL     | PROJECT No 30480-1 |
|                                                    |                                      | BIM control: SST | DRAWING No. p.9    |