
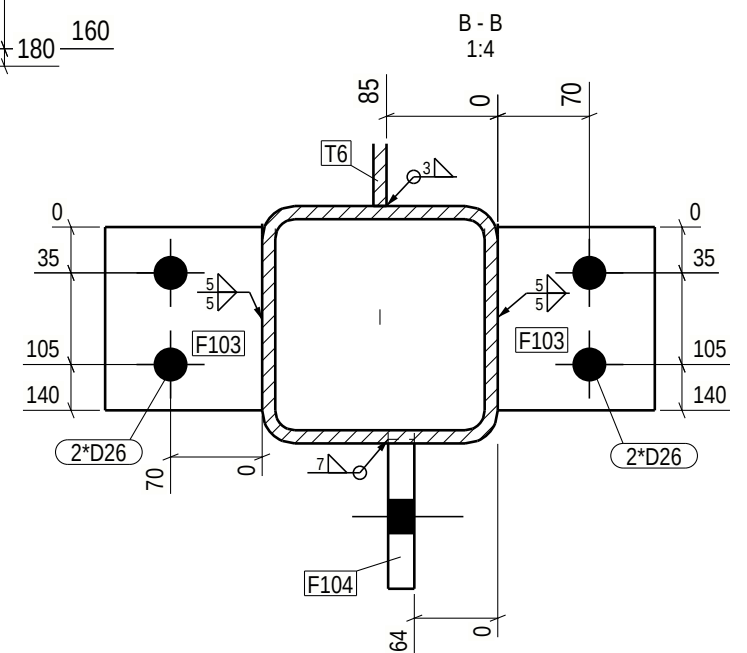
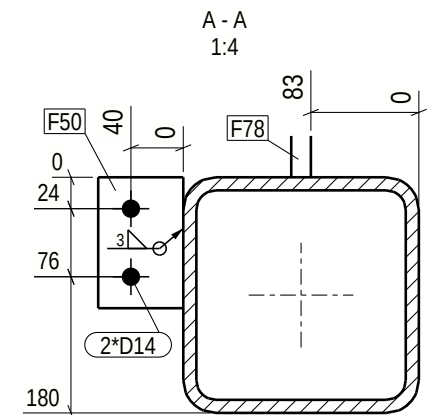


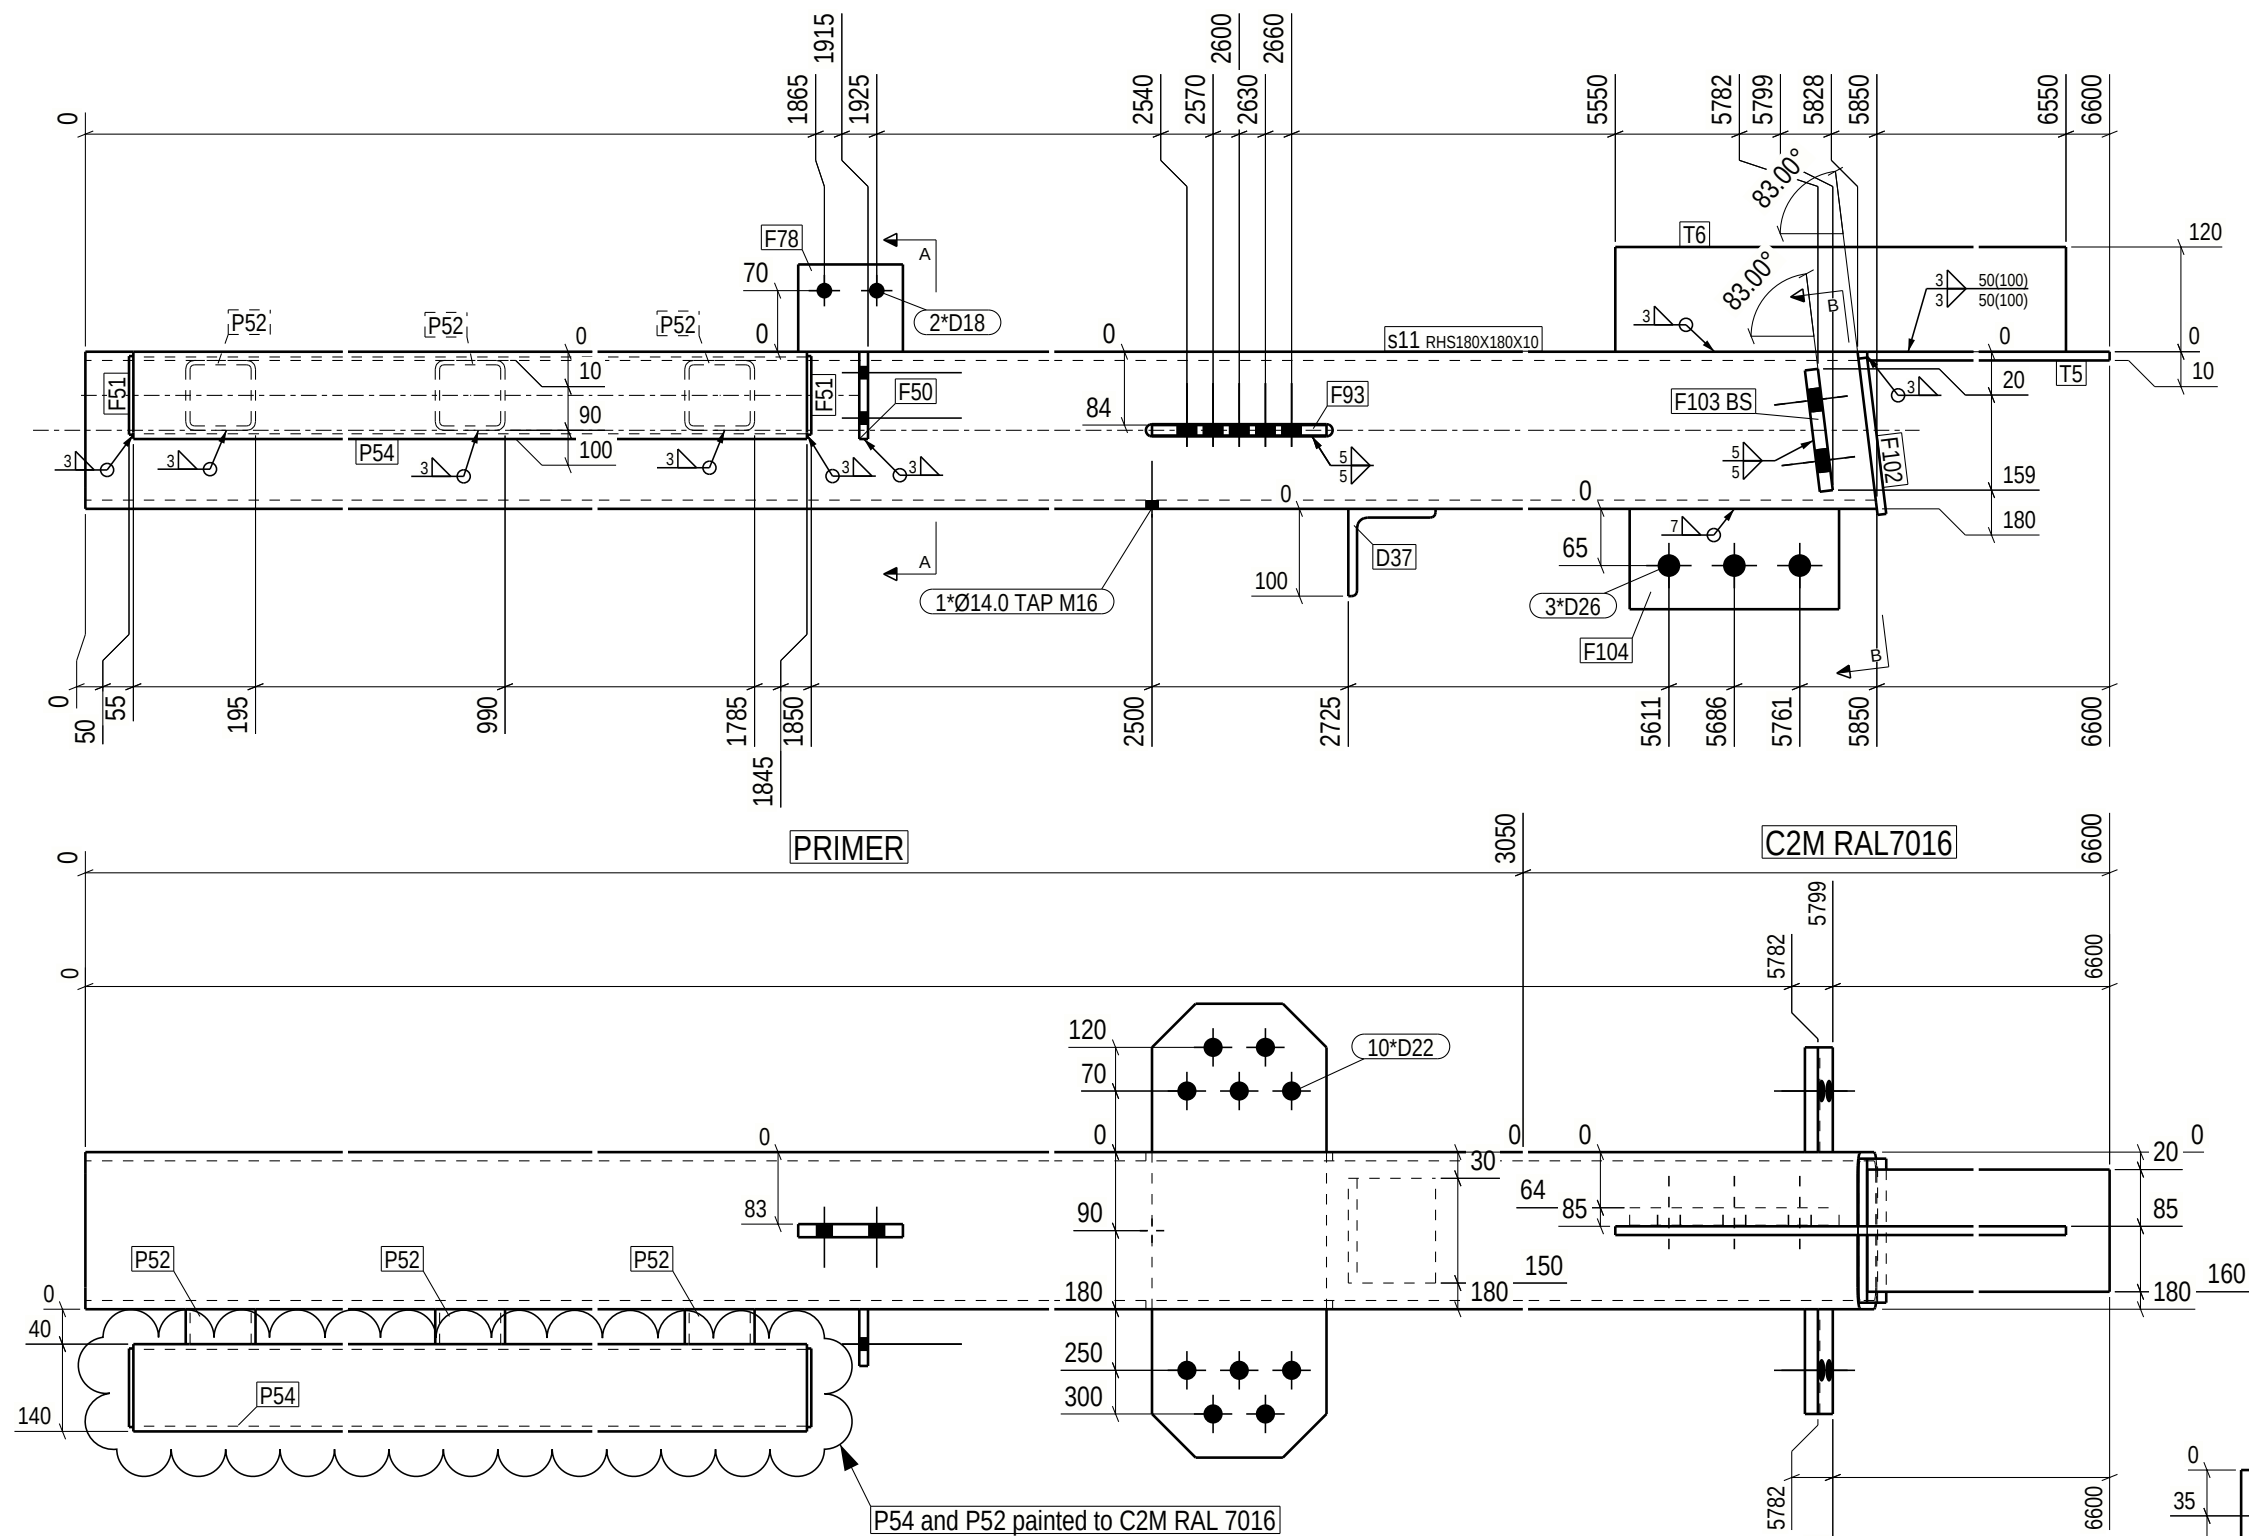

GENERAL NOTES: For your safety, check weight before handling:
0-5kg Light 5-15kg Normal 15+kg Heavy
ALL WELDS ARE 4 UNLESS NOTED ON DRAWING

MATERIAL LIST FOR ASSEMBLY MK'D S.11						1	No. Required
Mark	Profile	Material	No.	Length	Area	Weight	
s11	RHS180X180X10	S355J2H	1	5850	4.0	294.0 !!	
D37	L100*10	S355J2	1	120	0.0	1.8	
F50	FL10*65	S355J2	1	100	0.0	0.5	
F51	FL5*90	S355J2	2	90	0.0	0.3	
F78	FL15*100	S355J2	1	120	0.0	1.4	
F93	FL12*200	S355J2	1	520	0.2	9.3	
F102	FL10*165	S355J2	1	180	0.1	2.3	
F103	FL15*120	S355J2	2	140	0.0	2.0	
F104	FL20*115	S355J2	1	240	0.1	4.3	
P52	RHS80X80X5	S355J2H	3	40	0.0	0.4	
P54	RHS100X100X6	S355J2H	1	1790	0.7	30.3 !!	
T5	FL10*140	S355J2	1	761	0.2	8.4	
T6	FL10*120	S355J2	1	1000	0.3	9.4	
Total					5.8	367.7	

Finish Class	Standard
Surface treatment info:	Thickness/start point--> length
Partial Painting	Primerµm/0 -->3050mm
	No. 1

Special surface treatment weld a = 4

PHASE	QUANTITY
1	1

* o 3 0 4 8 0 - 1 * DS Skalkonstruktion * As 1 1 *			
PROJECT	Akkasæter Lager- og vedlikeholdshall	EXEC. CLASS	EXC 2
MEMBER	Søyle	QUANTITY:	1
REVISION	ISSUED: 07.11.2025	DRAFTER:	ZLL
		BIM control:	SST
PROJECT No		30480-1	
DRAWING No.		S.11	