


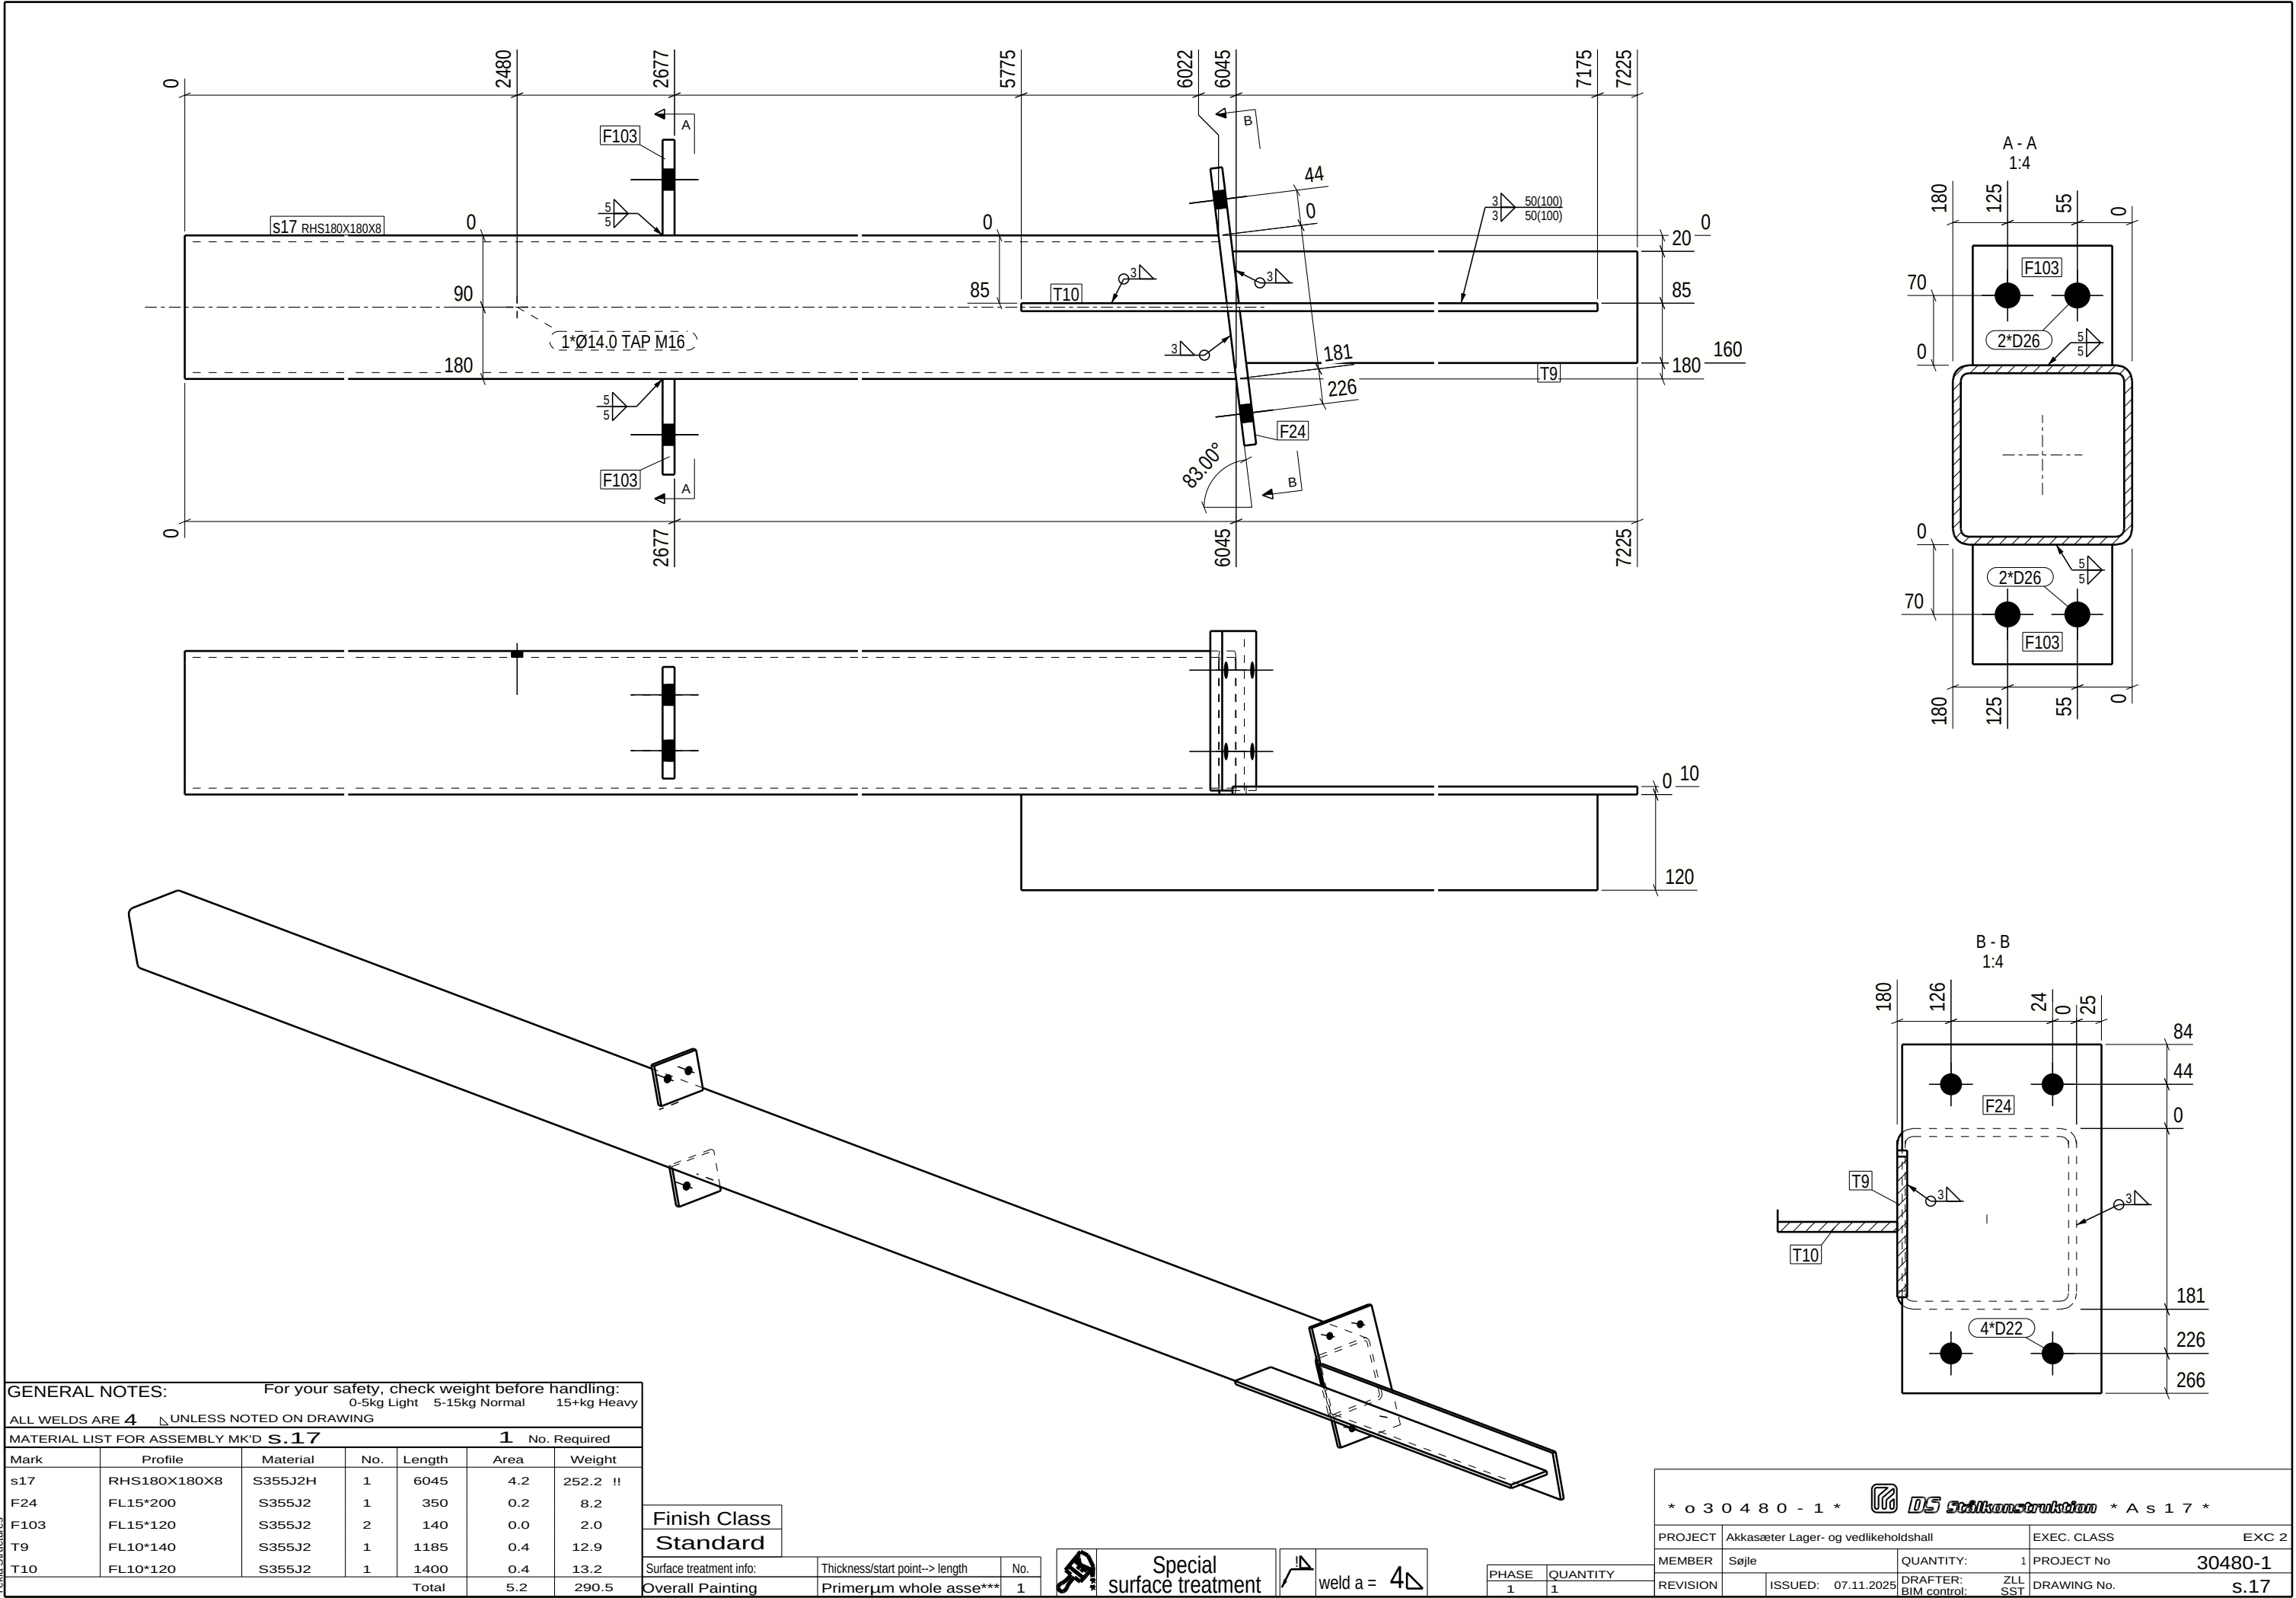

GENERAL NOTES: For your safety, check weight before handling:
0-5kg Light 5-15kg Normal 15+kg Heavy

ALL WELDS ARE 4 UNLESS NOTED ON DRAWING

MATERIAL LIST FOR ASSEMBLY MK'D s.17						1	No. Required
Mark	Profile	Material	No.	Length	Area	Weight	
s17	RHS180X180X8	S355J2H	1	6045	4.2	252.2 !!	
F24	FL15*200	S355J2	1	350	0.2	8.2	
F103	FL15*120	S355J2	2	140	0.0	2.0	
T9	FL10*140	S355J2	1	1185	0.4	12.9	
T10	FL10*120	S355J2	1	1400	0.4	13.2	
Total					5.2	290.5	

Finish Class
Standard

Surface treatment info:	Thickness/start point-> length	No.
Overall Painting	Primerµm whole asse***	1

Special surface treatment weld a = 4

PHASE	QUANTITY
1	1

* o 3 0 4 8 0 - 1 * DS Steelkonstruktion * A s 1 7 *			
PROJECT	Akkasæter Lager- og vedlikeholdshall	EXEC. CLASS	EXC 2
MEMBER	Søyle	QUANTITY:	1
REVISION	ISSUED: 07.11.2025	DRAFTER: ZLL	PROJECT No 30480-1
	BIM control: SST		DRAWING No. s.17