
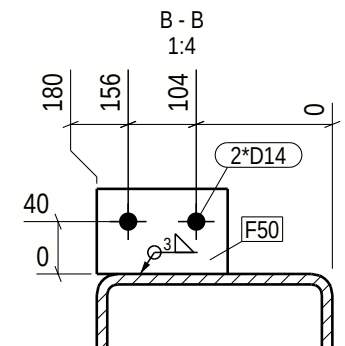
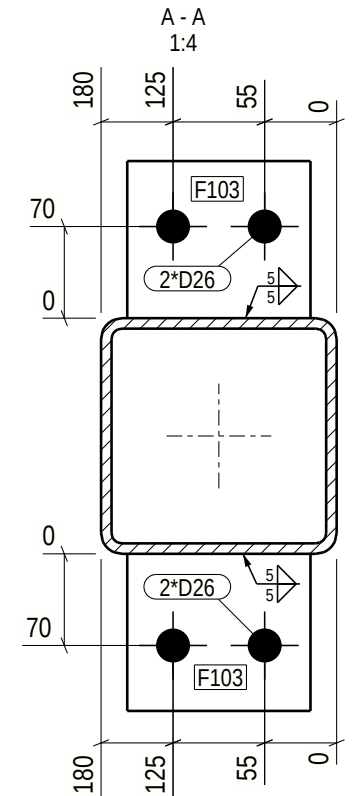


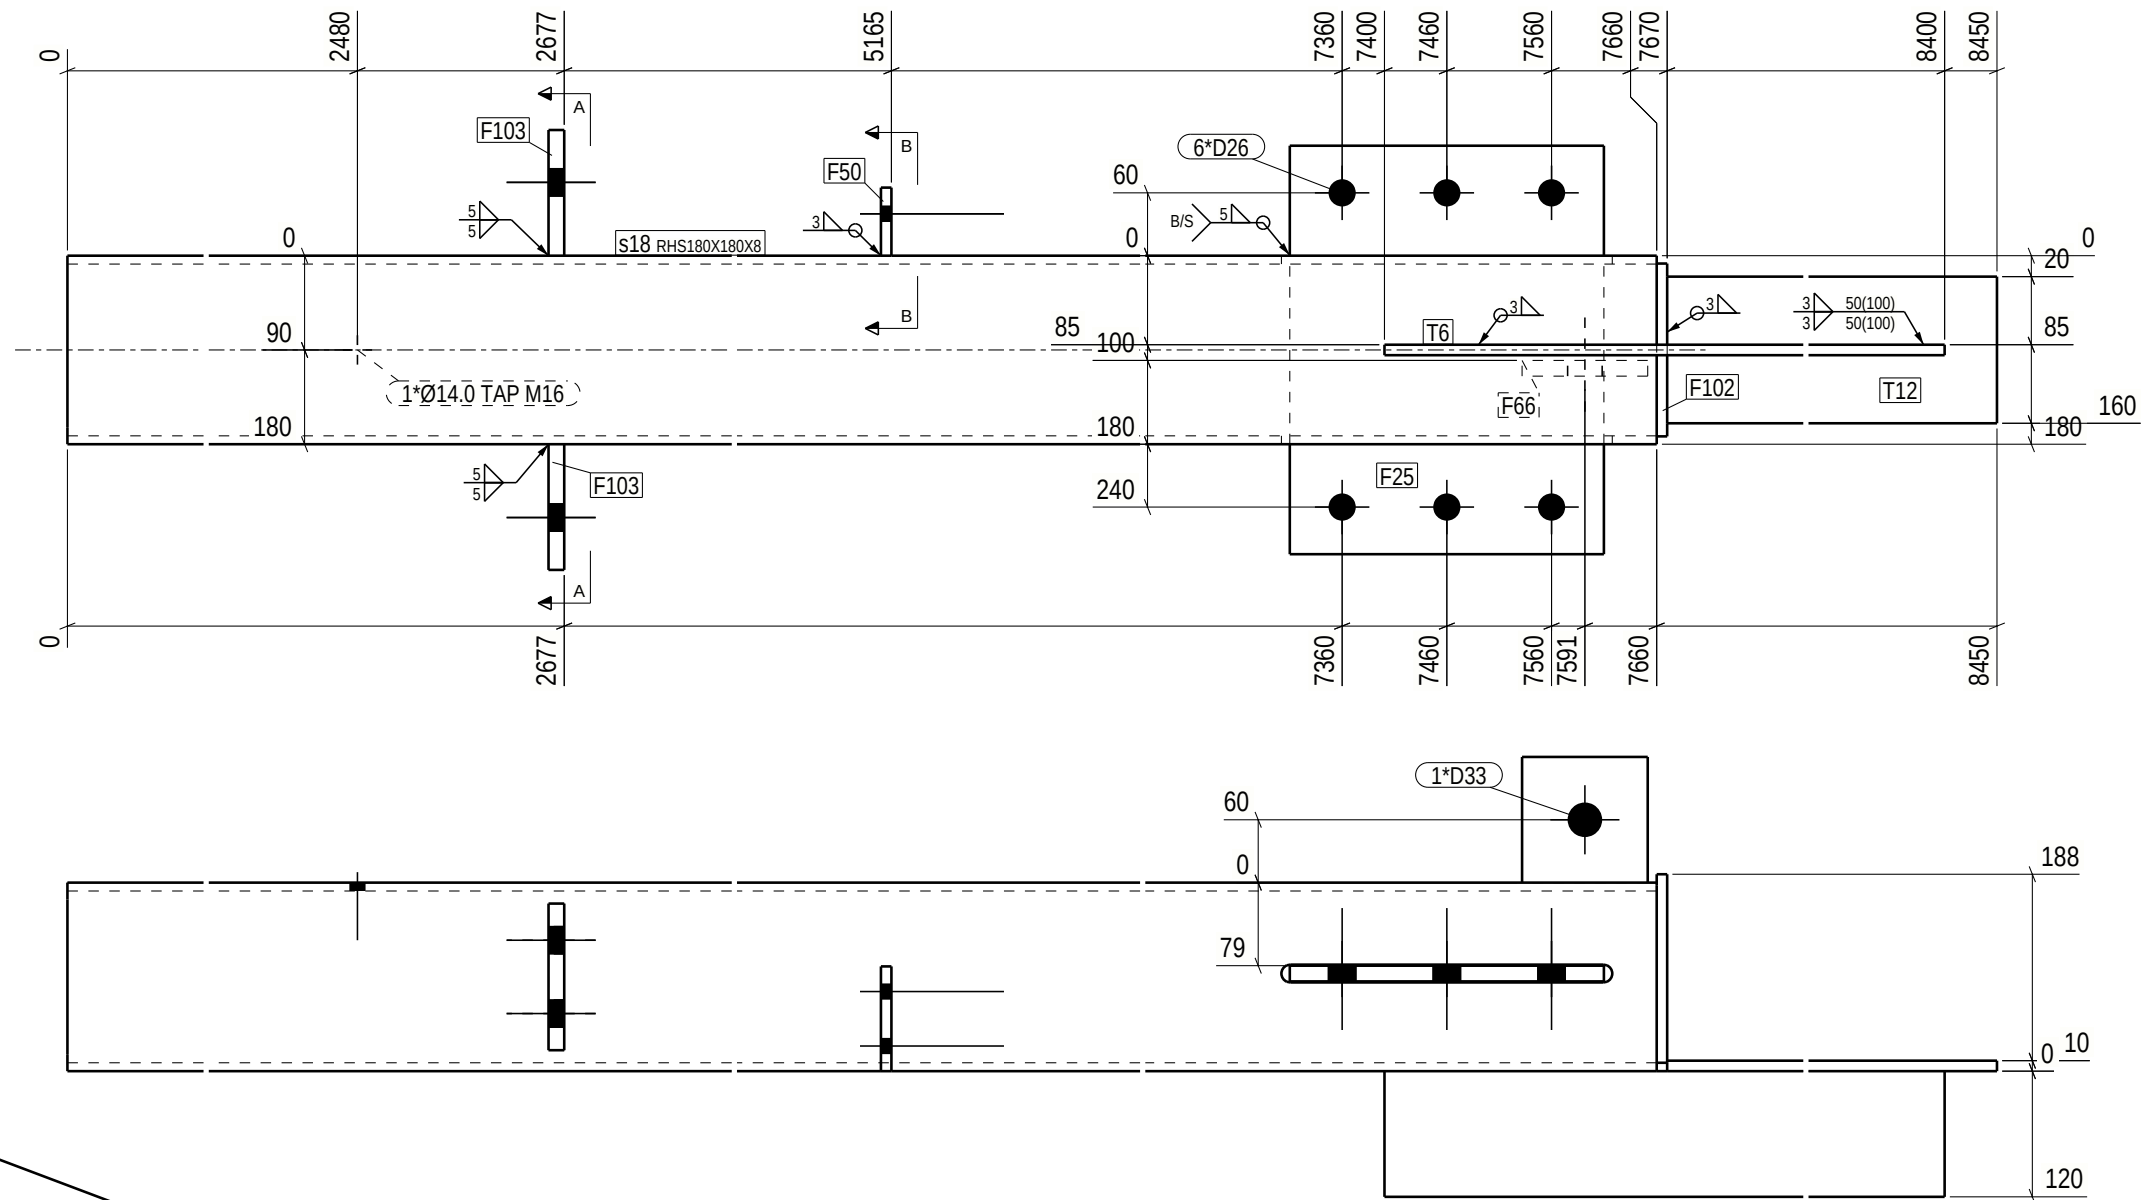

GENERAL NOTES: For your safety, check weight before handling:

ALL WELDS ARE 4 UNLESS NOTED ON DRAWING

MATERIAL LIST FOR ASSEMBLY MK'D s.18						1
Mark	Profile	Material	No.	Length	Area	Weight
s18	RHS180X180X8	S355J2H	1	7660	5.3	319.5 !!
F25	FL15*300	S355J2	1	390	0.3	13.8
F50	FL10*65	S355J2	1	100	0.0	0.5
F66	FL15*120	S355J2	1	120	0.0	1.7
F102	FL10*165	S355J2	1	180	0.1	2.3
F103	FL15*120	S355J2	2	140	0.0	2.0
T6	FL10*120	S355J2	1	1000	0.3	9.4
T12	FL10*140	S355J2	1	780	0.2	8.6
Total					6.3	359.7

Finish Class
Standard

Surface treatment info:	Thickness/start point-> length	No.
Overall Painting	Primerµm whole asse***	1



Special
surface treatment



weld a = 4

PHASE	QUANTITY
1	1

* o 3 0 4 8 0 - 1 * DS Stalkonstruktion * A s 1 8 *			
PROJECT	Akkasæter Lager- og vedlikeholdshall	EXEC. CLASS	EXC 2
MEMBER	Søyle	QUANTITY:	1
REVISION	ISSUED: 07.11.2025	DRAFTER: ZLL	PROJECT No 30480-1
	BIM control: SST		DRAWING No. s.18