
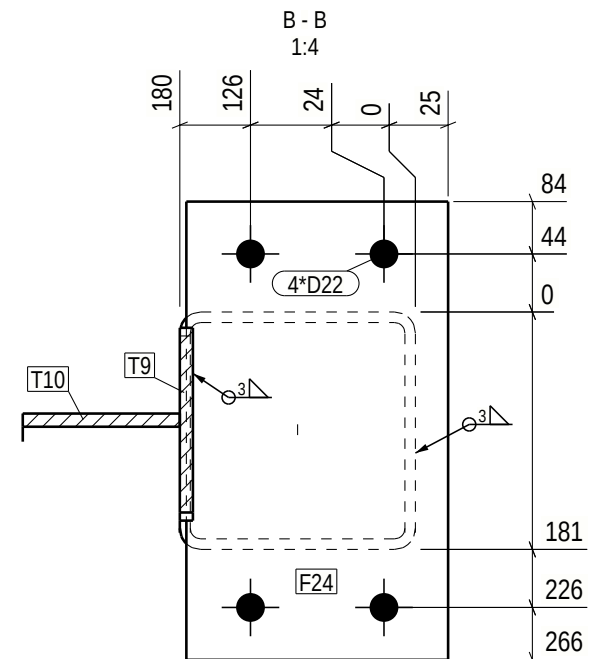
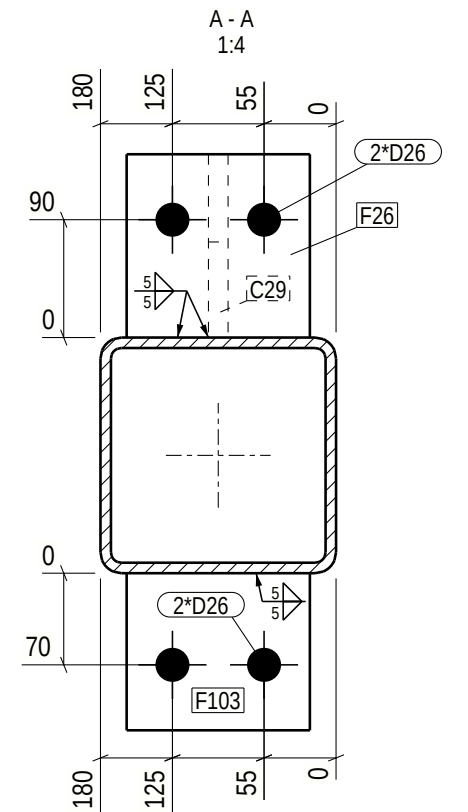


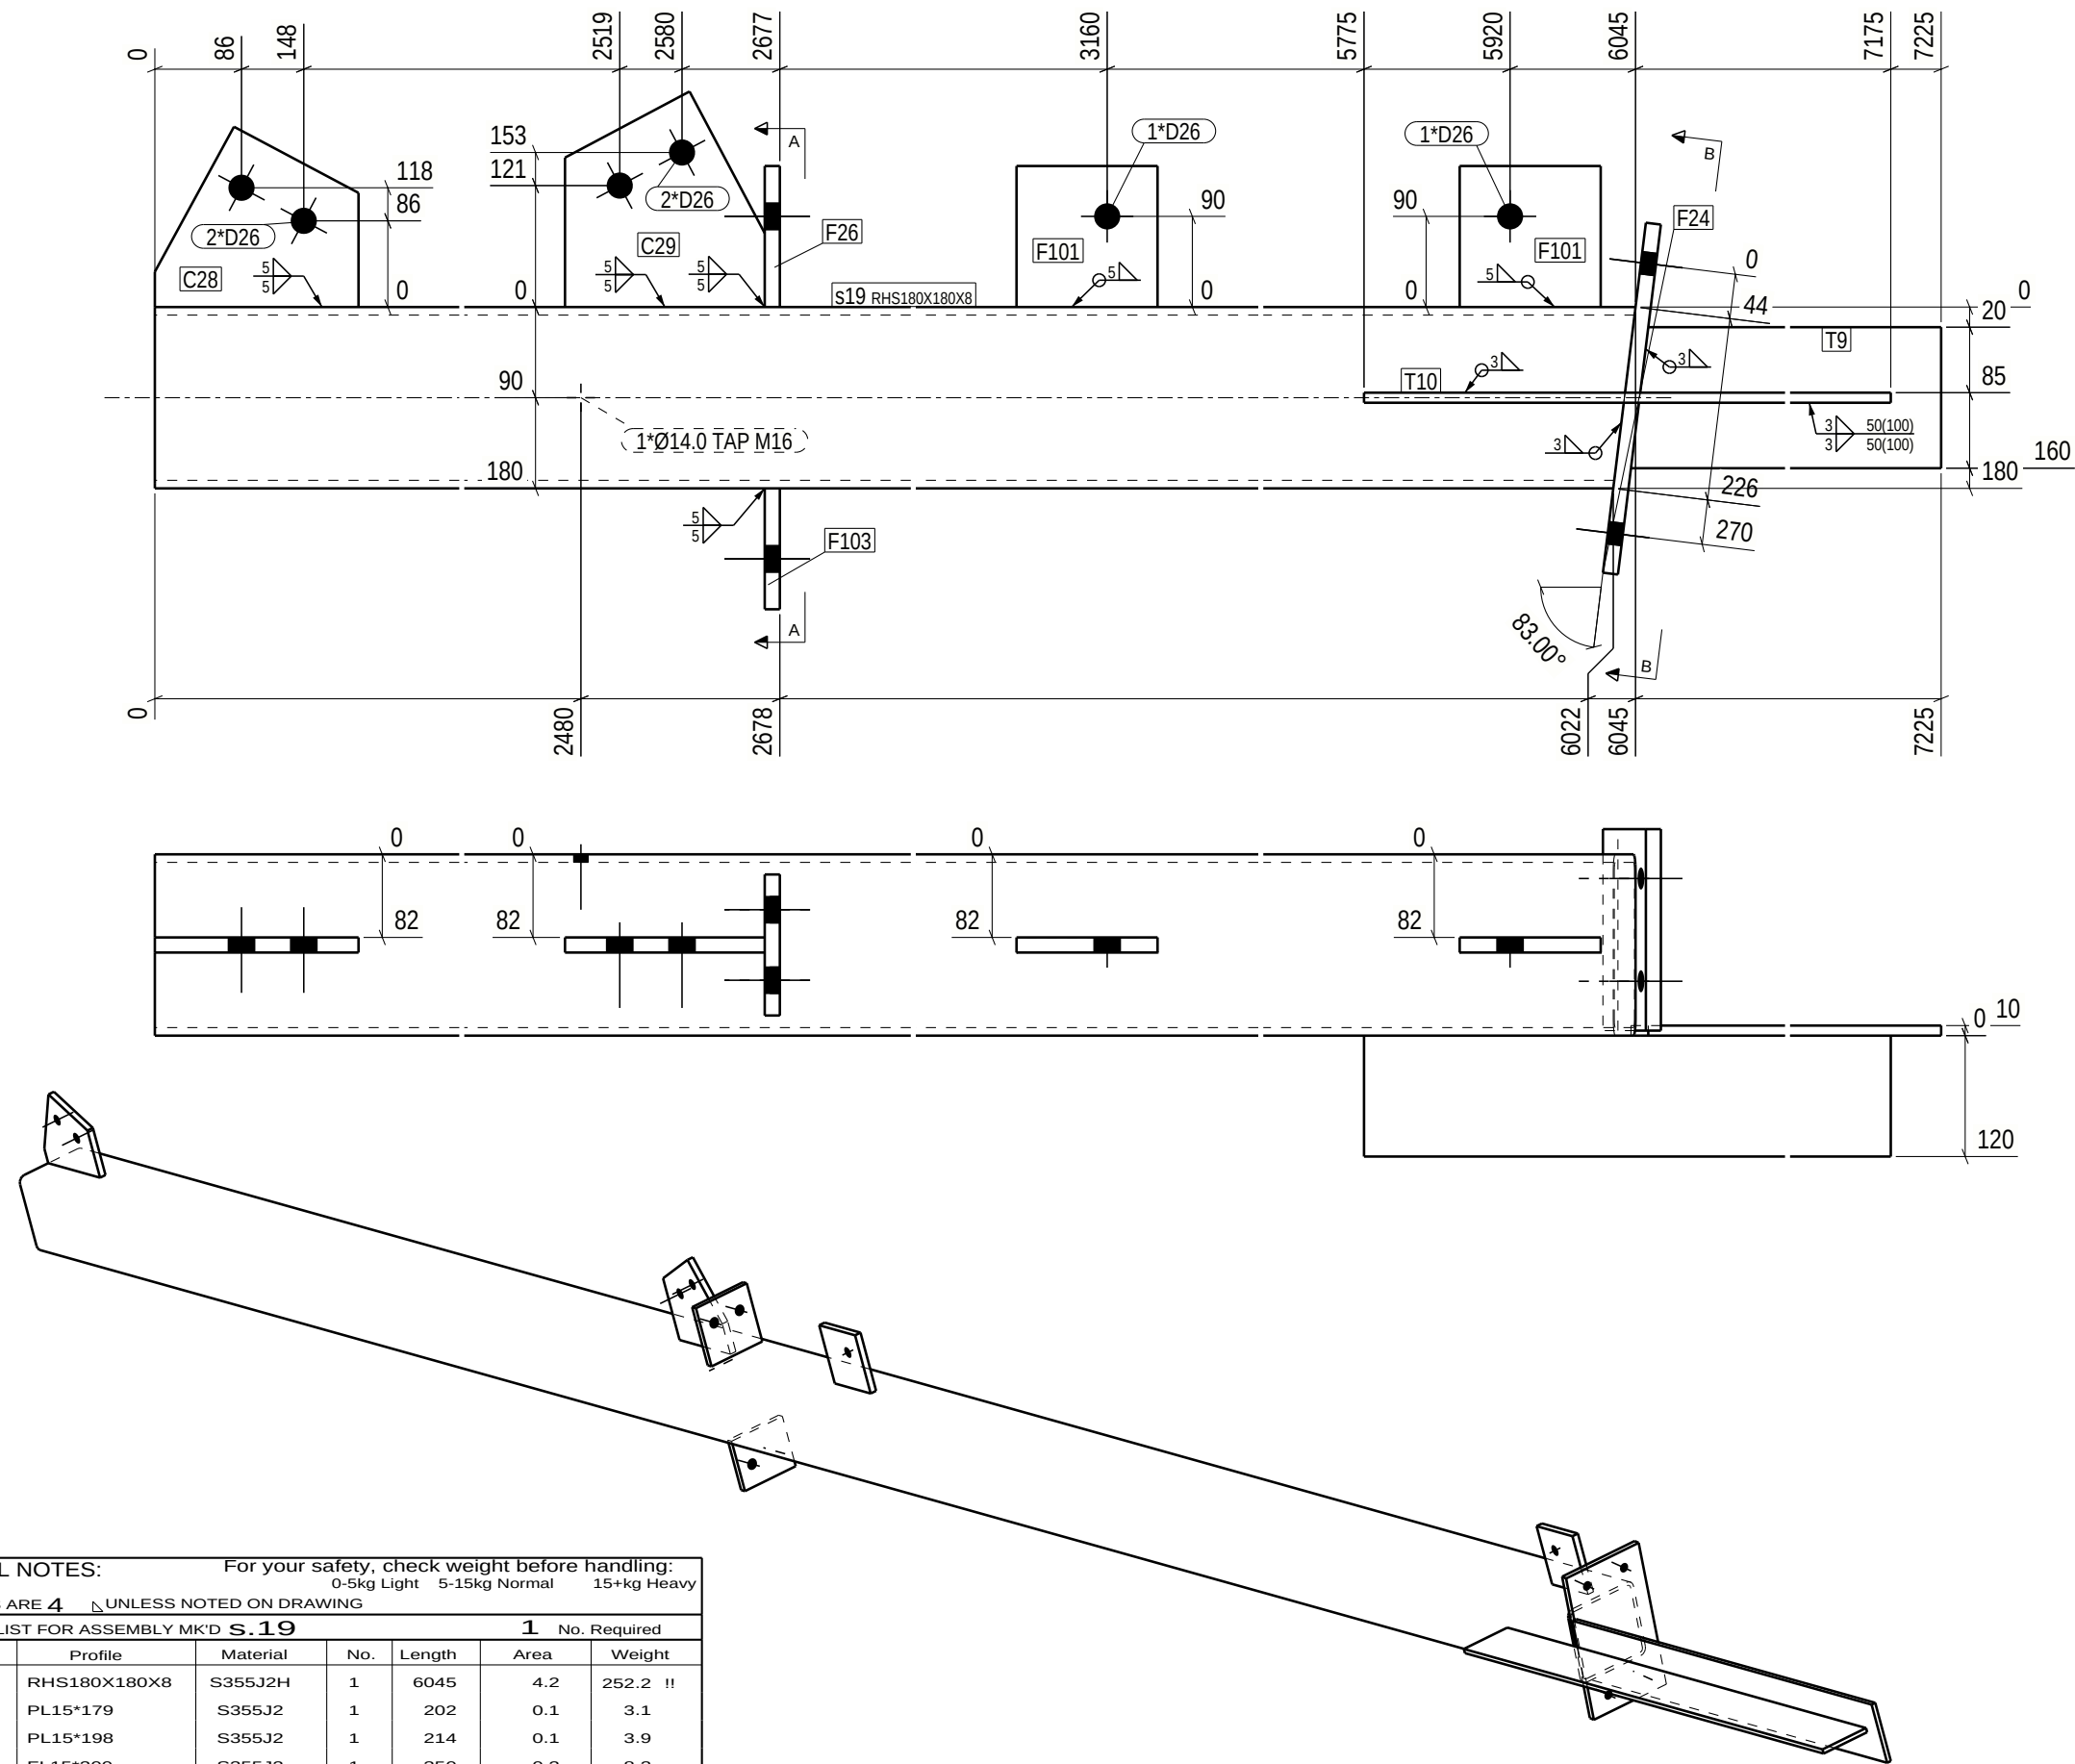

GENERAL NOTES: For your safety, check weight before handling:
0-5kg Light 5-15kg Normal 15+kg Heavy

ALL WELDS ARE 4 UNLESS NOTED ON DRAWING

MATERIAL LIST FOR ASSEMBLY MK'D **s.19** 1 No. Required

Mark	Profile	Material	No.	Length	Area	Weight
S19	RHS180X180X8	S355J2H	1	6045	4.2	252.2 !!
C28	PL15*179	S355J2	1	202	0.1	3.1
C29	PL15*198	S355J2	1	214	0.1	3.9
F24	FL15*200	S355J2	1	350	0.2	8.2
F26	FL15*140	S355J2	1	140	0.0	2.3
F101	FL15*140	S355J2	2	140	0.0	2.3
F103	FL15*120	S355J2	1	140	0.0	2.0
T9	FL10*140	S355J2	1	1185	0.4	12.9
T10	FL10*120	S355J2	1	1400	0.4	13.2
Total					5.4	302.4

Finish Class
Standard

Surface treatment info: Thickness/start point-> length No.
Overall Painting C2M RAL7016µm whole***1



Special
surface treatment



weld a = 4

PHASE	QUANTITY
1	1

* o 3 0 4 8 0 - 1 *  DS <i>Stålkonstruktion</i> * A s 1 9 *			
PROJECT	Akkasæter Lager- og vedlikeholdshall	EXEC. CLASS	EXC 2
MEMBER	Søyle	QUANTITY:	1
REVISION	ISSUED: 07.11.2025	DRAFTER: ZLL	PROJECT No 30480-1
	BIM control: SST		DRAWING No. s.19