

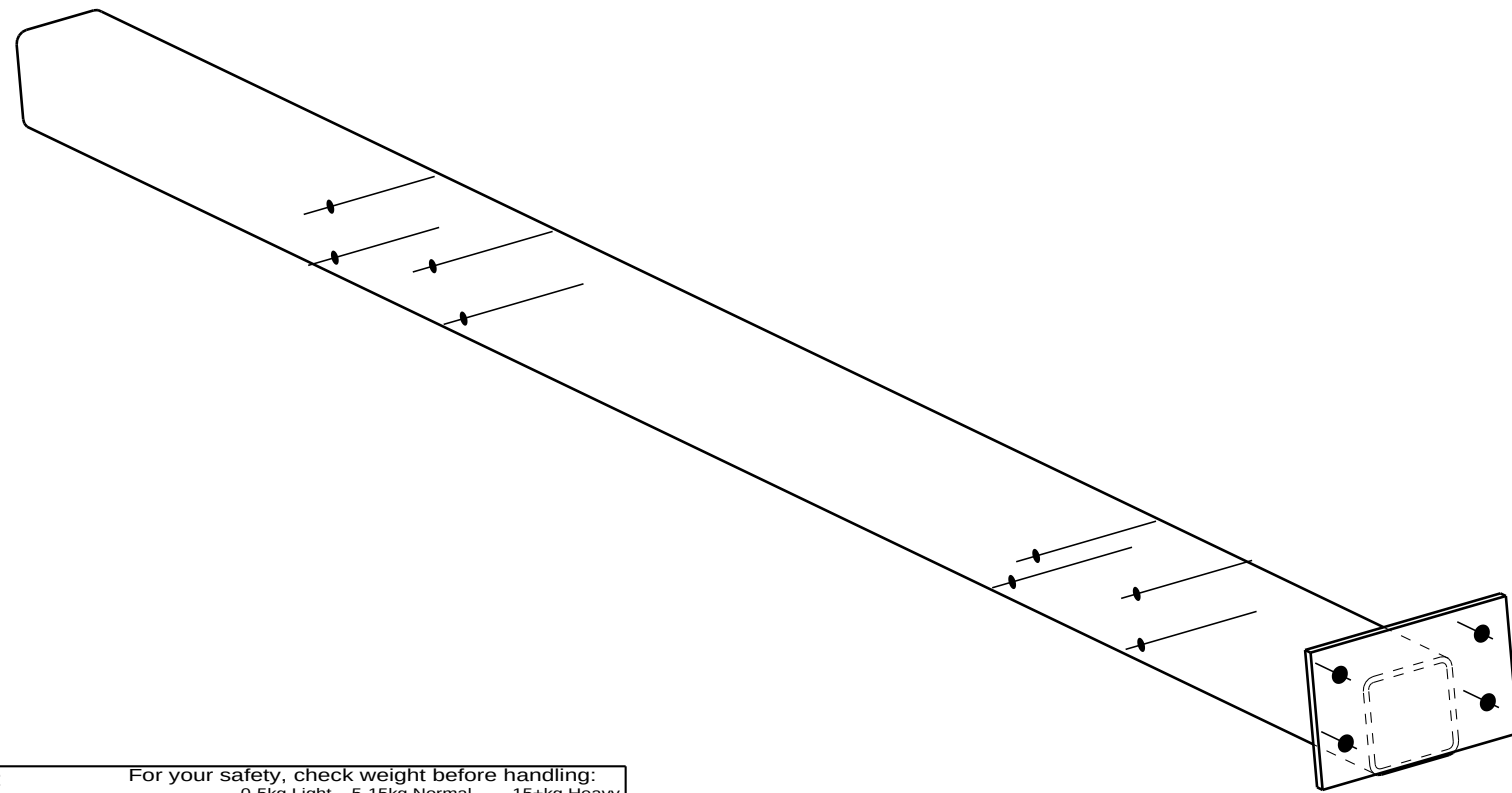
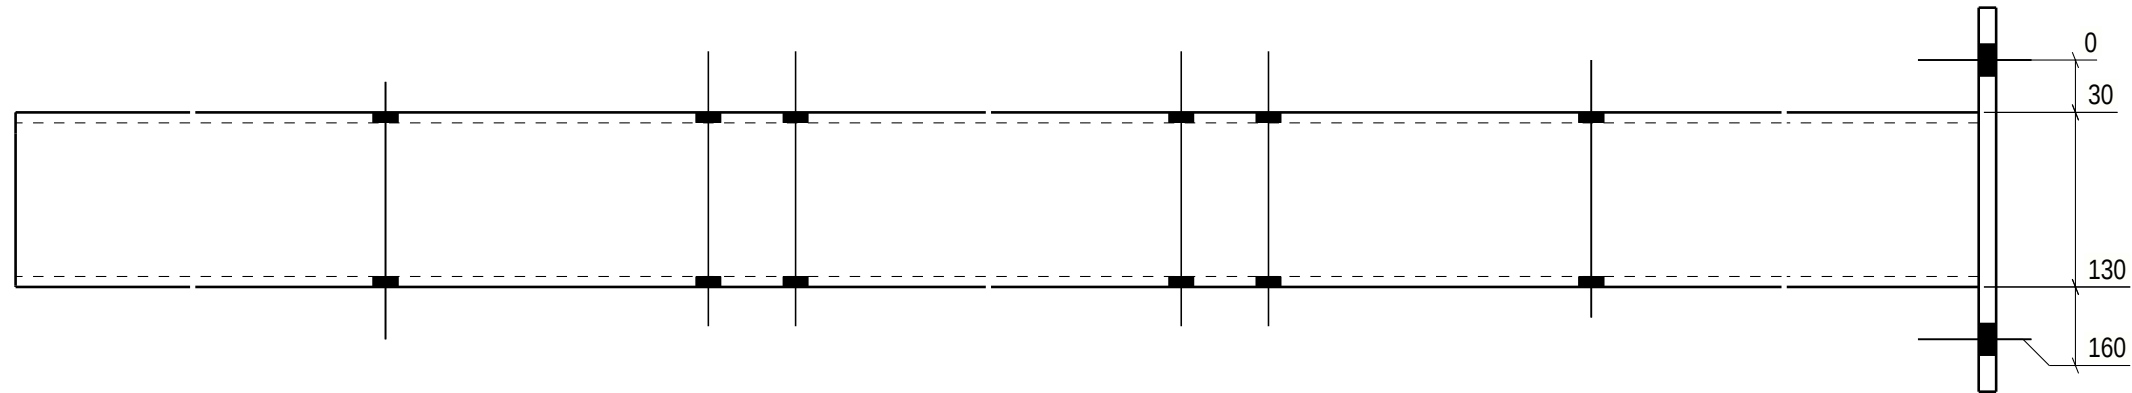


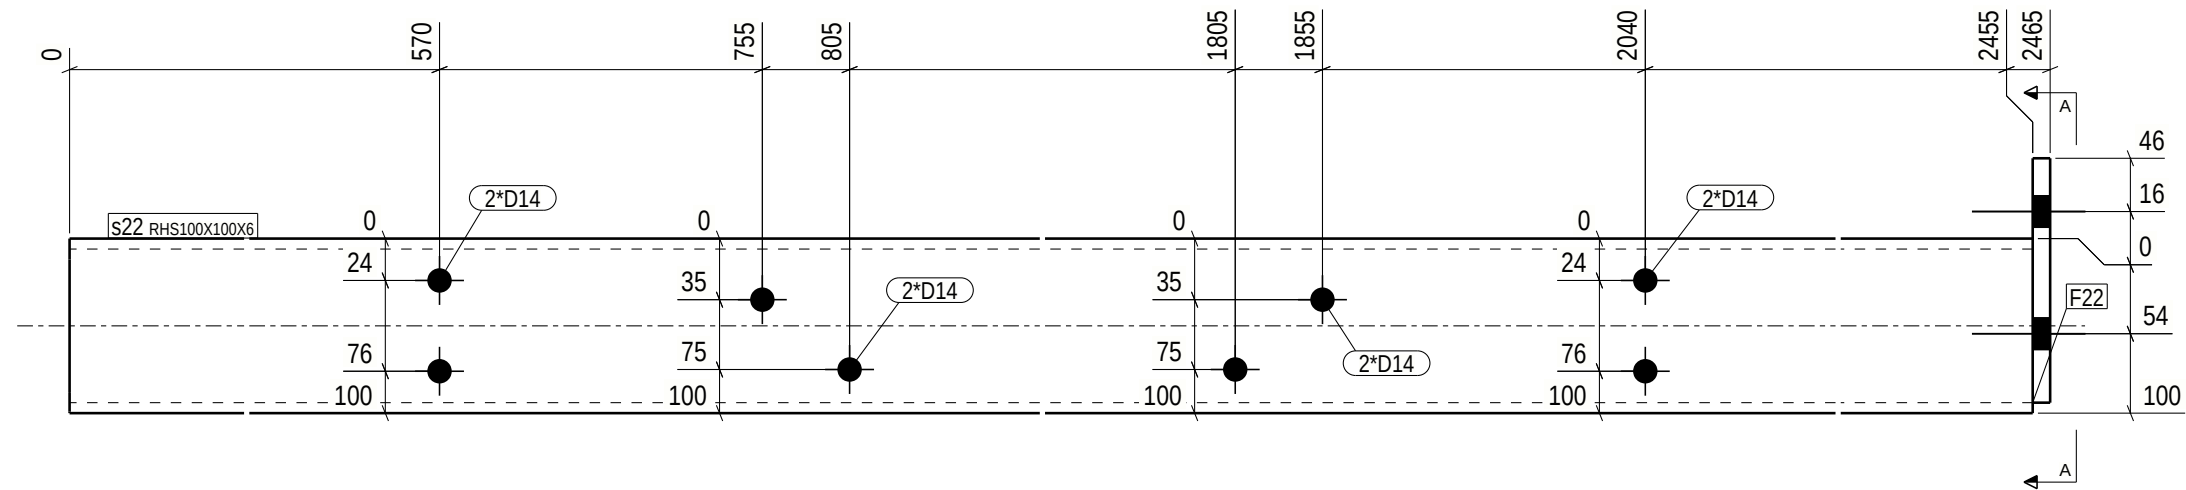

A - A
1:2

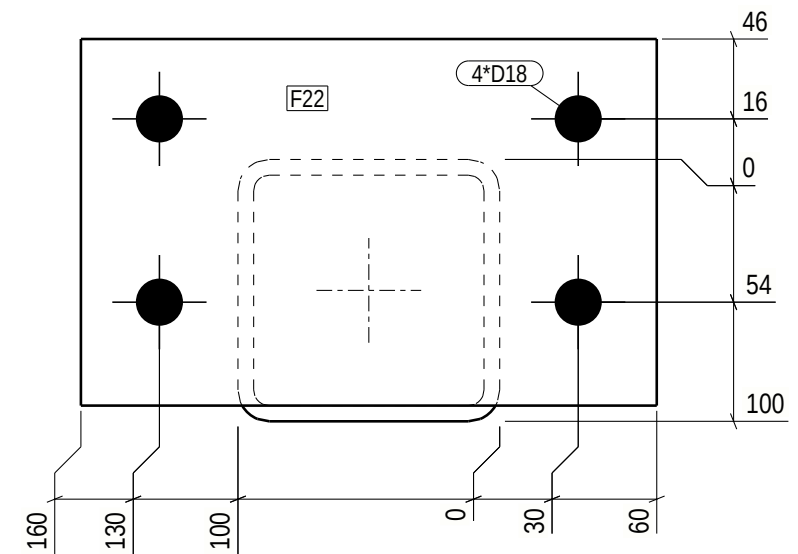

GENERAL NOTES:						
For your safety, check weight before handling:						
0-5kg Light 5-15kg Normal 15+kg Heavy						
ALL WELDS ARE 4 UNLESS NOTED ON DRAWING						
MATERIAL LIST FOR ASSEMBLY MK'D S.22						
Mark	Profile	Material	No.	Length	Area	Weight
S22	RHS100X100X6	S355J2H	1	2455	0.9	41.5 !!
F22	FL10*140	S355J2	1	220	0.1	2.4
Total				1.0	43.9	

Finish Class
Standard

Surface treatment info:	Thickness/start point-> length	No.
Overall Painting	C2M RAL7016µm whole**2	



Special
surface treatment



weld a = 4

PHASE	QUANTITY
1	2

* o 3 0 4 8 0 - 1 * DS Skalkonstruktion * A s 2 2 *			
PROJECT	Akkasæter Lager- og vedlikeholdshall	EXEC. CLASS	EXC 2
MEMBER	Søyle	QUANTITY:	2
REVISION	ISSUED: 07.11.2025	DRAFTER:	ZLL
		BIM control:	SST
PROJECT No		30480-1	
DRAWING No.		s.22	