


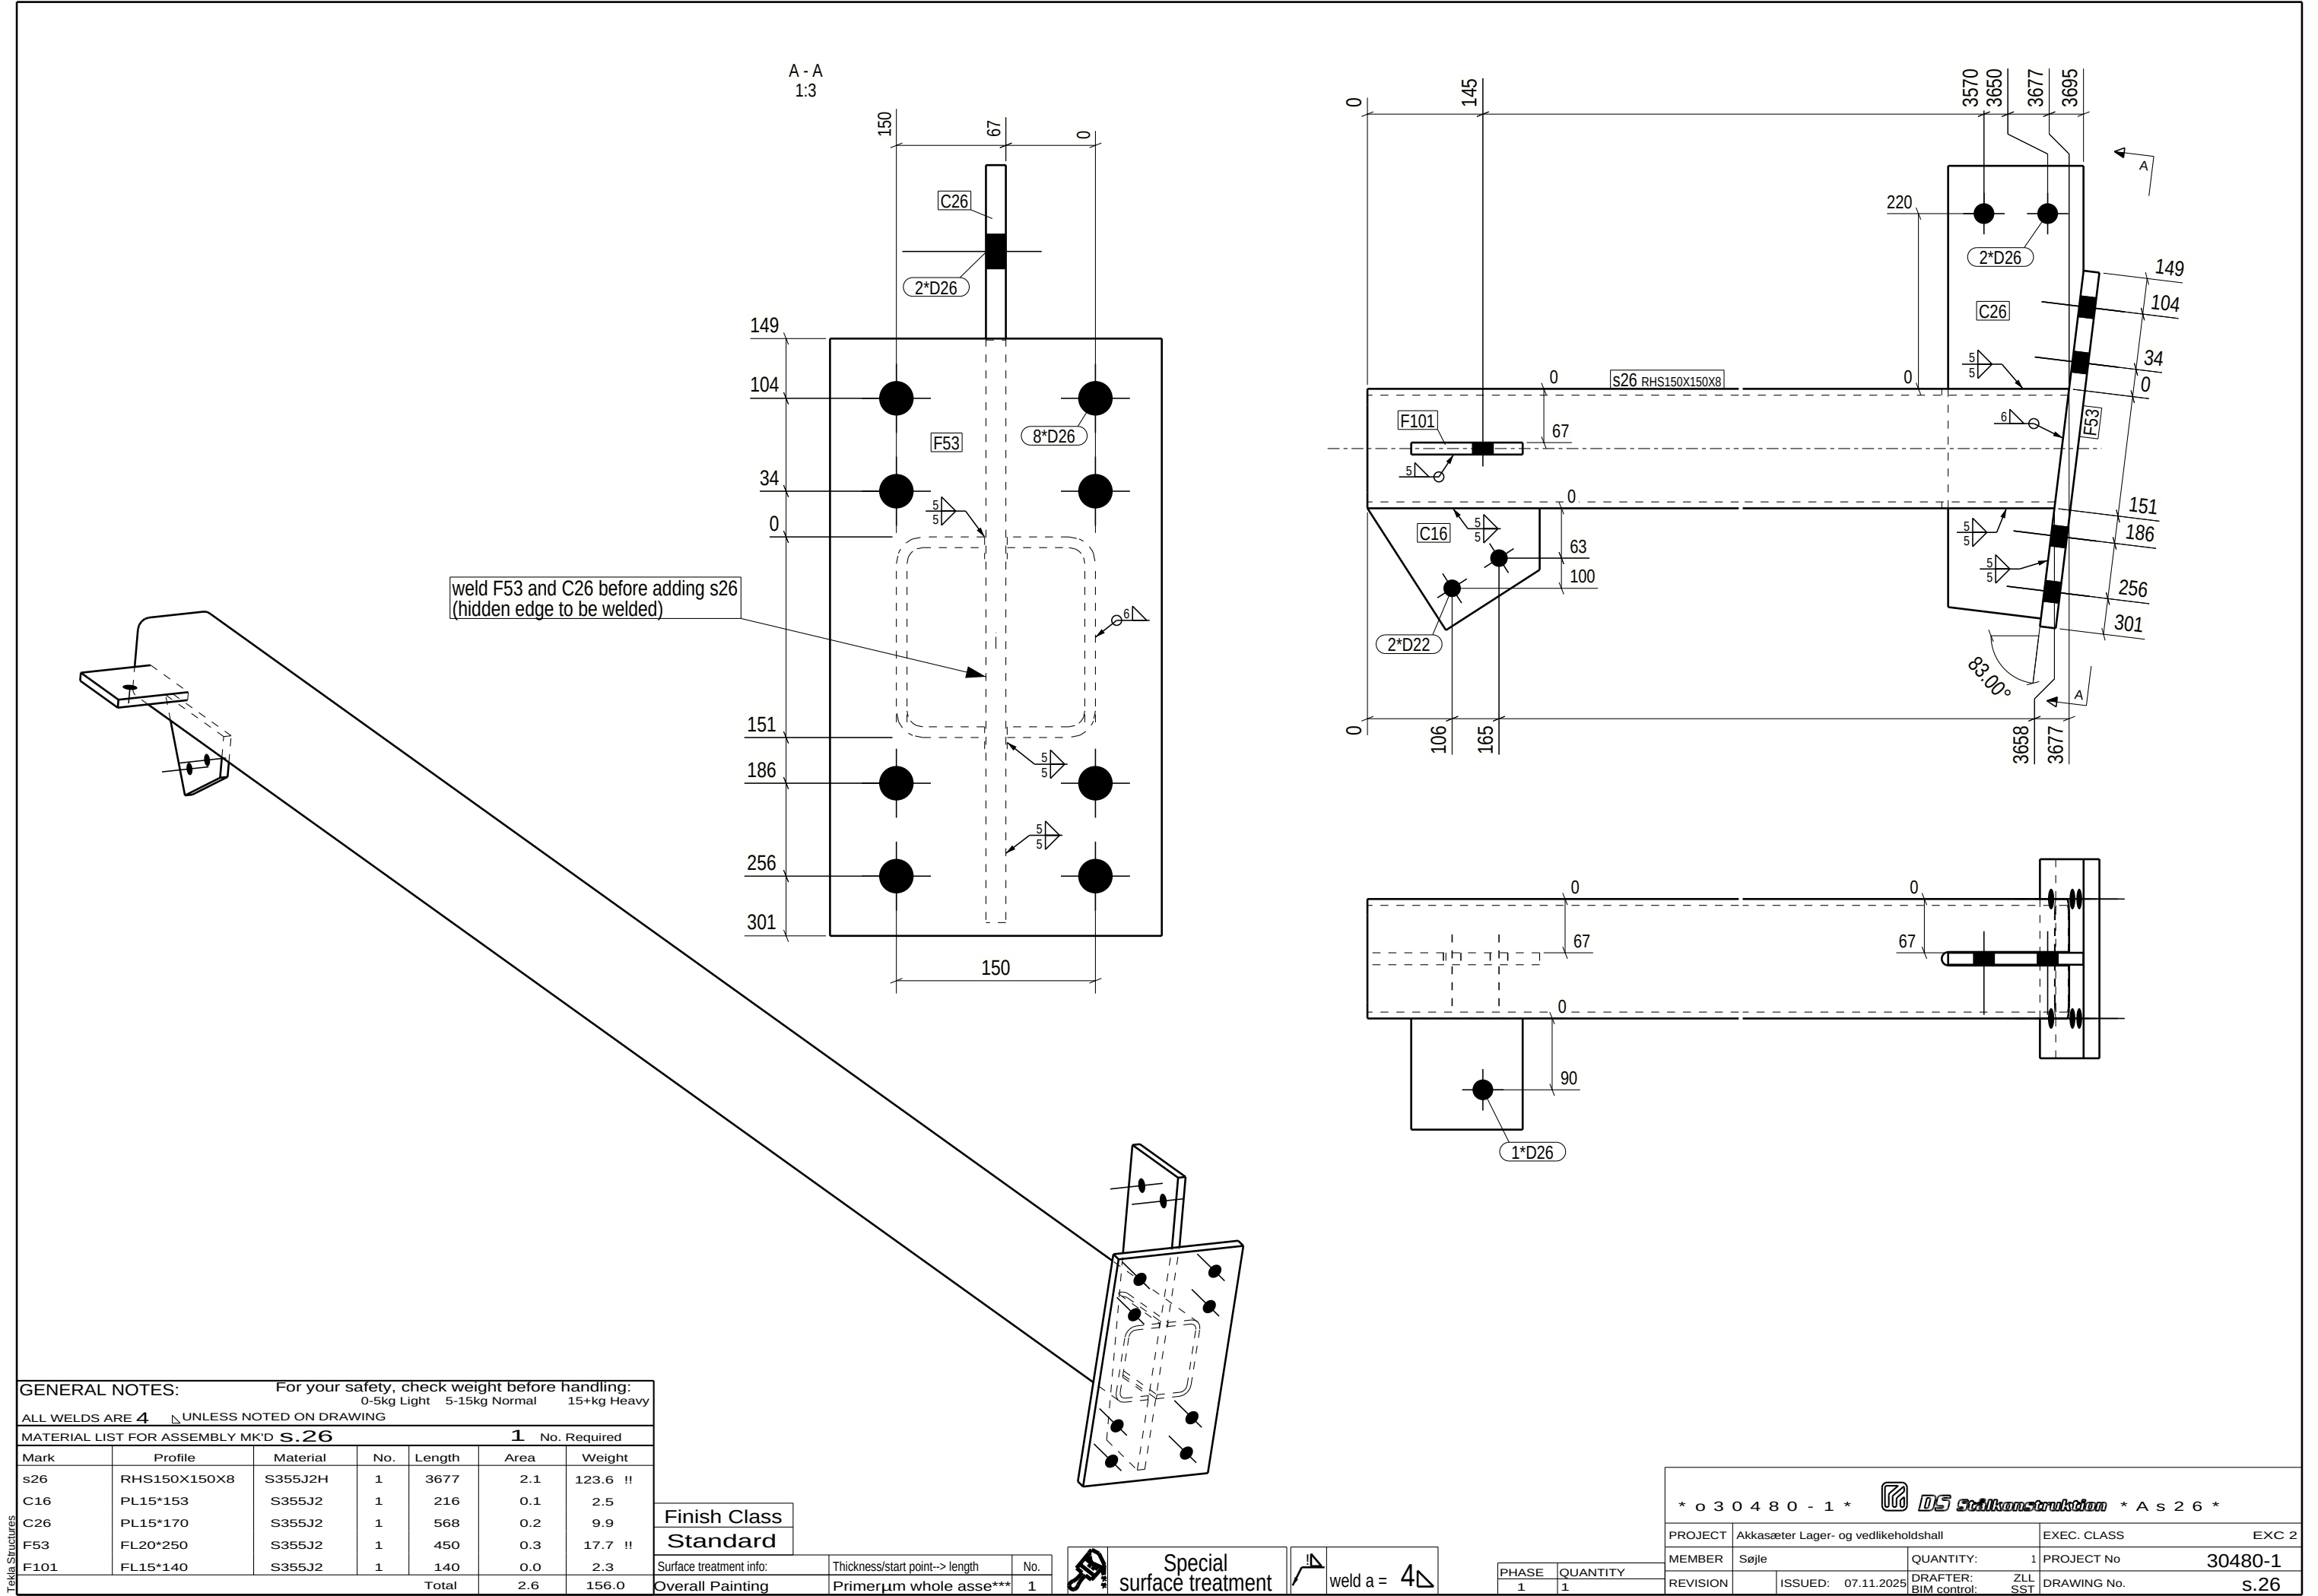

GENERAL NOTES: For your safety, check weight before handling:
0-5kg Light 5-15kg Normal 15+kg Heavy

ALL WELDS ARE 4 UNLESS NOTED ON DRAWING

Mark	Profile	Material	No.	Length	Area	Weight
s26	RHS150X150X8	S355J2H	1	3677	2.1	123.6 !!
C16	PL15*153	S355J2	1	216	0.1	2.5
C26	PL15*170	S355J2	1	568	0.2	9.9
F53	FL20*250	S355J2	1	450	0.3	17.7 !!
F101	FL15*140	S355J2	1	140	0.0	2.3
Total					2.6	156.0

Finish Class
Standard

Surface treatment info:	Thickness/start point--> length	No.
Overall Painting	Primerµm whole asse***	1

Special
surface treatment

weld a = 4

PHASE	QUANTITY
1	1

* o 3 0 4 8 0 - 1 * DS Skalkonstruktion * A s 2 6 *			
PROJECT	Akkasæter Lager- og vedlikeholdshall	EXEC. CLASS	EXC 2
MEMBER	Søyle	QUANTITY:	1
REVISION	ISSUED: 07.11.2025	DRAFTER: ZLL SST	PROJECT No 30480-1
			DRAWING No. s.26