
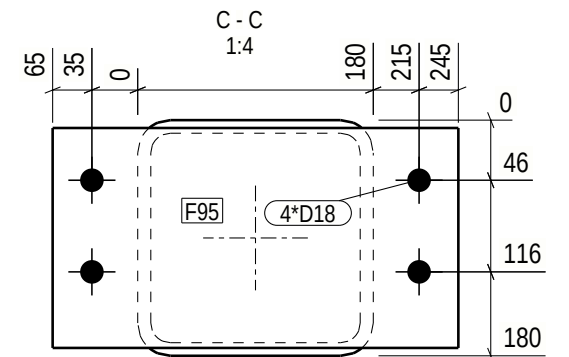
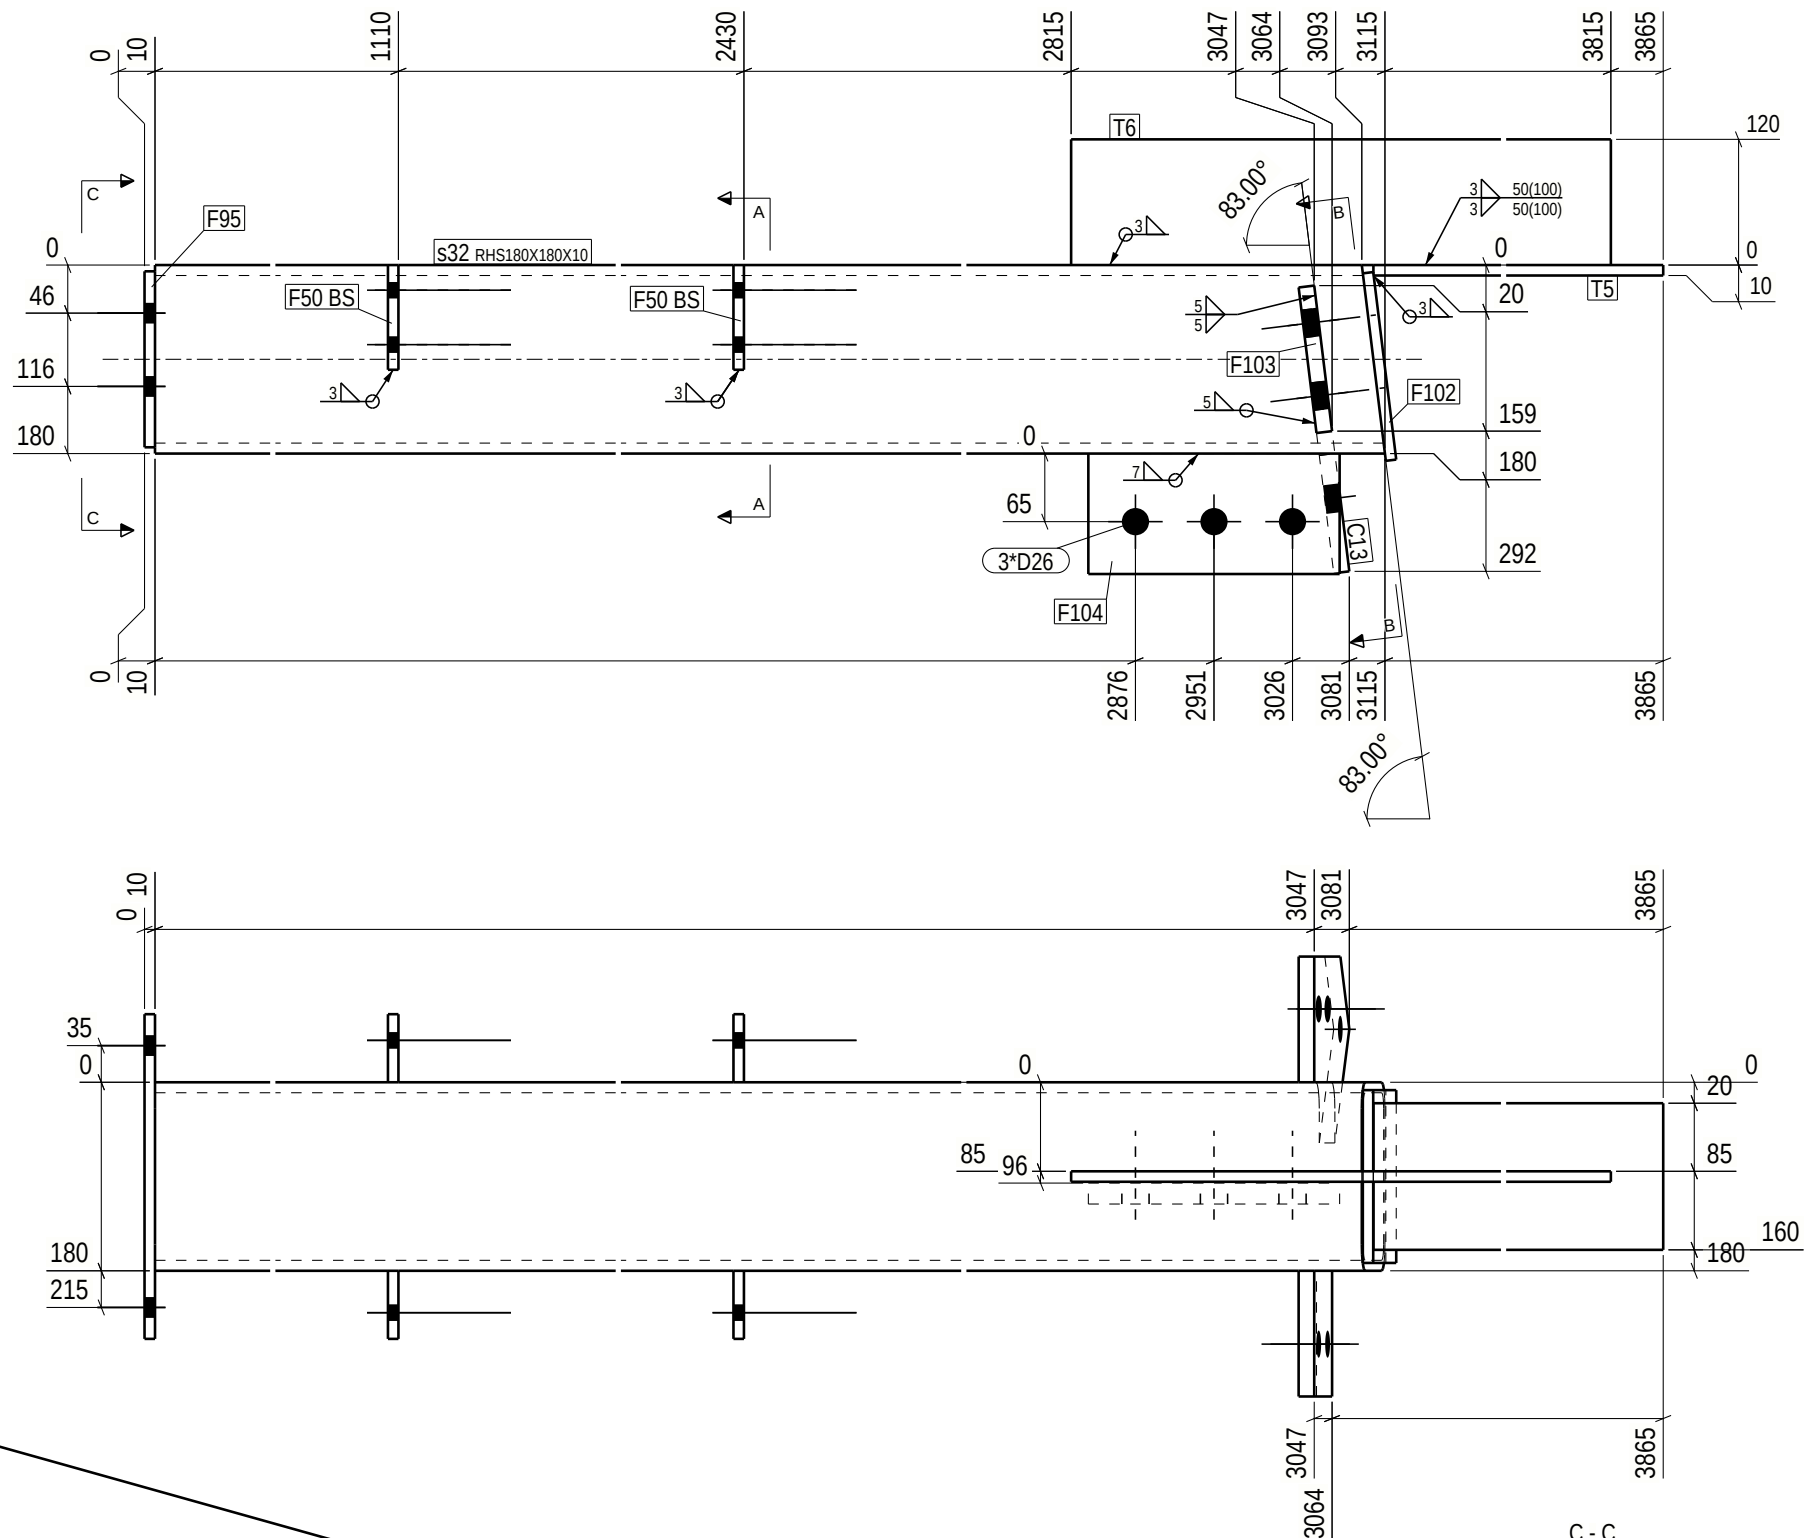
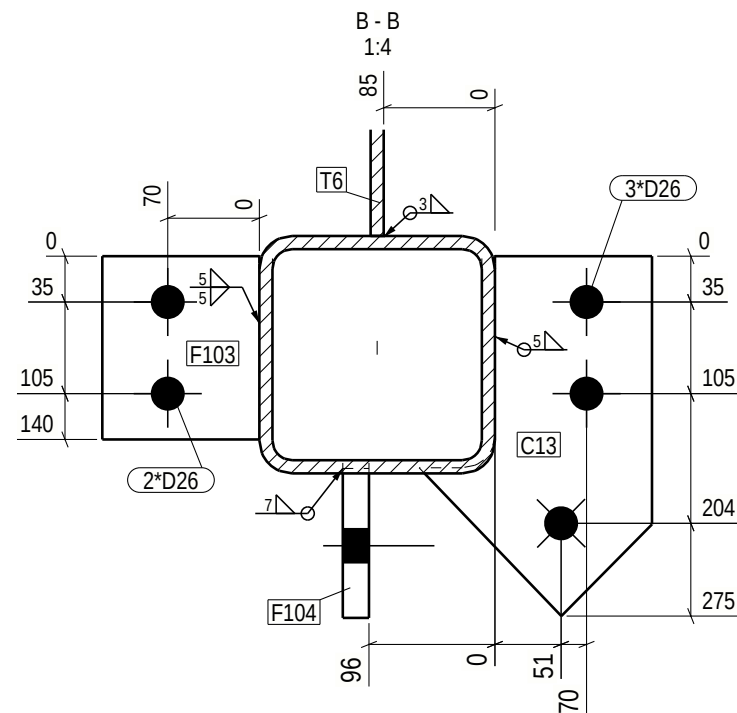


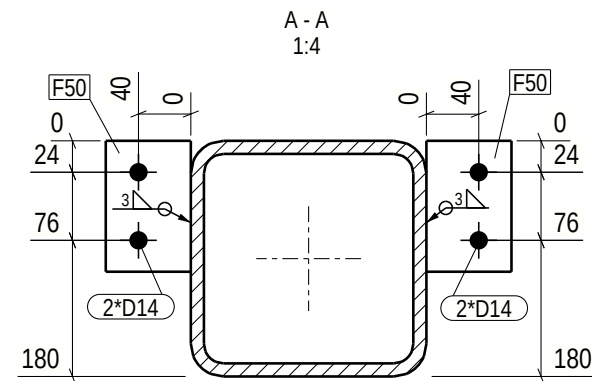

GENERAL NOTES: For your safety, check weight before handling:
0-5kg Light 5-15kg Normal 15+kg Heavy

ALL WELDS ARE 4 UNLESS NOTED ON DRAWING

MATERIAL LIST FOR ASSEMBLY MK'D **s.32** 1 No. Required

Mark	Profile	Material	No.	Length	Area	Weight
S32	RHS180X180X10	S355J2H	1	3105	2.1	156.0 !!
C13	PL15*178	S355J2	1	275	0.1	3.7
F50	FL10*65	S355J2	4	100	0.0	0.5
F95	FL10*168	S355J2	1	310	0.1	4.1
F102	FL10*165	S355J2	1	180	0.1	2.3
F103	FL15*120	S355J2	1	140	0.0	2.0
F104	FL20*115	S355J2	1	240	0.1	4.3
T5	FL10*140	S355J2	1	761	0.2	8.4
T6	FL10*120	S355J2	1	1000	0.3	9.4
Total					3.0	192.3

Finish Class
Standard

Surface treatment info: Thickness/start point-> length No.
Overall Painting C2M RAL7016µm whole***1



Special
surface treatment



weld a = 4

PHASE	QUANTITY
1	1

* o 3 0 4 8 0 - 1 * **DS** *Stålkonstruktion* * A s 3 2 *

PROJECT	Akkasæter Lager- og vedlikeholdshall	EXEC. CLASS	EXC 2
MEMBER	Søyle	QUANTITY:	1
REVISION	ISSUED: 07.11.2025	DRAFTER: ZLL	PROJECT No 30480-1
	BIM control: SST		DRAWING No. s.32