
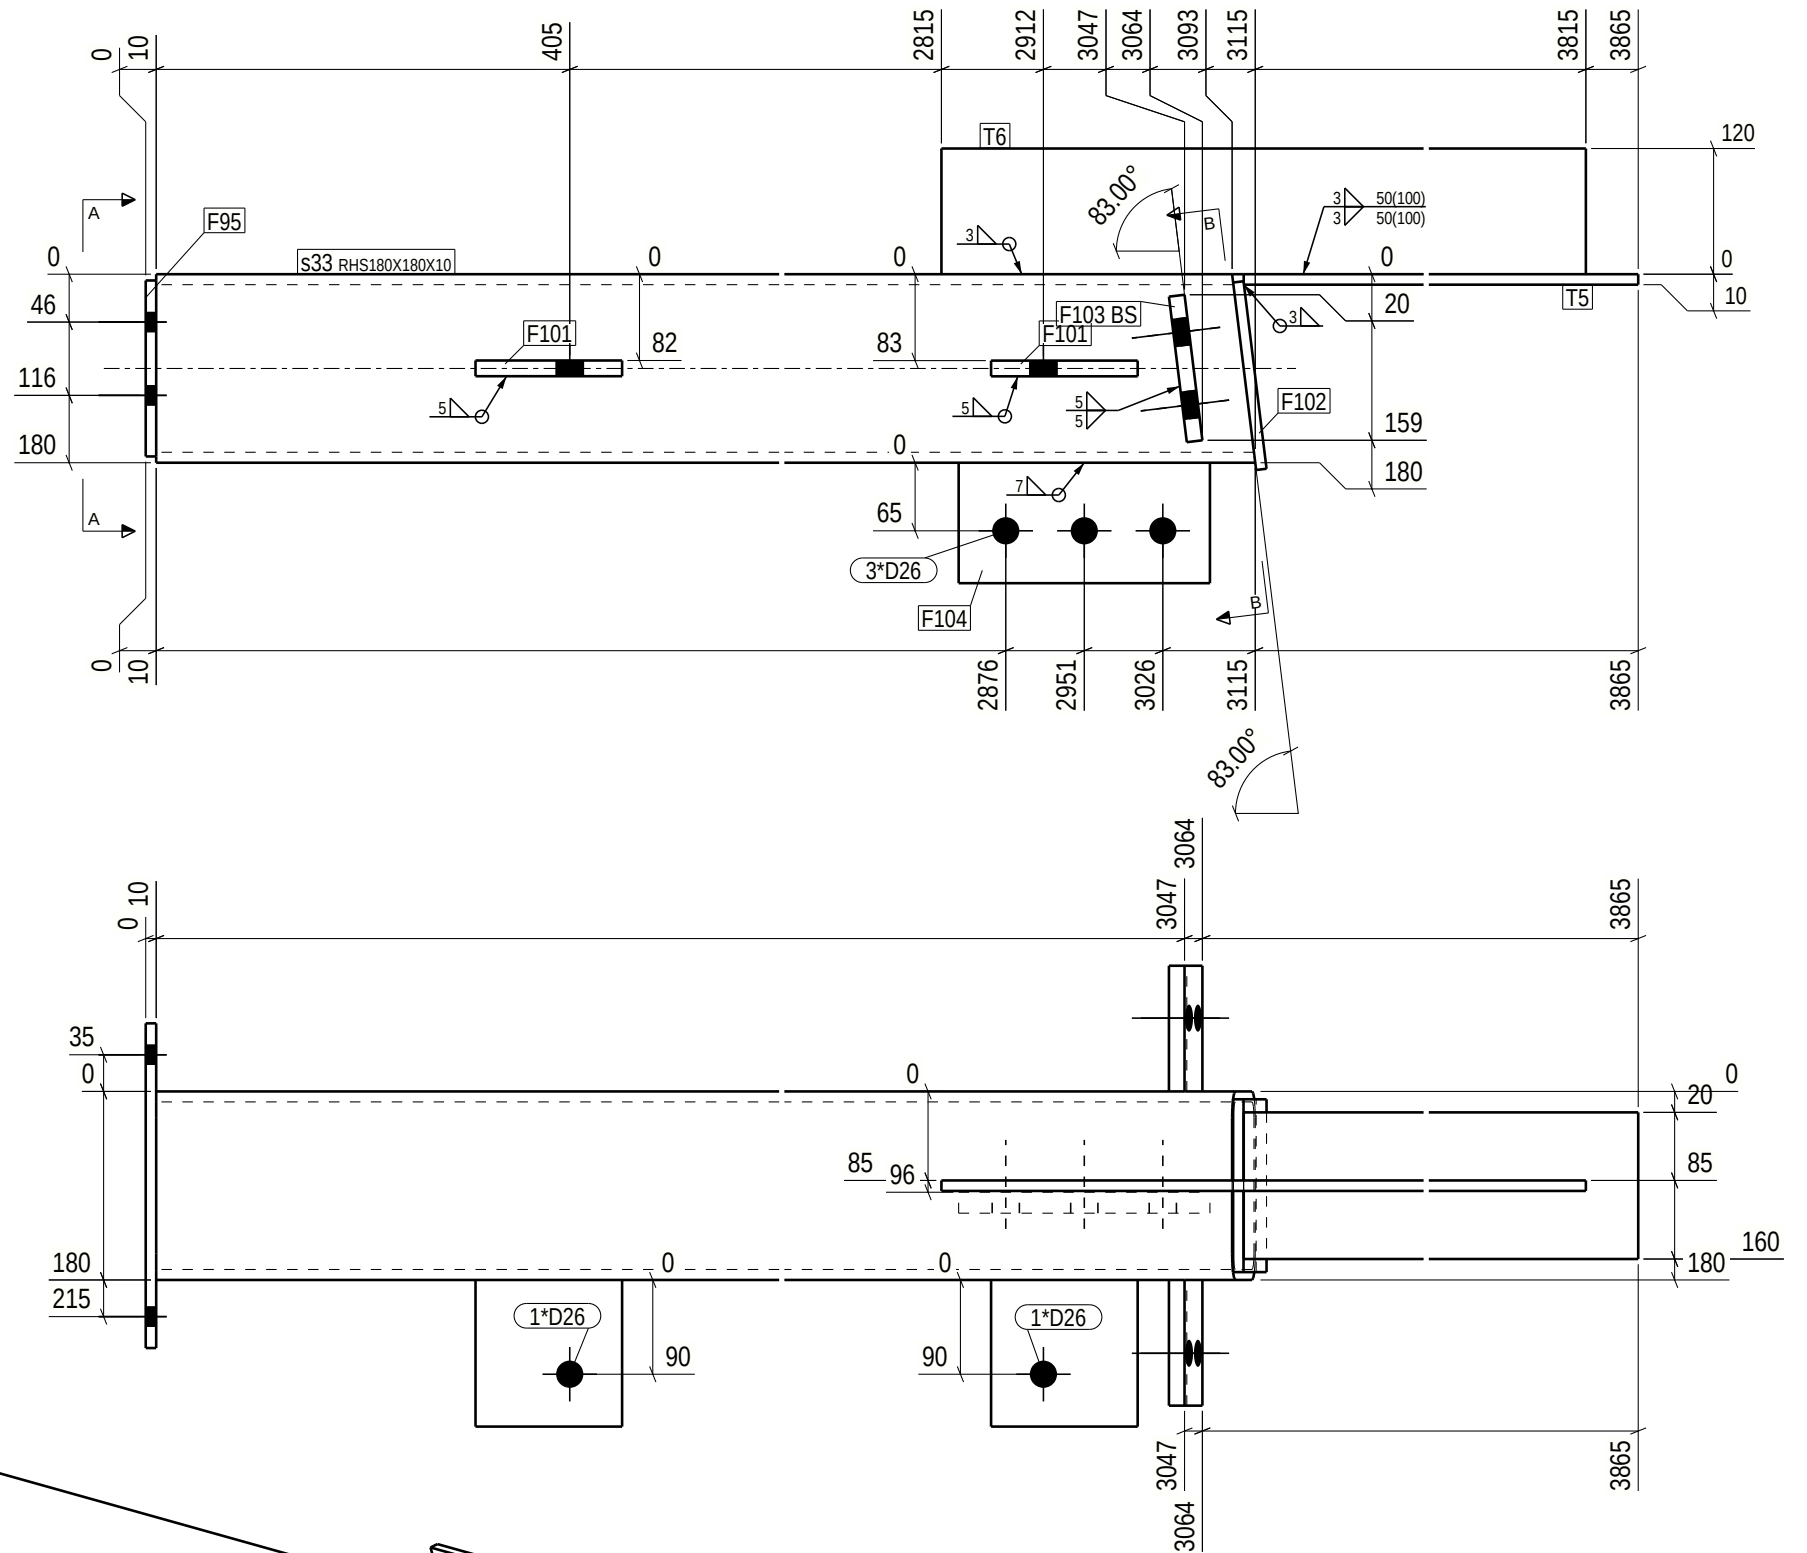
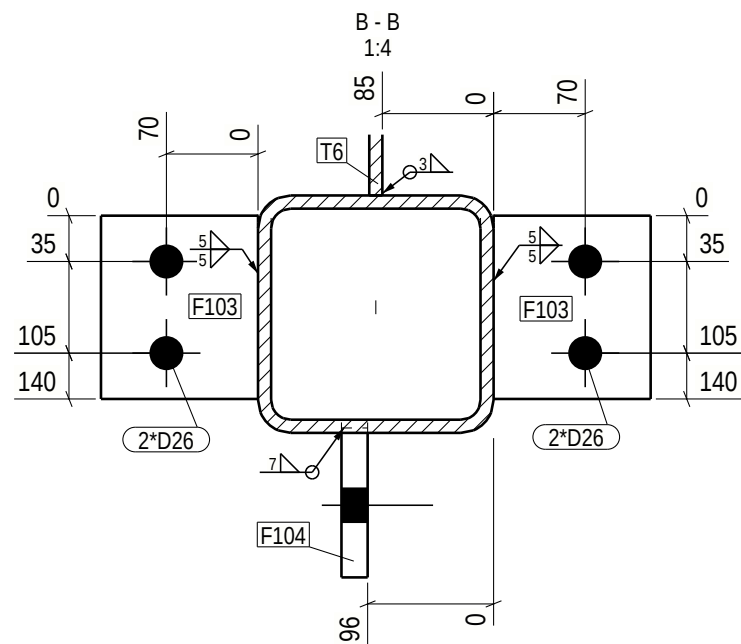


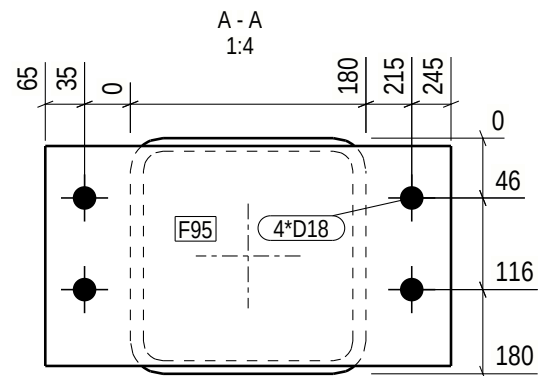

GENERAL NOTES: For your safety, check weight before handling:

ALL WELDS ARE 4 UNLESS NOTED ON DRAWING

MATERIAL LIST FOR ASSEMBLY MK'D S.33 1 No. Required

Mark	Profile	Material	No.	Length	Area	Weight
s33	RHS180X180X10	S355J2H	1	3105	2.1	156.0 !!
F95	FL10*168	S355J2	1	310	0.1	4.1
F101	FL15*140	S355J2	2	140	0.0	2.3
F102	FL10*165	S355J2	1	180	0.1	2.3
F103	FL15*120	S355J2	2	140	0.0	2.0
F104	FL20*115	S355J2	1	240	0.1	4.3
T5	FL10*140	S355J2	1	761	0.2	8.4
T6	FL10*120	S355J2	1	1000	0.3	9.4
Total					3.0	193.1

Finish Class
Standard

Surface treatment info:	Thickness/start point-> length	No.
Overall Painting	C2M RAL7016µm whole	**1

Special surface treatment
weld a = 4

PHASE	QUANTITY
1	1

* o 3 0 4 8 0 - 1 * DS Stalkonstruktion * A s 3 3 *			
PROJECT	Akkasæter Lager- og vedlikeholdshall	EXEC. CLASS	EXC 2
MEMBER	Søyle	QUANTITY:	1 PROJECT No 30480-1
REVISION	ISSUED: 07.11.2025	DRAFTER: ZLL SST	DRAWING No. s.33