
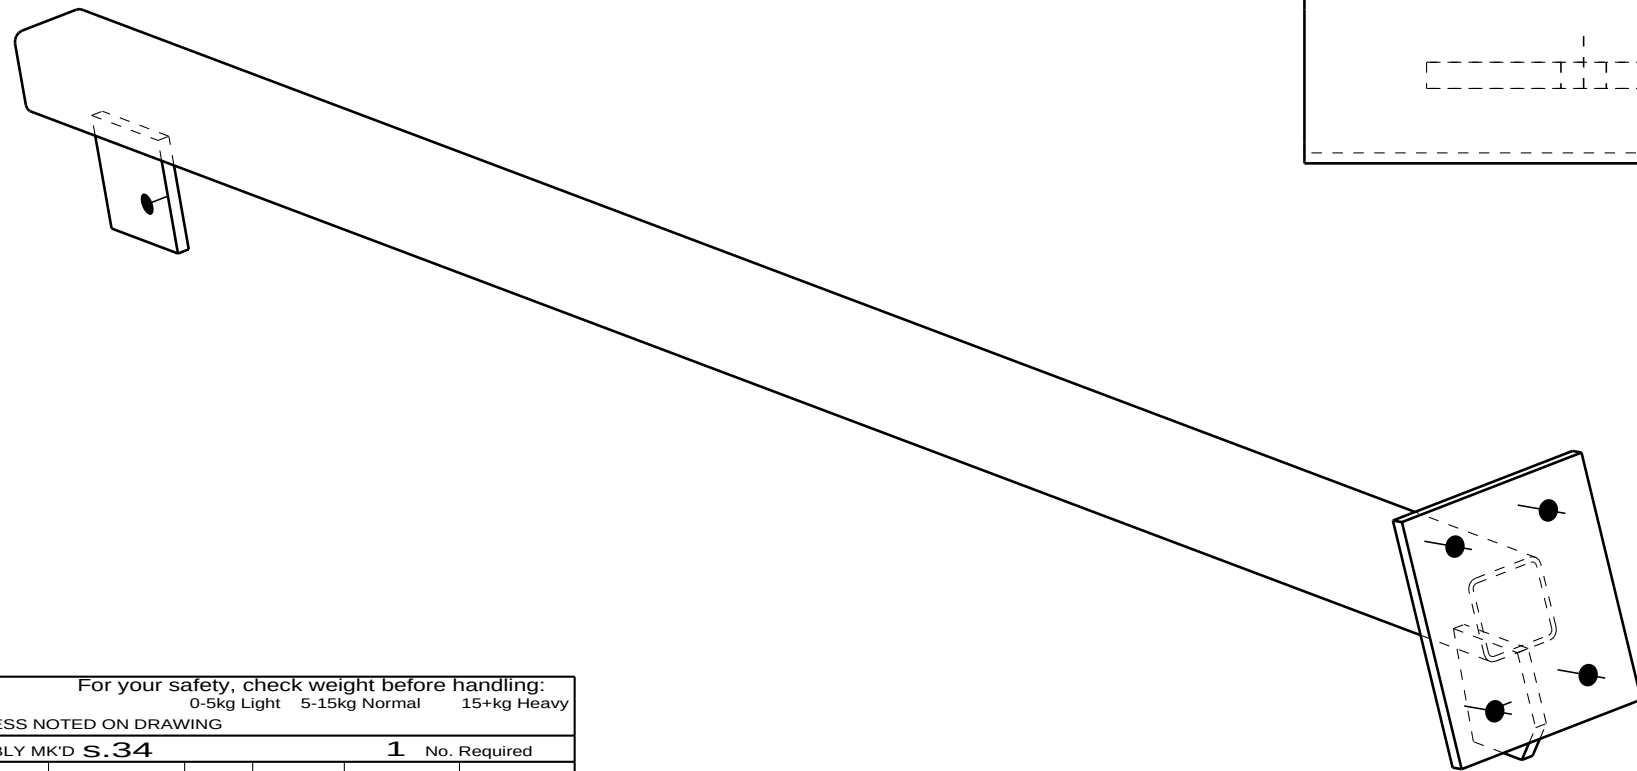
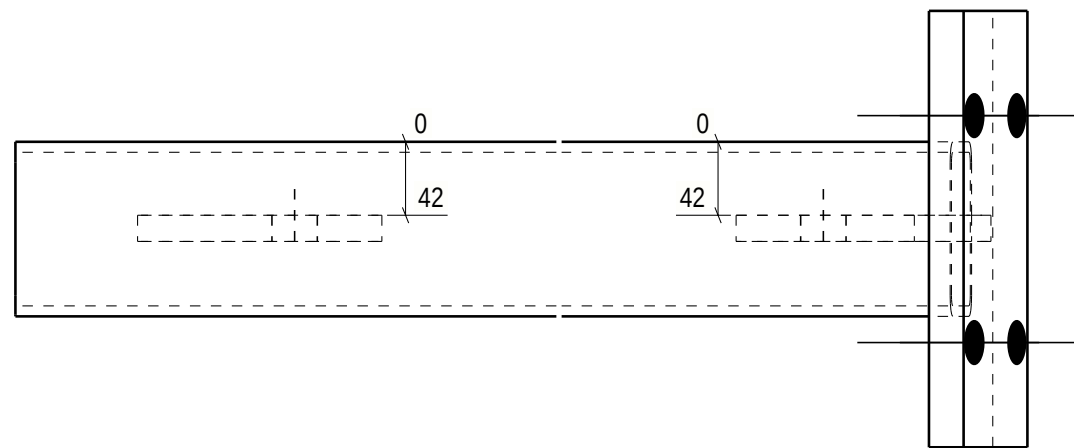
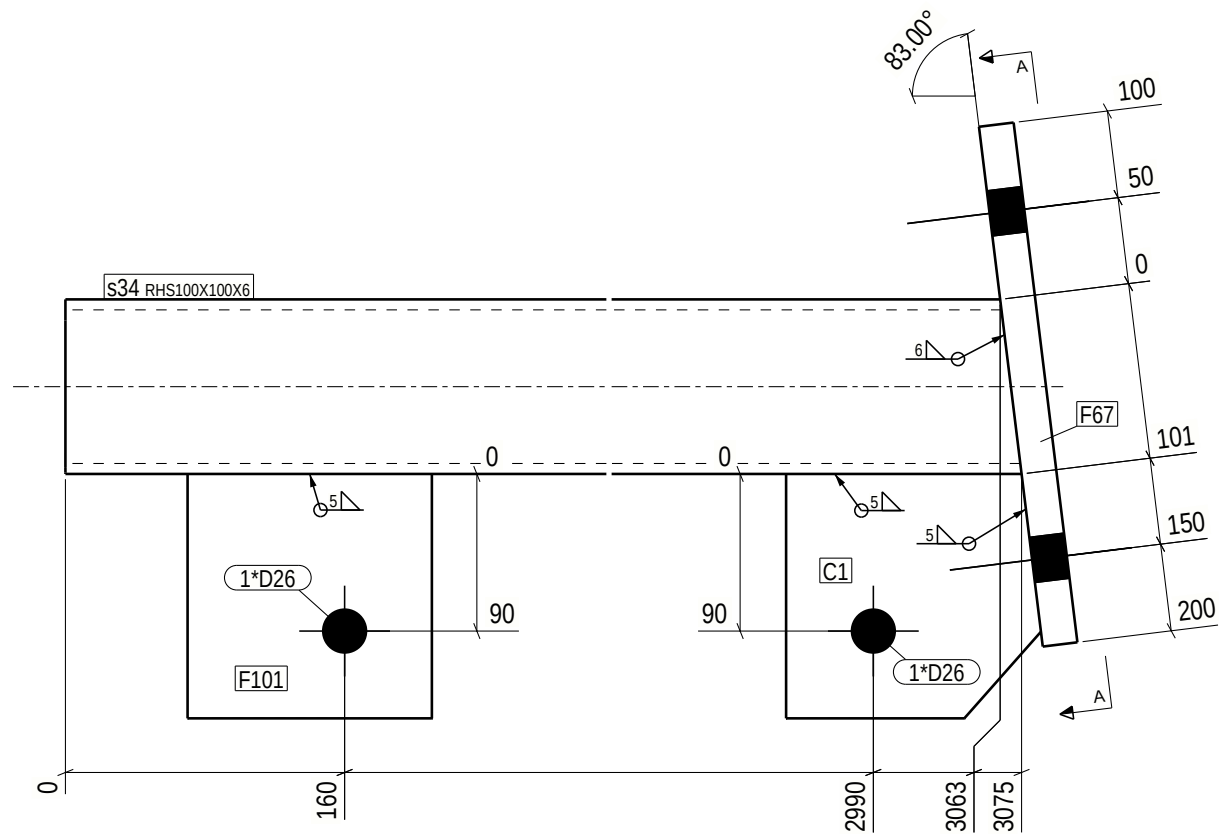


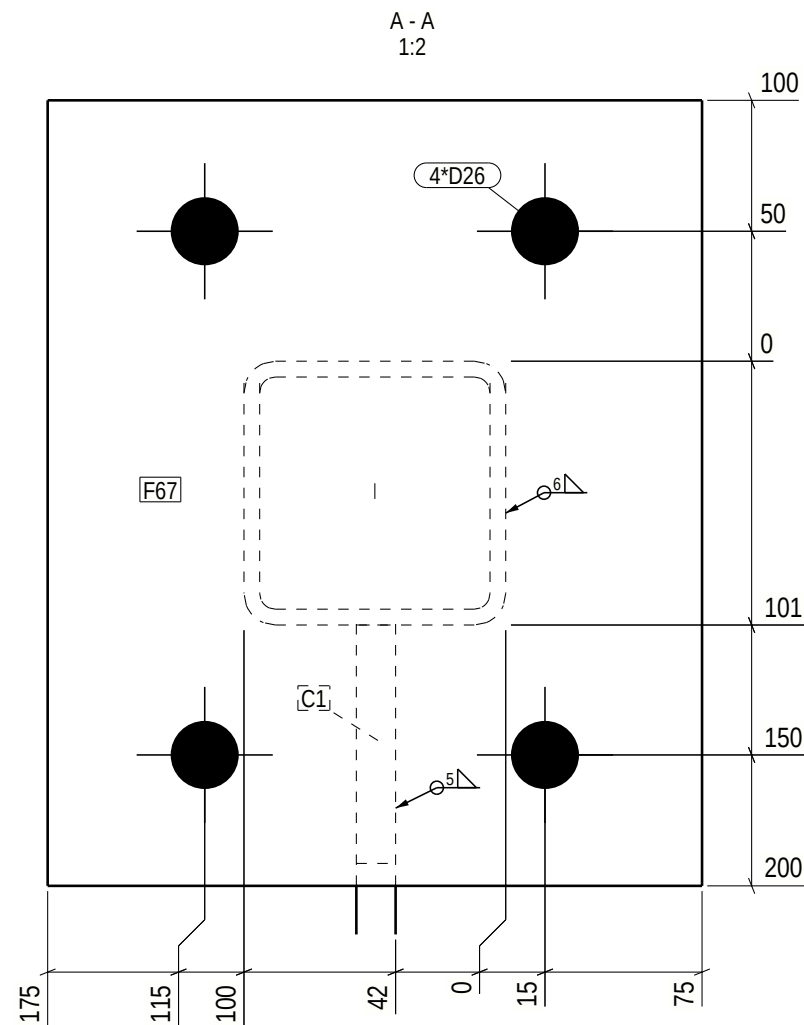

GENERAL NOTES: For your safety, check weight before handling:
0-5kg Light 5-15kg Normal 15+kg Heavy

ALL WELDS ARE 4 UNLESS NOTED ON DRAWING

MATERIAL LIST FOR ASSEMBLY MK'D S.34						
Mark	Profile	Material	No.	Length	Area	Weight
s34	RHS100X100X6	S355J2H	1	3075	1.2	51.9 !!
C1	PL15*140	S355J2	1	146	0.0	2.2
F67	FL20*250	S355J2	1	300	0.2	11.8
F101	FL15*140	S355J2	1	140	0.0	2.3
Total				1.4	68.2	

Finish Class
Standard

Surface treatment info:	Thickness/start point-> length	No.
Overall Painting	C2M RAL7016µm whole	**1



Special
surface treatment



weld a = 4

PHASE	QUANTITY
1	1

* o 3 0 4 8 0 - 1 * DS Skalkonstruktion * A s 3 4 *			
PROJECT	Akkasæter Lager- og vedlikeholdshall	EXEC. CLASS	EXC 2
MEMBER	Søyle	QUANTITY:	1
REVISION	ISSUED: 07.11.2025	DRAFTER: ZLL	PROJECT No 30480-1
	BIM control: SST		DRAWING No. s.34