
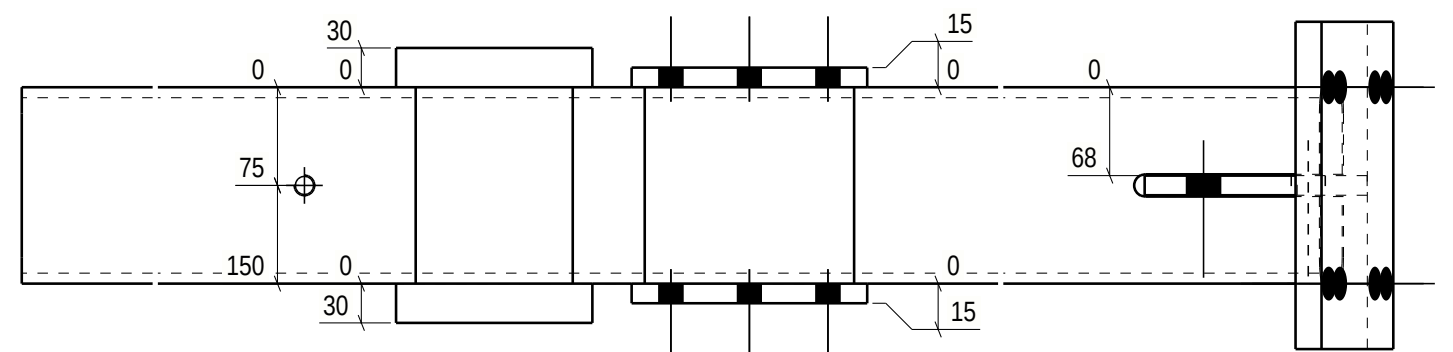
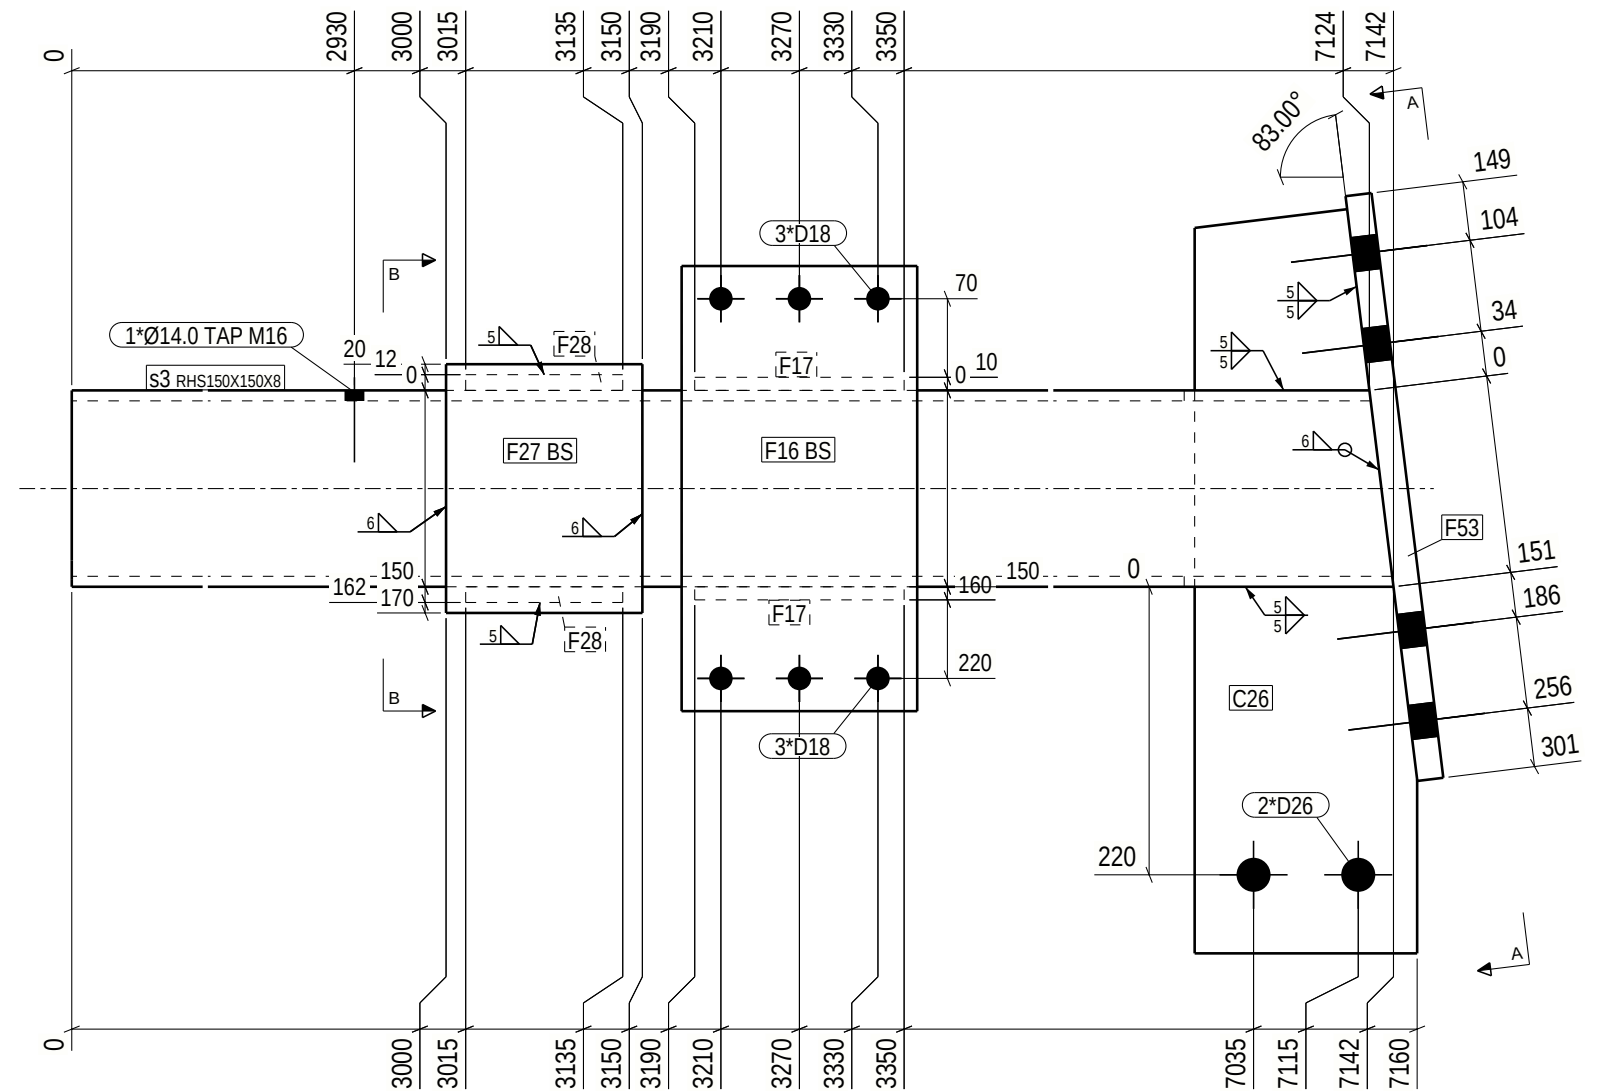


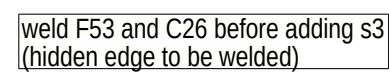

* 030480 - 1 *		 DS		Stalkonstruktion		* A s 3 *	
PROJECT	Akkasæter Lager- og vedlikeholdshall				EXEC. CLASS	EXC 2	
MEMBER	Sølje	QUANTITY:	1	PROJECT No	30480-1		
REVISION	ISSUED: 07.11.2025	DRAFTER: BIM Control	ZLL SST	DRAWING No.	S.3		