

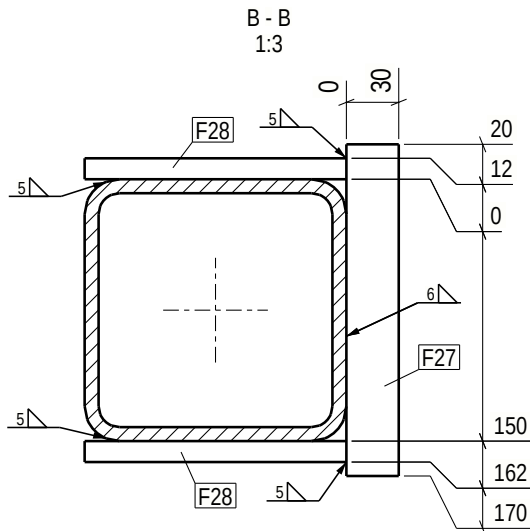
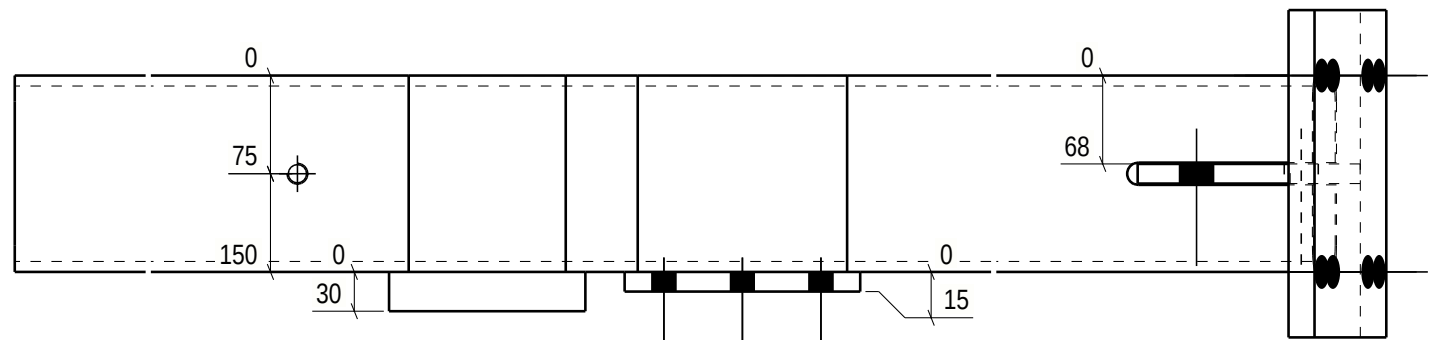


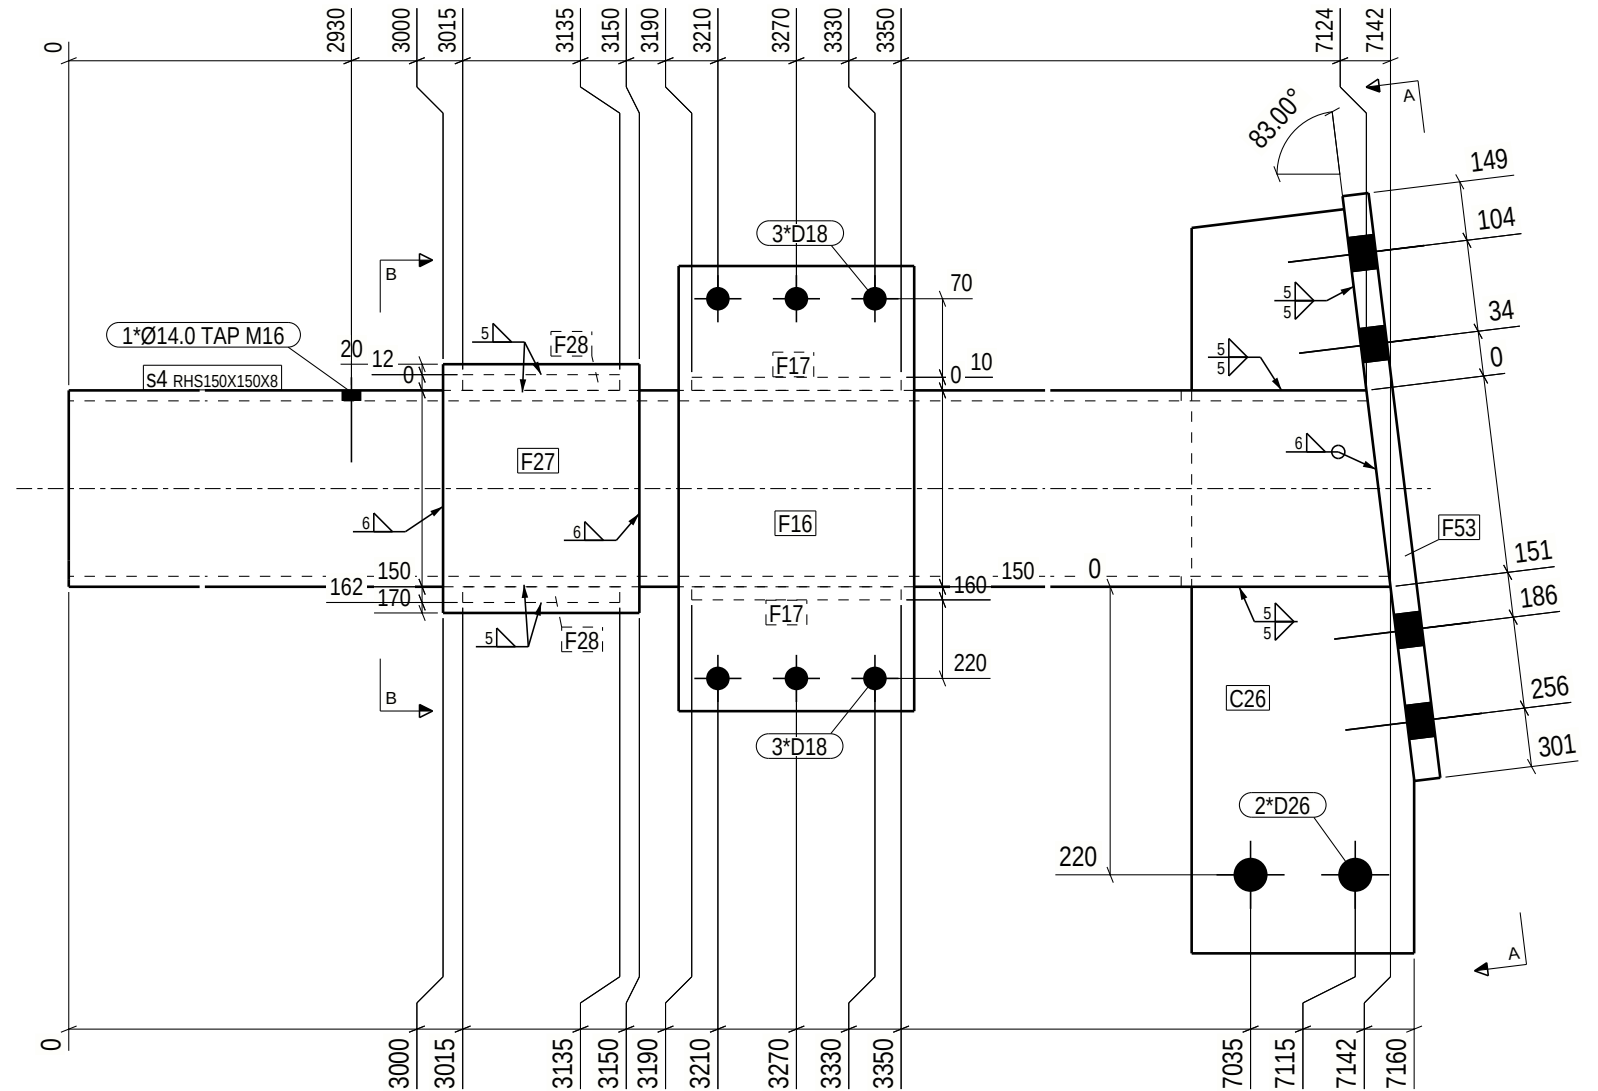

weld F53 and C26 before adding s4  
(hidden edge to be welded)

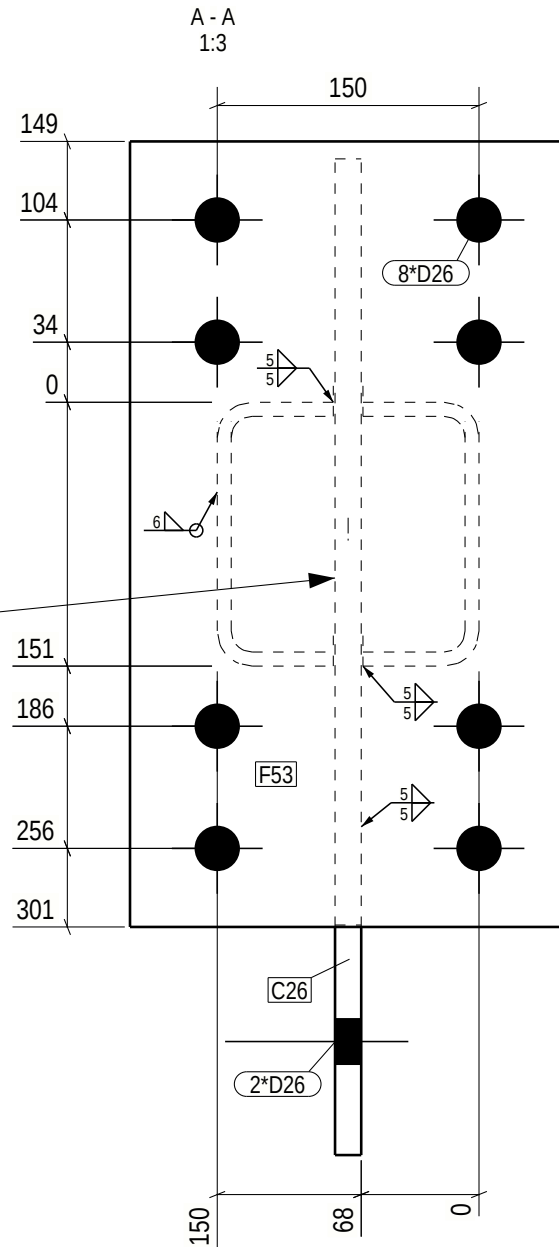

GENERAL NOTES: For your safety, check weight before handling:  
0-5kg Light 5-15kg Normal 15+kg Heavy

ALL WELDS ARE 4 UNLESS NOTED ON DRAWING

MATERIAL LIST FOR ASSEMBLY MK'D S.4

| Mark  | Profile      | Material | No. | Length | Area | Weight   |
|-------|--------------|----------|-----|--------|------|----------|
| s4    | RHS150X150X8 | S355J2H  | 1   | 7142   | 4.1  | 240.7 !! |
| C26   | PL15*170     | S355J2   | 1   | 568    | 0.2  | 9.9      |
| F16   | FL15*180     | S355J2   | 1   | 340    | 0.1  | 7.2      |
| F17   | FL10*150     | S355J2   | 2   | 160    | 0.1  | 1.9      |
| F27   | FL30*150     | S355J2   | 1   | 190    | 0.1  | 6.7      |
| F28   | FL12*120     | S355J2   | 2   | 150    | 0.0  | 1.7      |
| F53   | FL20*250     | S355J2   | 1   | 450    | 0.3  | 17.7 !!  |
| Total |              |          |     | 4.9    |      | 289.3    |

Finish Class  
Standard

|                         |                                |     |
|-------------------------|--------------------------------|-----|
| Surface treatment info: | Thickness/start point-> length | No. |
| Overall Painting        | C2M RAL7016µm whole            | **1 |



Special  
surface treatment



weld a = 4

| PHASE | QUANTITY |
|-------|----------|
| 1     | 1        |

|                                                   |                                      |                  |                      |
|---------------------------------------------------|--------------------------------------|------------------|----------------------|
| * o 3 0 4 8 0 - 1 * DS Skalkonstruktion * A s 4 * |                                      |                  |                      |
| PROJECT                                           | Akkasæter Lager- og vedlikeholdshall | EXEC. CLASS      | EXC 2                |
| MEMBER                                            | Søyle                                | QUANTITY:        | 1 PROJECT No 30480-1 |
| REVISION                                          | ISSUED: 07.11.2025                   | DRAFTER: ZLL SST | DRAWING No. S.4      |