



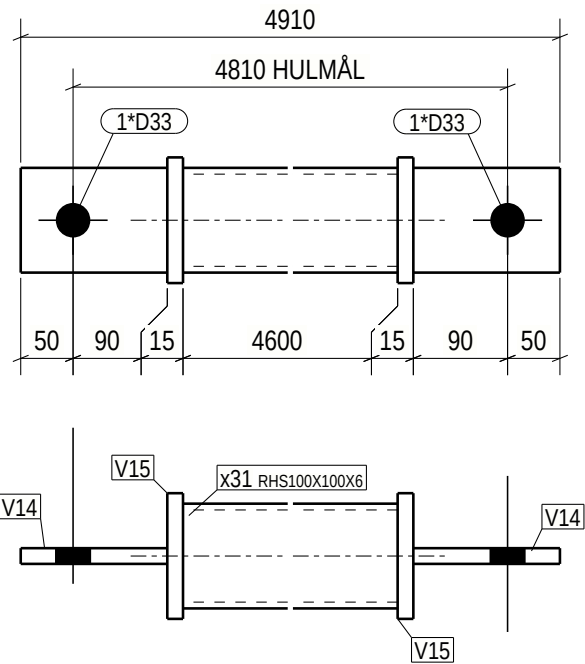

GENERAL NOTES: For your safety, check weight before handling:						
ALL WELDS ARE 4 UNLESS NOTED ON DRAWING						
MATERIAL LIST FOR ASSEMBLY MK'D x.31						
Mark	Profile	Material	No.	Length	Area	Weight
x31	RHS100X100X6	S355J2H	1	4600	1.8	77.8 !!
V14	FL15*100	S355J2	2	140	0.0	1.6
V15	FL15*120	S355J2	2	120	0.0	1.7
Total				1.9	84.5	

Finish Class
Standard

Surface treatment info:	Thickness/start point--> length	No.
Overall Painting	C2M RAL7016µm whole**6	

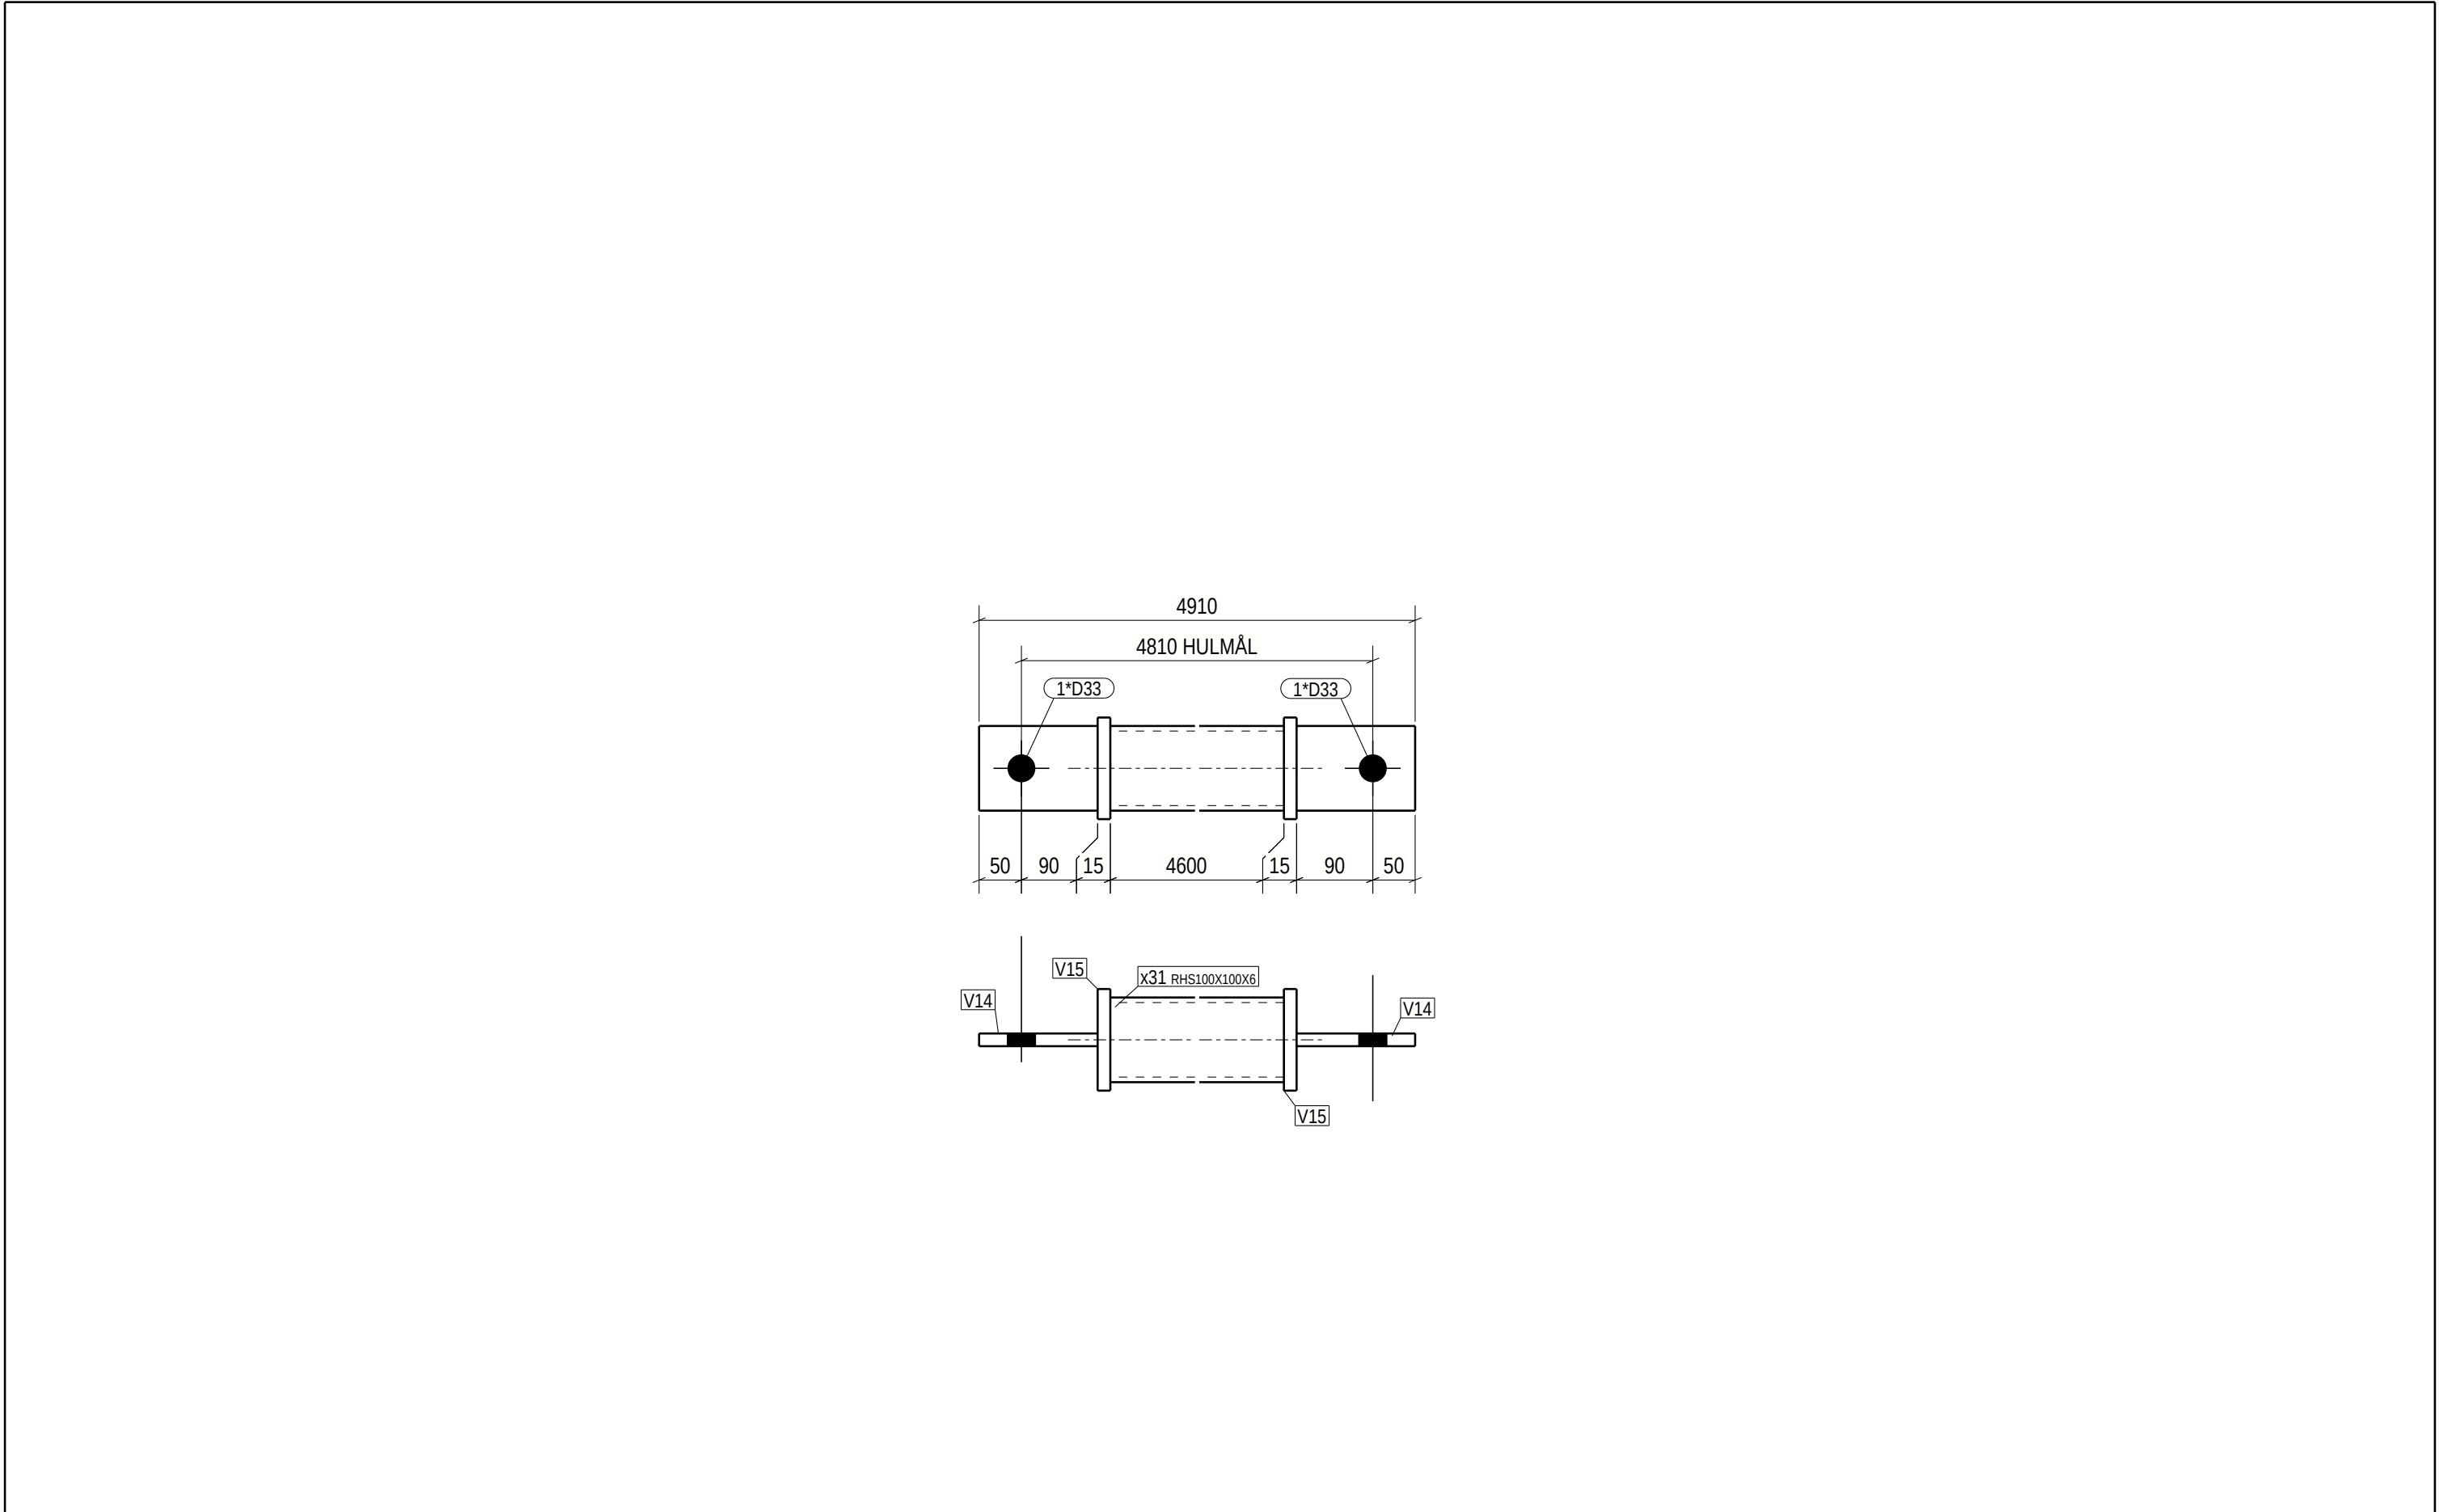

Special
surface treatment



weld a = 4

PHASE	QUANTITY
1	6

* o 3 0 4 8 0 - 1 * DS Stahlkonstruktion * A x 3 1 *			
PROJECT	Akkasæter Lager- og vedlikeholdshall	EXEC. CLASS	EXC 2
MEMBER	Vind-X	QUANTITY:	6
REVISION		ISSUED:	07.11.2025
		DRAFTER:	ZLL
		BIM control:	SST
PROJECT No		30480-1	
DRAWING No.		x.31	