



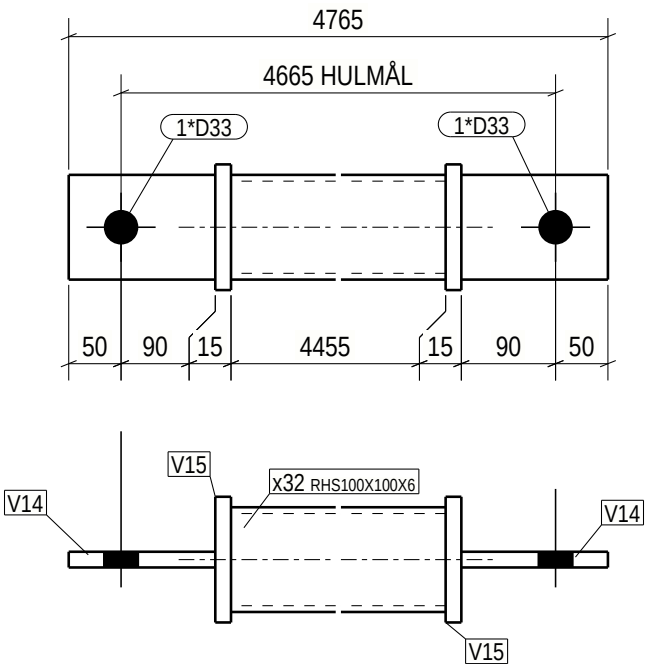

GENERAL NOTES:						
For your safety, check weight before handling:						
0-5kg Light 5-15kg Normal 15+kg Heavy						
ALL WELDS ARE 4 UNLESS NOTED ON DRAWING						
MATERIAL LIST FOR ASSEMBLY MK'D x.32 1 No. Required						
Mark	Profile	Material	No.	Length	Area	Weight
x32	RHS100X100X6	S355J2H	1	4455	1.7	75.4 !!
V14	FL15*100	S355J2	2	140	0.0	1.6
V15	FL15*120	S355J2	2	120	0.0	1.7
Total					1.9	82.0

Finish Class
Standard

Surface treatment info:	Thickness/start point-> length	No.
Overall Painting	C2M RAL7016µm whole***1	

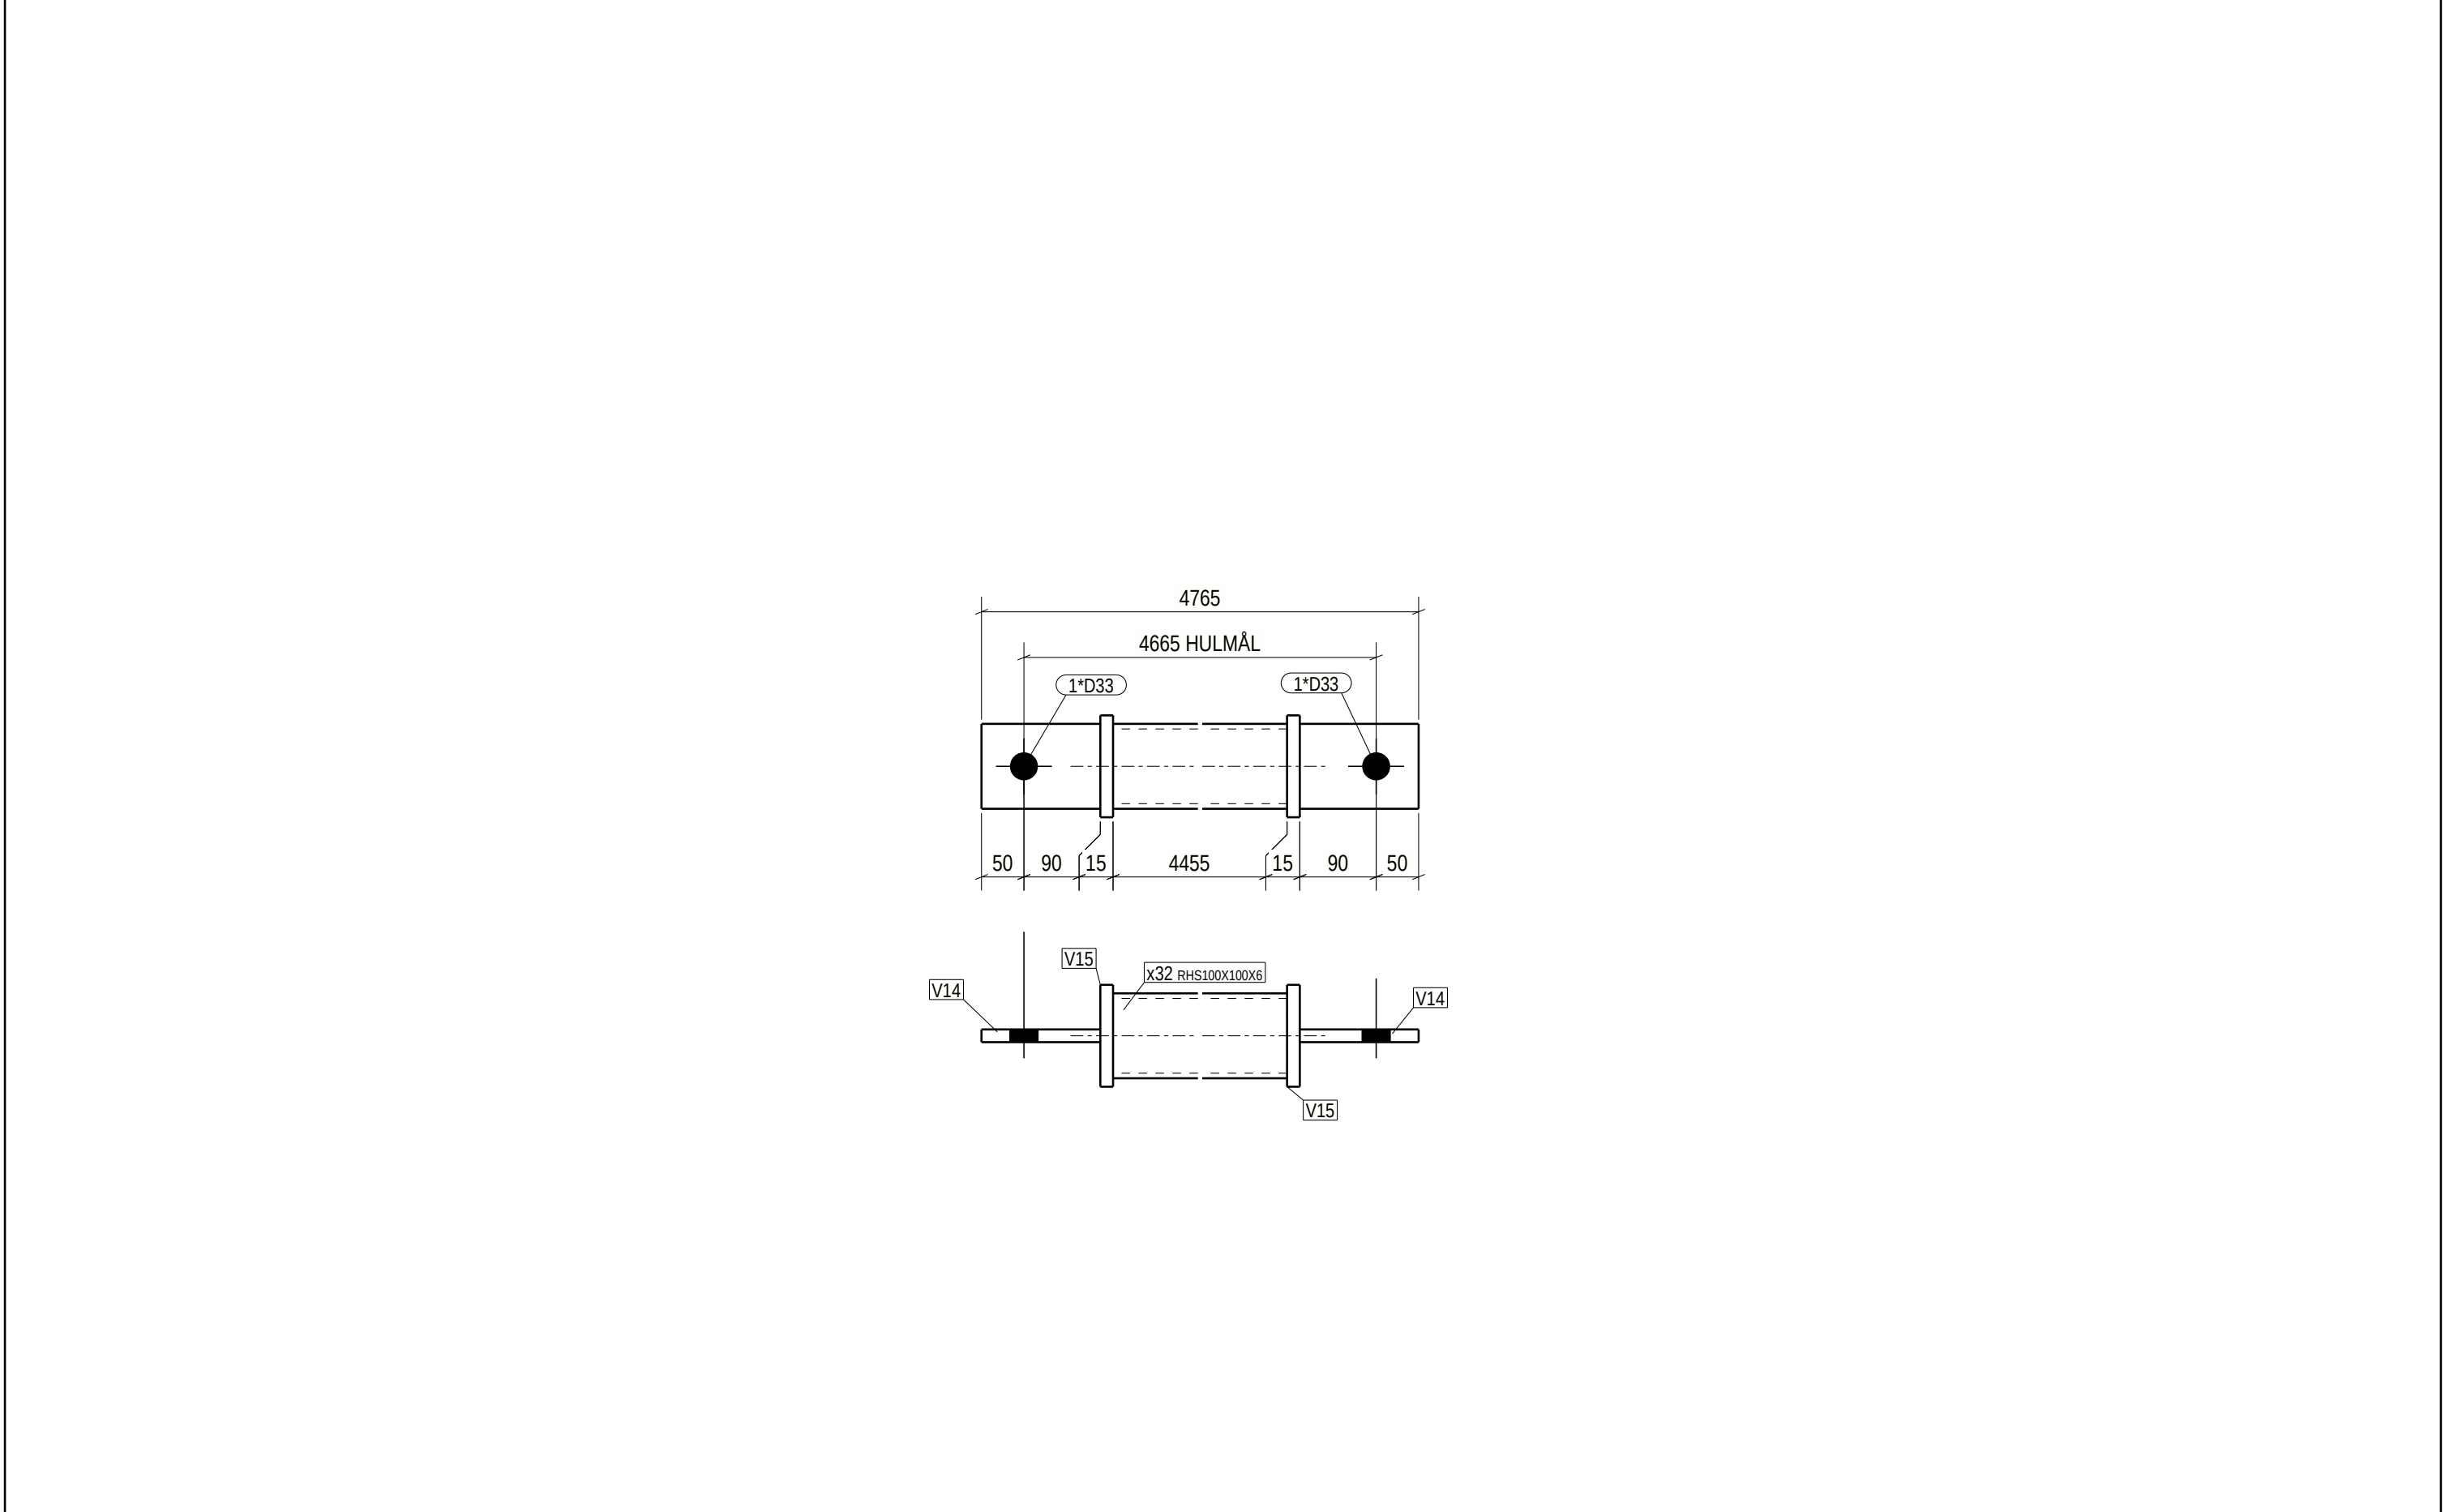

Special
surface treatment



weld a = 4

PHASE	QUANTITY
1	1

* o 3 0 4 8 0 - 1 *  DS <i>Stålkonstruktion</i> * A x 3 2 *					
PROJECT	Akkasæter Lager- og vedlikeholdshall			EXEC. CLASS	EXC 2
MEMBER	Vind-X	QUANTITY:	1	PROJECT No	30480-1
REVISION		ISSUED:	07.11.2025	DRAFTER: ZLL BIM control: SST	DRAWING No. x.32