


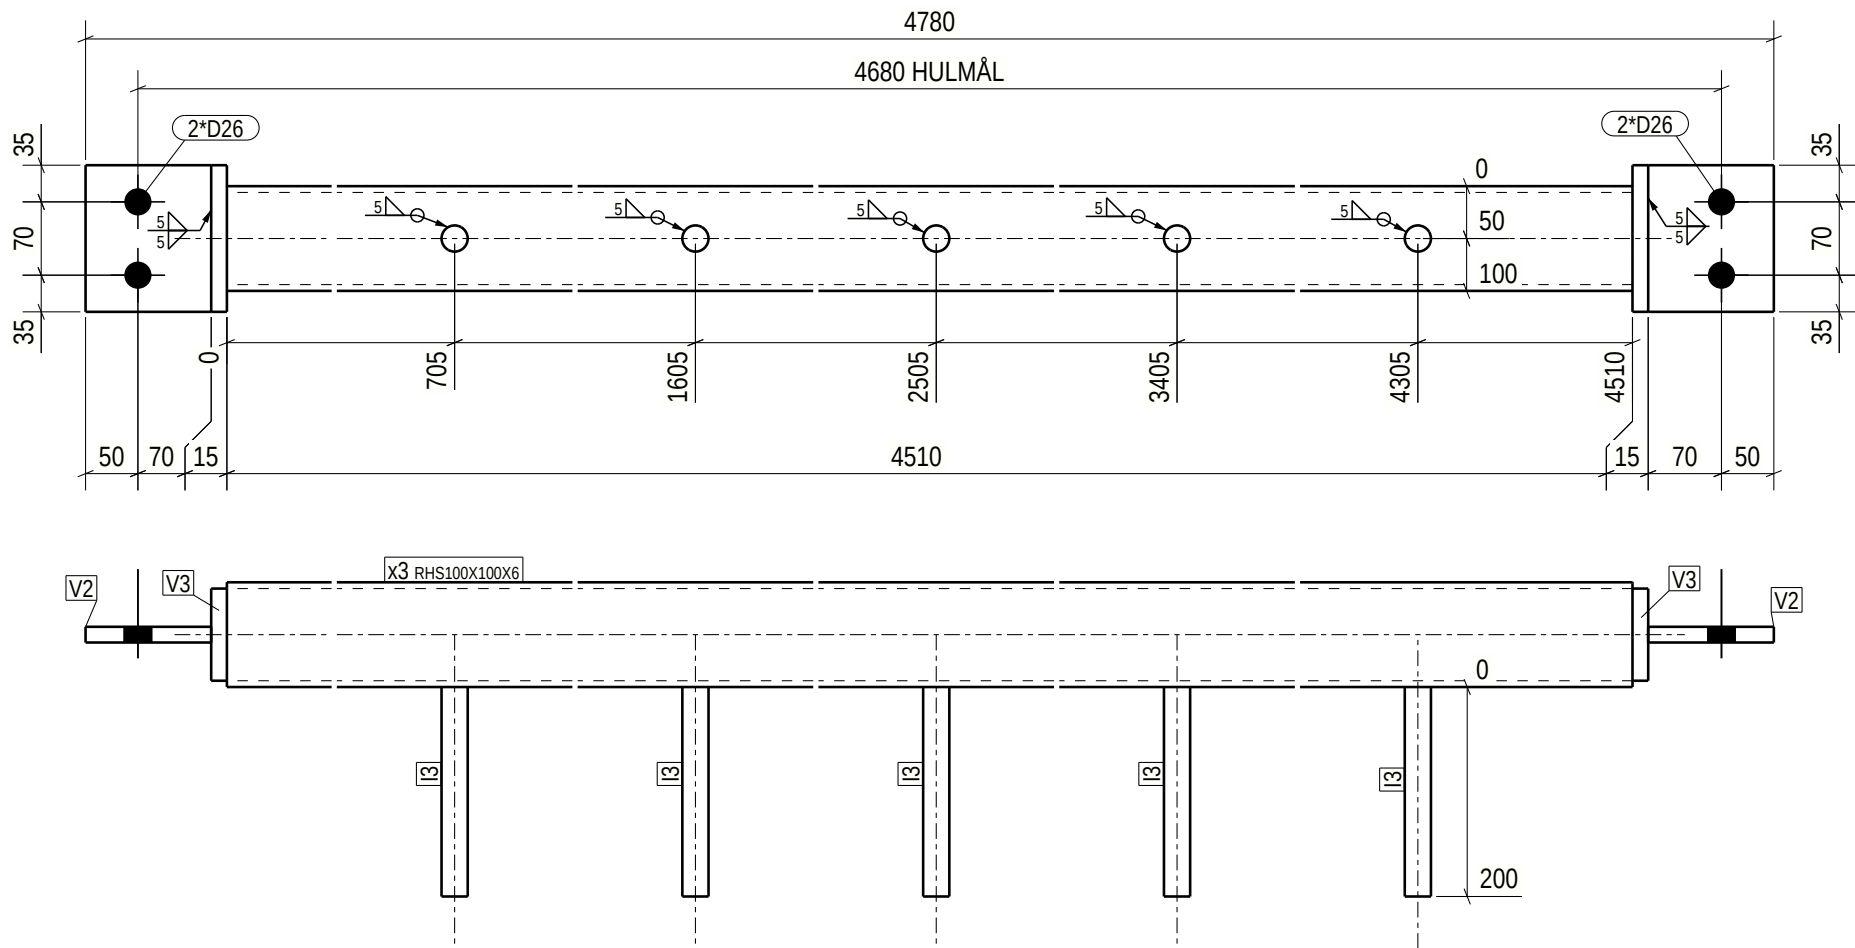

GENERAL NOTES: For your safety, check weight before handling:						
ALL WELDS ARE 4 UNLESS NOTED ON DRAWING						
MATERIAL LIST FOR ASSEMBLY MK'D x.3						
Mark	Profile	Material	No.	Length	Area	Weight
x3	RHS100X100X6	S355J2H	1	4510	1.7	76.3 !!
I3	REBAR25	B550B	5	200	0.0	0.7
V2	FL15*120	S355J2	2	140	0.0	2.0
V3	FL15*88	S355J2	2	140	0.0	1.5
Total					2.0	86.8

Finish Class
Standard

Surface treatment info:	Thickness/start point-> length	No.
Overall Painting	Primerµm whole asse***	1



Special
surface treatment



weld a = 4

PHASE	QUANTITY
1	1

* o 3 0 4 8 0 - 1 * DS Steelkonstruktion * A x 3 *			
PROJECT	Akkasæter Lager- og vedlikeholdshall	EXEC. CLASS	EXC 2
MEMBER	Vind-X	QUANTITY:	1
REVISION	ISSUED: 07.11.2025	DRAFTER: ZLL	PROJECT No 30480-1
		BIM control: SST	DRAWING No. x.3